

CONSTRUCTION PLANS FOR PROPOSED
SINGLE-FAMILY RESIDENCE
264 CROCKETT RD WEATHERFORD TX 76088

SITE INFORMATION

- JURISDICTION: -
- ZONING: RESIDENTIAL
- SETBACKS:
 - 1. FRONT: -
 - 2. SIDES: -
 - 3. REAR: -
- THIS PROJECT IS EXEMPT FROM THE WATERSHED PROTECTION CLASSIFICATION AND IS NOT LOCATED IN THE 100-YEAR FLOODPLAIN
- THIS LOT IS RECORDED IN PARKER COUNTY.
- TYPE OF CONSTRUCTION: II-B
- TOTAL FLOOR AREA: 5422.8SQ.FT
- BUILDING MAX. HEIGHT: 24 FT
- LOT AREA:
- F.A.R:
- NUMBER OF STORIES: I
- SPRINKLER SYSTEM: NO
- OCCUPANCY CLASSIFICATION: RESIDENTIAL

APPLICABLE CODES:

- 2018 INTERNATIONAL BUILDING CODE (IBC)
- 2018 INTERNATIONAL RESIDENTIAL CODE (IRC)
- 2018 INTERNATIONAL MECHANICAL CODE (IMC)
- 2018 INTERNATIONAL PLUMBING CODE (IPC)
- 2018 UNIFORM PLUMBING CODE (UPC)
- 2017 NATIONAL ELECTRICAL CODE (NEC)

SHEET INDEX

- A001 COVER SHEET
- A002 GENERAL NOTES
- A100 FLOOR PLAN
- A101 ROOF PLAN
- A200 ELEVATION
- A300 DETAILS
- A301 DOOR SCHEDULE

REVIEWED BY:

DIRECTOR OF DEVELOPMENT SERVICES	DATE
DEPARTMENT OF PUBLIC WORKS	DATE
CITY ENGINEER	DATE



PERPECTIVE



SITE LOCATION

Bauen Consultants
ENGINEERING & ARCHITECTURE

CONTACT: 773-937-0712
ADDRESS: 128 DAV LN LONDON KY 40741

THIS DRAWING IS PROVIDED AS AN INSTRUMENT OF SERVICE BY THE ARCHITECT AND IS INTENDED FOR USE ON THIS PROJECT ONLY. THE DRAWING REMAINS THE PROPERTY OF THE ARCHITECT AND SHALL BE RETURNED TO HIM/HER UPON COMPLETION OF THE CONSTRUCTION WORK. PURSUANT TO THE ARCHITECTURAL WORKS COPYRIGHT PROTECTION ACT OF 1990, ALL DRAWINGS, SPECIFICATIONS, IDEAS, AND DESIGNS, INCLUDING THE OVERALL FORM, ARRANGEMENT, AND COMPOSITION OF THE SPACES, AND ELEMENTS APPEARING HEREIN, CONSTITUTES THE COPYRIGHT WORK OF THE ARCHITECT. ANY REPRODUCTION, USE, OR DISCLOSURE OF INFORMATION CONTAINED HEREIN WITHOUT PRIOR WRITTEN CONSENT OF THE ARCHITECT IS STRICTLY PROHIBITED.

GENERAL PLAN NOTES

OWNER TO PERFORM THE FOLLOWING BEFORE CONSTRUCTION COMMENCES. DESIGNER ASSUMES NO LIABILITY FOR CONSTRUCTION:

- BUILDER OR CONTRACTOR SHALL VERIFY ALL DIMENSIONS PRIOR TO PROCEEDING WITH CONSTRUCTION.
- BUILDER OR CONTRACTOR SHALL VERIFY COMPLIANCE WITH CITY AMENDMENTS TO IRC.
- DO NOT USE SCALED DIMENSIONS; USE ONLY DIMENSIONS AS CALLED OUT. WHEN NO DIMENSION IS PROVIDED, CONSULT WITH THE OWNER BEFORE PROCEEDING WITH WORK.
- CONTRACTOR SHALL VERIFY ALL EXISTING CONDITIONS, SITE UTILITY SERVICES AND DIMENSIONS AND NOTIFY ARCHITECT OF DISCREPANCIES THAT MAY AFFECT THE EXECUTION OF THE WORK BEFORE PROCEEDING.
- OMISSIONS OR CONFLICTS WITHIN THE DRAWINGS, NOTES OR DETAILS SHALL BE REPORTED THE OWNER BEFORE PROCEEDING WITH WORK.
- DETAILS TAKE PRECEDENCE DRAWING NOTES

REVISION SCHEDULE		
REV. #	NAME	DATE

PROPOSED ONE STORY FARM HOUSE

264 CROCKETT RD WEATHERFORD TX 76088

COVER SHEET

DATE	01.31.2025
A001	
SCALE	AS INDICATED ON I1X17

7/14/2024 9:40:01 PM

I. SCOPE OF DOCUMENTS

THESE DRAWINGS INDICATE THE GENERAL SCOPE OF THE PROJECT IN TERMS OF THE ARCHITECTURAL DESIGN INTENT, THE DIMENSIONS OF THE BUILDING, THE MAJOR ARCHITECTURAL ELEMENTS AND THE TYPE OF STRUCTURAL SYSTEM, ON THE BASIS OF THE GENERAL SCOPE INDICATED OR DESCRIBED. FRAMING AND FINISH WORK TO MATCH EXISTING WILL BE PROVIDED WHETHER SPECIFICALLY CALLED FOR OR NOT WHERE EQUIPMENT OR ITEMS ARE REMOVED. THE CONTRACTOR SHALL FURNISH ALL ITEMS REQUIRED FOR THE PROPER EXECUTION AND COMPLETION OF THE WORK. WHERE HEREAFTER DESCRIBED, "PROVIDED" MEANS TO PROVIDE AND INSTALL.

CONSTRUCTION FROM DRAWINGS OF THIS BUILDING STRUCTURE & FOUNDATION SHALL BE BUILT FROM THE STRUCTURAL DRAWINGS. ANY CONFLICTS BETWEEN THE STRUCTURAL & ARCHITECTURAL SHALL BE BROUGHT TO THE ATTENTION OF THE ARCHITECT TWO DAYS PRIOR TO LAYOUT OF ANY PORTION IN CONFLICT.

2. INTERPRETATION AND MISUNDERSTANDINGS
WORK NOT CLEARLY DETAILED SHOWN OR SPECIFIED SHALL BE SAME AS SIMILAR PARTS THAT ARE SHOWN OR SPECIFIED. LARGE SCALE DRAWINGS SHALL TAKE PRECEDENCE OVER SMALLER SCALE DRAWINGS. SPECIFICATIONS SHALL GOVERN AS TO MATERIALS, WORKMANSHIP, AND INSTALLATION PROCEDURES. IF CONTRACTOR OBSERVES THAT DRAWINGS AND SPECIFICATIONS ARE IN CONFLICT, HE OR SHE SHALL PROMPTLY NOTIFY THE ARCHITECT IN WRITING.

WHEN DETAIL OR INFORMATION IS NOT CLEAR, THE CONTRACTOR SHALL ASK FOR CLARIFICATION DURING BIDDING (10 DAYS MIN. PRIOR TO CLOSE OF BIDS) OR CONSTRUCT PER THE ARCHITECTS CLARIFICATION WHEN MADE DURING CONSTRUCTION.

3. CONFLICTS WITHIN CONTRACT DOCUMENTS
THE CONTRACTOR SHALL VERIFY ALL DIMENSIONS AND SITE CONDITIONS DURING BIDING PHASE. SHOULD A DISCREPANCY BE IDENTIFIED IN THE SPECIFICATIONS OR DRAWINGS, OR IN THE WORK DONE BY OTHERS FROM THE CONTRACT DOCUMENTS THAT AFFECT ANY WORK, NOTIFY THE ARCHITECT IN WRITING AT ONCE FOR INSTRUCTION ON HOW TO IF PROCEED. IF THE CONTRACTOR PROCEEDS WITH THE WORK AFFECTED WITHOUT INSTRUCTIONS FROM THE ARCHITECT, THE CONTRACTOR SHALL MAKE GOOD ANY RESULTING DAMAGE OR DEFECT TO THE SATISFACTION OF THE ARCHITECT.

4. SUBSTITUTIONS AND ALTERNATE DESIGN CONCEPTS
COSTS FOR EVALUATION OR STUDY BY THE ARCHITECT OR ENGINEER OF SUBSTITUTED MATERIALS OR METHODS OF CONSTRUCTION SHALL BE THE RESPONSIBILITY OF THE CONTRACTOR OR THE ORIGINATOR OF THE ALTERNATE.

5. CHANGES
20. CUTTING REPAIRING AND PATCHING
THE CONTRACTOR SHALL DO ALL CUTTING, FITTING, OR PATCHING OF HIS WORK THAT MAY BE REQUIRED TO MAKE ITS SEVERAL PARTS FIT TOGETHER PROPERLY AND SHALL NOT ENDANGER ANY OTHER WORK BY CUTTING, EXCAVATING, OR OTHERWISE ALTERING THE TOTAL WORK OR ANY PART OF IT. ALL PATCHING, REPAIRING AND REPLACING OF MATERIALS AND SURFACES, CUT OR DAMAGED IN EXECUTION OF WORK, SHALL BE DONE WITH APPLICABLE MATERIALS SO THAT SURFACES REPLACED SHALL, UPON COMPLETION, MATCH SURROUNDING SIMILAR SURFACES.

21. INSULATION
INSULATE THE FOLLOWING WHETHER NOTED ON THE DRAWINGS OR NOT: ROOFS, EXTERIOR WALLS, WALLS AND CEILINGS BETWEEN HEATED AND NON-HEATED SPACES, AND FLOORS, STAIRS, ETC. BETWEEN HEATED AND NON-HEATED ACCESSIBLE SPACES. INSULATION SHALL BE R-13 WALLS/R-38 ROOF UNLESS NOTED OTHERWISE ON THE DRAWINGS. PER ZONE 2B

NO CHANGE IS APPROVED BY THE ARCHITECT OR ENGINEER UNLESS DEFINED AND DETAILED IN WRITING AND/OR BY

DRAWING CHANGE NOTICE (DCN). ANY VERBAL COMMENTS BY PHONE OR IN PERSON ARE NOT CONSIDERED BINDING. THE CONTRACTOR WILL TAKE ALL RESPONSIBILITY FOR ALL CHANGES NOT APPROVED IN WRITING BY THE ARCHITECT AND/OR THE ENGINEER.

6. OWNER AND TENANT CONSIDERATIONS
THE FOLLOWING ARE INSTRUCTIONS FOR WORK TO BE PERFORMED IN OR AROUND EXISTING BUILDINGS AND IN SITUATIONS WHERE THE OWNER OCCUPIES THE BUILDING PRIOR TO COMPLETION:

- A. CONTRACTOR SHALL CONDUCT ALL HIS OPERATIONS IN A MANNER TO AFFORD NO HAZARD TO OWNER’S PERSONNEL OR VISITORS. THE CONTRACTOR WILL BE REQUIRED TO COOPERATE WITH OWNER IN SCHEDULING NEW CONSTRUCTION SO THAT INTERRUPTIONS OR NORMAL USAGE OF EXISTING STRUCTURE WILL BE KEPT TO A MINIMUM.
- B. CONTRACTOR SHALL NOT DISRUPT EXISTING SERVICES AND/OR UTILITIES FOR ANY REASON WITHOUT OBTAINING OWNER’S PRIOR APPROVAL AND INSTRUCTION IN EACH CASE. CONTRACTOR MUST CONFORM TO OWNER’S REQUIREMENTS AS TO THE EXACT TIME SUCH INTERRUPTIONS CAN BE ALLOWED AND THE LENGTH OF TIME THE UTILITY / SERVICES CAN BE SHUT OFF. OWNER MAY REQUIRE UTILITY SHUT DOWN TIMES AT NIGHT OR WEEKENDS.
- C. CONTRACTOR WILL BE ALLOWED LIMITED ACCESS TO REQUIRED AREAS IN ORDER TO FIELD MEASURE, DEVELOP SHOP DRAWINGS AND VERIFY EXISTING CONDITIONS IN ORDER TO MAKE FULL USE OF THE BIDDING & CONSTRUCTION PERIOD.

7. DIMENSIONS
- A. ALL DIMENSIONS SHALL TAKE PRECEDENCE OVER SCALE. THE DRAWINGS SHALL NEVER BE SCALED. THE ARCHITECT SHALL BE CONTACTED FOR INCORRECT OR MISSING DIMENSIONS 2 DAYS PRIOR TO LAYOUT WORK.
 - B. ALL DIMENSIONS ARE TO FACE OF FRAMING UNLESS OTHERWISE NOTED.
 - C. CEILING HEIGHT DIMENSIONS ARE FROM FINISH FLOOR TO FINISH FACE OF CEILING.
 - D. ALL DIMENSIONS ON PLANS FOR ANY BUILT-IN SYSTEM (STOREFRONT, CABINETS, SEATING, PARTITIONS, ETC.) ARE FOR BIDDING PURPOSES ONLY. EXACT DIMENSIONS SHALL BE TAKEN AT THE SITE WITH WALLS IN PLACE PRIOR TO MANUFACTURING AND INSTALLATION.

8. CONSTRUCTION MEANS & METHODS DURING CONSTRUCTION
THE ARCHITECT WILL NOT BE RESPONSIBLE FOR OR HAVE CONTROL OR CHARGE OF CONSTRUCTION MEANS, METHODS, TECHNIQUES, SEQUENCES OR PROCEDURES, OR FOR SAFETY PRECAUTIONS AND PROGRAMS IN CONNECTION WITH THE WORK, AND NEITHER WILL THE ARCHITECT BE RESPONSIBLE FOR THE CONTRACTOR’S FAILURE TO CARRY OUT THE WORK IN ACCORDANCE WITH THE CONTRACT DOCUMENTS.

29. DISCLAIMER
BY USING THESE PERMIT READY CONSTRUCTION DOCUMENTS, THE RECIPIENT IS ACKNOWLEDGING ACCEPTANCE OF THE FOLLOWING CONDITIONS:

- 1. THE USE OF THIS INFORMATION IS RESTRICTED TO THE ORIGINAL PROJECT FOR WHICH IT WAS PREPARED FOR. THIS DOES NOT ELIMINATE OR REDUCE THE RECIPIENT’S RESPONSIBILITY TO VERIFY ANY AND ALL INFORMATION RELEVANT TO THE RECIPIENT’S WORK AND RESPONSIBILITY ON THIS PROJECT. PRODUCER OF THE DRAWINGS SHALL NOT BE RESPONSIBLE FOR TRANSLATION ERRORS.
- 2. THE RECIPIENT RECOGNIZES AND ACKNOWLEDGES THAT THE USE OF THIS INFORMATION WILL BE AT THEIR SOLE RISK AND WITHOUT ANY LIABILITY OR LEGAL EXPOSURE TO PRODUCER OF THE DRAWINGS. NO WARRANTIES OF ANY NATURE, WHETHER EXPRESS OR IMPLIED, SHALL ATTACH TO THESE DOCUMENTS AND THE INFORMATION

CONTAINED THEREON. ANY USE, REUSE, OR ALTERATION OF THESE DOCUMENTS BY THE RECIPIENT OR BY OTHERS WILL BE AT THE RECIPIENT’S RISK AND FULL LEGAL RESPONSIBILITY. FURTHERMORE, THE RECIPIENT WILL, TO THE FULLEST EXTENT PERMITTED BY LAW, INDEMNIFY AND HOLD PRODUCER OF THE DRAWINGS HARMLESS FROM ANY AND ALL CLAIMS, SUITS, LIABILITY, DEMANDS, JUDGMENTS, OR COSTS ARISING OUT OF OR RESULTING THERE FROM ON ACCOUNT OF ANY INJURY, DEATH, DAMAGE OR LOSS TO PERSONS OR PROPERTY.

- 3. THE DESIGNS REPRESENTED BY THESE DRAWINGS ARE COPYRIGHTED AND ARE SUBJECT TO COPYRIGHT PROTECTION. IF THE RECIPIENT DOES NOT AGREE WITH THE ABOVE CONDITIONS, DO NOT PROCEED BEYOND THIS DISCLAIMER.
- 9. EQUIPMENT LOCATIONS
 - A. THE LOCATIONS OF APPARATUS AND EQUIPMENT INDICATED ON THE DRAWINGS ARE SCHEMATIC ONLY, AND SHALL BE MODIFIED TO MEET THE EXISTING ARCHITECTURAL, MECHANICAL AND STRUCTURAL CODES AND CONDITIONS AS REQUIRED WITHOUT ADDITIONAL COST TO THE OWNER.
 - B. THE CONTRACTOR SHALL INSTALL ALL PIPING AND EQUIPMENT IN A PROPER MANNER AND IN LOCATIONS AVOIDING ALL OBSTRUCTIONS, PRESERVING HEADROOM AND KEEPING OPENINGS AND PASSAGEWAYS CLEAR. THE CONTRACTOR SHALL MAKE CHANGES, WITH OWNER’S APPROVAL, IN LOCATIONS OF EQUIPMENT AND MATERIALS, WHICH MAY BE NECESSARY IN ORDER TO ACCOMPLISH THESE ENDS, WITHOUT ADDITIONAL COST TO THE OWNER.
 - C. E ELECTRICAL DRAWINGS ARE DIAGRAMMATIC TO THE EXTENT THAT OFFSETS, BENDS, SPECIAL FITTINGS AND EXACT LOCATIONS ARE NOT INDICATED. THE CONTRACTOR SHALL CAREFULLY STUDY THE DRAWINGS, AND THE PREMISES, IN ORDER TO DETERMINE THE BEST METHODS, EXACT LOCATION, ROUTES, BUILDING OBSTRUCTIONS, ETC. THE CONTRACTOR SHALL INCLUDE THE INSTALLATION OF ALL EQUIPMENT IN AVAILABLE LOCATIONS. WHERE CHANGES IN LOCATION ARE SIGNIFICANT, REVISIONS SHALL BE ISSUED AS A CHANGE ORDER. ANY CHANGES MUST BE COORDINATED BY THE GENERAL CONTRACTOR’S SUPERINTENDENT.

10. SHOP DRAWINGS / SUBMITTALS
CONTRACTOR SHALL VERIFY ALL FIELD DIMENSIONS FOR EXISTING CONDITIONS ON THE CONTRACT DOCUMENTS. THE CONTRACTOR SHALL SUBMIT COPIES TO THE ARCHITECT/ENGINEER OF ALL FABRICATION AND PLACEMENT DRAWINGS, SCHEDULES, AND MATERIALS LIST REQUIRED FOR THE WORK OF VARIOUS TRADES. SUBMITTALS SHALL BE REVIEWED AND STAMPED BY THE CONTRACTOR PRIOR TO DELIVERY TO THE ARCHITECT/ENGINEER. THIS SHALL BE DONE WITH SUCH PROMPTNESS AS TO CAUSE NO DELAY IN HIS OWN WORK OR IN THAT OF ANY OTHER CONTRACTOR. THE CONTRACTOR SHALL IN WRITING, CALL TO THE ARCHITECT/ENGINEER’S ATTENTION DEVIATIONS IN THE DRAWINGS AT THE TIME OF SUBMISSION AND SECURE HIS WRITTEN APPROVAL FOR THEM. THE ARCHITECT/ENGINEER SHALL REVIEW SUCH SCHEDULES AND DRAWINGS ONLY FOR CONFORMANCE WITH THE DESIGN INTENT OF THE PROJECT, AND COMPLIANCE WITH INFORMATION GIVEN IN THE CONTRACT DOCUMENTS. THE CONTRACTOR SHALL MAKE ANY CORRECTIONS REQUIRED BY THE ARCHITECT/ENGINEER, RETAIN FILE COPIES AND FURNISH SUCH OTHER COPIES AS MAY BE NEEDED FOR CONSTRUCTION. THE ARCHITECT/ENGINEER’S ACCEPTANCE OF SUCH DRAWINGS OR SPECIFICATIONS SHALL NOT RELIEVE THE CONTRACTOR FROM RESPONSIBILITY FOR ERRORS IN SHOP DRAWINGS OR SCHEDULES. SUBMITTALS SHALL BE SENT TO THE ARCHITECT/ENGINEER AS FOLLOWS:

- WHEN REQUESTED BY ARCHITECT/ENGINEER.
- WHEN REQUIRED PER THE CONTRACT DOCUMENTS.
- FOR APPROVAL OF DEVIATIONS OR CLARIFICATION OF THE SPECIFIED DESIGN.
- FOR APPROVAL OF “ OR EQUALS” .

11. CODES
ALL CONSTRUCTION AND MATERIALS SHALL COMPLY WITH THE MOST RESTRICTIVE REQUIREMENTS OF APPLICABLE CODES INCLUDING BUT NOT LIMITED TO THE LATEST ADOPTED EDITION IBC, IRC, NTA, ACI, ASCE AND LOCAL CODE AUTHORITIES. ALL CODES REFERRED TO IN THESE DOCUMENTS SHALL BE UNDERSTOOD TO MEAN THE LATEST ADOPTED EDITION.

12. BUILDING LOCATION
THE CONTRACTOR SHALL BE RESPONSIBLE FOR THE ACCURATE PLACEMENT OF THE BUILDING ON THE SITE.

13. JOB SITE USE AND CLEANUP
THE CONTRACTOR SHALL CONFINЕ HIS OPERATIONS ON THE SITE TO AREAS PERMITTED BY THE OWNER. THE WORK SHALL BE DONE IN ACCORDANCE WITH APPLICABLE LAWS, LOCAL ORDINANCES, PERMITS AND THE CONTRACT DOCUMENTS. THE JOB SITE SHALL BE MAINTAINED IN A CLEAN, ORDERLY CONDITION FREE OF DEBRIS AND LITTER, AND SHALL NOT BE UNREASONABLY ENCUMBERED WITH ANY MATERIALS OR EQUIPMENT. EACH SUBCONTRACTOR, ON A DAILY BASIC, SHALL REMOVE ALL TRASH AND DEBRIS RESULTING FROM HIS OPERATION.

14. PERMITS
THE GENERAL BUILDING PERMIT AND PLAN CHECK SHALL BE SECURED BY GENERAL CONTRACTOR AND PAID BY THE OWNER. ALL OTHER PERMITS SHALL BE SECURED AND PAID FOR BY THE SUBCONTRACTOR DIRECTLY RESPONSIBLE.

15. PROTECTION OF WORK
ALL FINISH MATERIALS SHALL BE PROTECTED AT ALL TIMES AGAINST SUBSEQUENT DAMAGE, UNTIL FINAL ACCEPTANCE BY THE ARCHITECT OR OWNER AT A SUBSTANTIAL COMPLETION. PRIOR TO THIS ACCEPTANCE, ALL DAMAGED ITEMS TO BE REPAIRED, AT NO COST TO OWNER, BY CONTRACTOR.

16. DUCT, PIPING AND CONDUIT ENCLOSURES
WHERE LARGER STUDS OR FURRING ARE REQUIRED TO COVER OR ENCLOSE DUCTS, PIPING AND CONDUITS, THE LARGER STUD SIZE OR FURRING SHALL EXTEND THE FULL WALL WIDTH AND LENGTH, FOR A FLUSH AND CONTINUOUS SURFACE, WHERE THE ENCLOSURE OCCURS.

17. PAINTING
GENERAL INTENT: PAINT ALL INTERIOR AND EXTERIOR EXPOSED SURFACES (INCLUDING EXPOSED STRUCTURE, PIPES AND DUCTS) EXCEPT WHERE SPECIFICALLY NOTED AS NOT TO BE PAINTED. OBVIOUS ITEMS SUCH AS GLASS, CARPET, FLOOR & WALL TILE, SUSPENDED CEILING TILES, AND HARDWARE SHALL NOT BE PAINTED, UNLESS INDICATED. PAINT ALL REQUIRED SURFACES WITH THE MANUFACTURER’S RECOMMENDED NUMBER OF COATS EXCEPT FOR EXCLUDED MATERIALS MENTIONED ABOVE, OR MATERIALS CALLING FOR A PRE FINISHED MANUFACTURERS FINISH. THE CONTRACTOR SHALL PROVIDE FOR PROTECTION OF FINISHES NOT TO RECEIVE PAINT. FOR BIDDING PURPOSES BENJAMIN MOORE -HISTORICAL COLORS” TO BE USED.

Bauen Consultants
ENGINEERING & ARCHITECTURE

CONTACT: 773-937-0712
ADDRESS:128 DAV LN LONDON KY 40741

THIS DRAWING IS PROVIDED AS AN INSTRUMENT OF SERVICE BY THE ARCHITECT AND IS INTENDED FOR USE ON THIS PROJECT ONLY. THE DRAWING REMAINS THE PROPERTY OF THE ARCHITECT AND SHALL BE RETURNED TO HIM/HER UPON COMPLETION OF THE CONSTRUCTION WORK. PURSUANT TO THE ARCHITECTURAL WORKS COPYRIGHT PROTECTION ACT OF 1990, ALL DRAWINGS, SPECIFICATIONS, IDEAS, AND DESIGNS, INCLUDING THE OVERALL FORM, ARRANGEMENT, AND COMPOSITION OF THE SPACES, AND ELEMENTS APPEARING HEREIN, CONSTITUTES THE COPYRIGHT WORK OF THE ARCHITECT. ANY REPRODUCTION, USE, OR DISCLOSURE OF INFORMATION CONTAINED HEREIN WITHOUT PRIOR WRITTEN CONSENT OF THE ARCHITECT IS STRICTLY PROHIBITED.

GENERAL PLAN NOTES

- OWNER TO PERFORM THE FOLLOWING BEFORE CONSTRUCTION COMMENCES. DESIGNER ASSUMES NO LIABILITY FOR CONSTRUCTION:
- 1. BUILDER OR CONTRACTOR SHALL VERIFY ALL DIMENSIONS PRIOR TO PROCEEDING WITH CONSTRUCTION.
 - 2. BUILDER OR CONTRACTOR SHALL VERIFY COMPLIANCE WITH CITY AMENDMENTS TO IRC.
 - 3. DO NOT USE SCALED DIMENSIONS; USE ONLY DIMENSIONS AS CALLED OUT. WHEN NO DIMENSION IS PROVIDED, CONSULT WITH THE OWNER BEFORE PROCEEDING WITH WORK.
 - 4. CONTRACTOR SHALL VERIFY ALL EXISTING CONDITIONS, SITE UTILITY SERVICES AND DIMENSIONS AND NOTIFY ARCHITECT OF DISCREPANCIES THAT MAY AFFECT THE EXECUTION OF THE WORK BEFORE PROCEEDING.
 - 5. OMISSIONS OR CONFLICTS WITHIN THE DRAWINGS, NOTES OR DETAILS SHALL BE REPORTED THE OWNER BEFORE PROCEEDING WITH WORK.
 - 6. DETAILS TAKE PRECEDENCE DRAWING NOTES


REVISION SCHEDULE		
REV. #	NAME	DATE

PROPOSED ONE STORY
FARM HOUSE

264 CROCKETT RD WEATHERFORD TX
76088

GENERAL NOTES

DATE	01.31.2025
A002	
SCALE	AS INDICATED ON I1X17

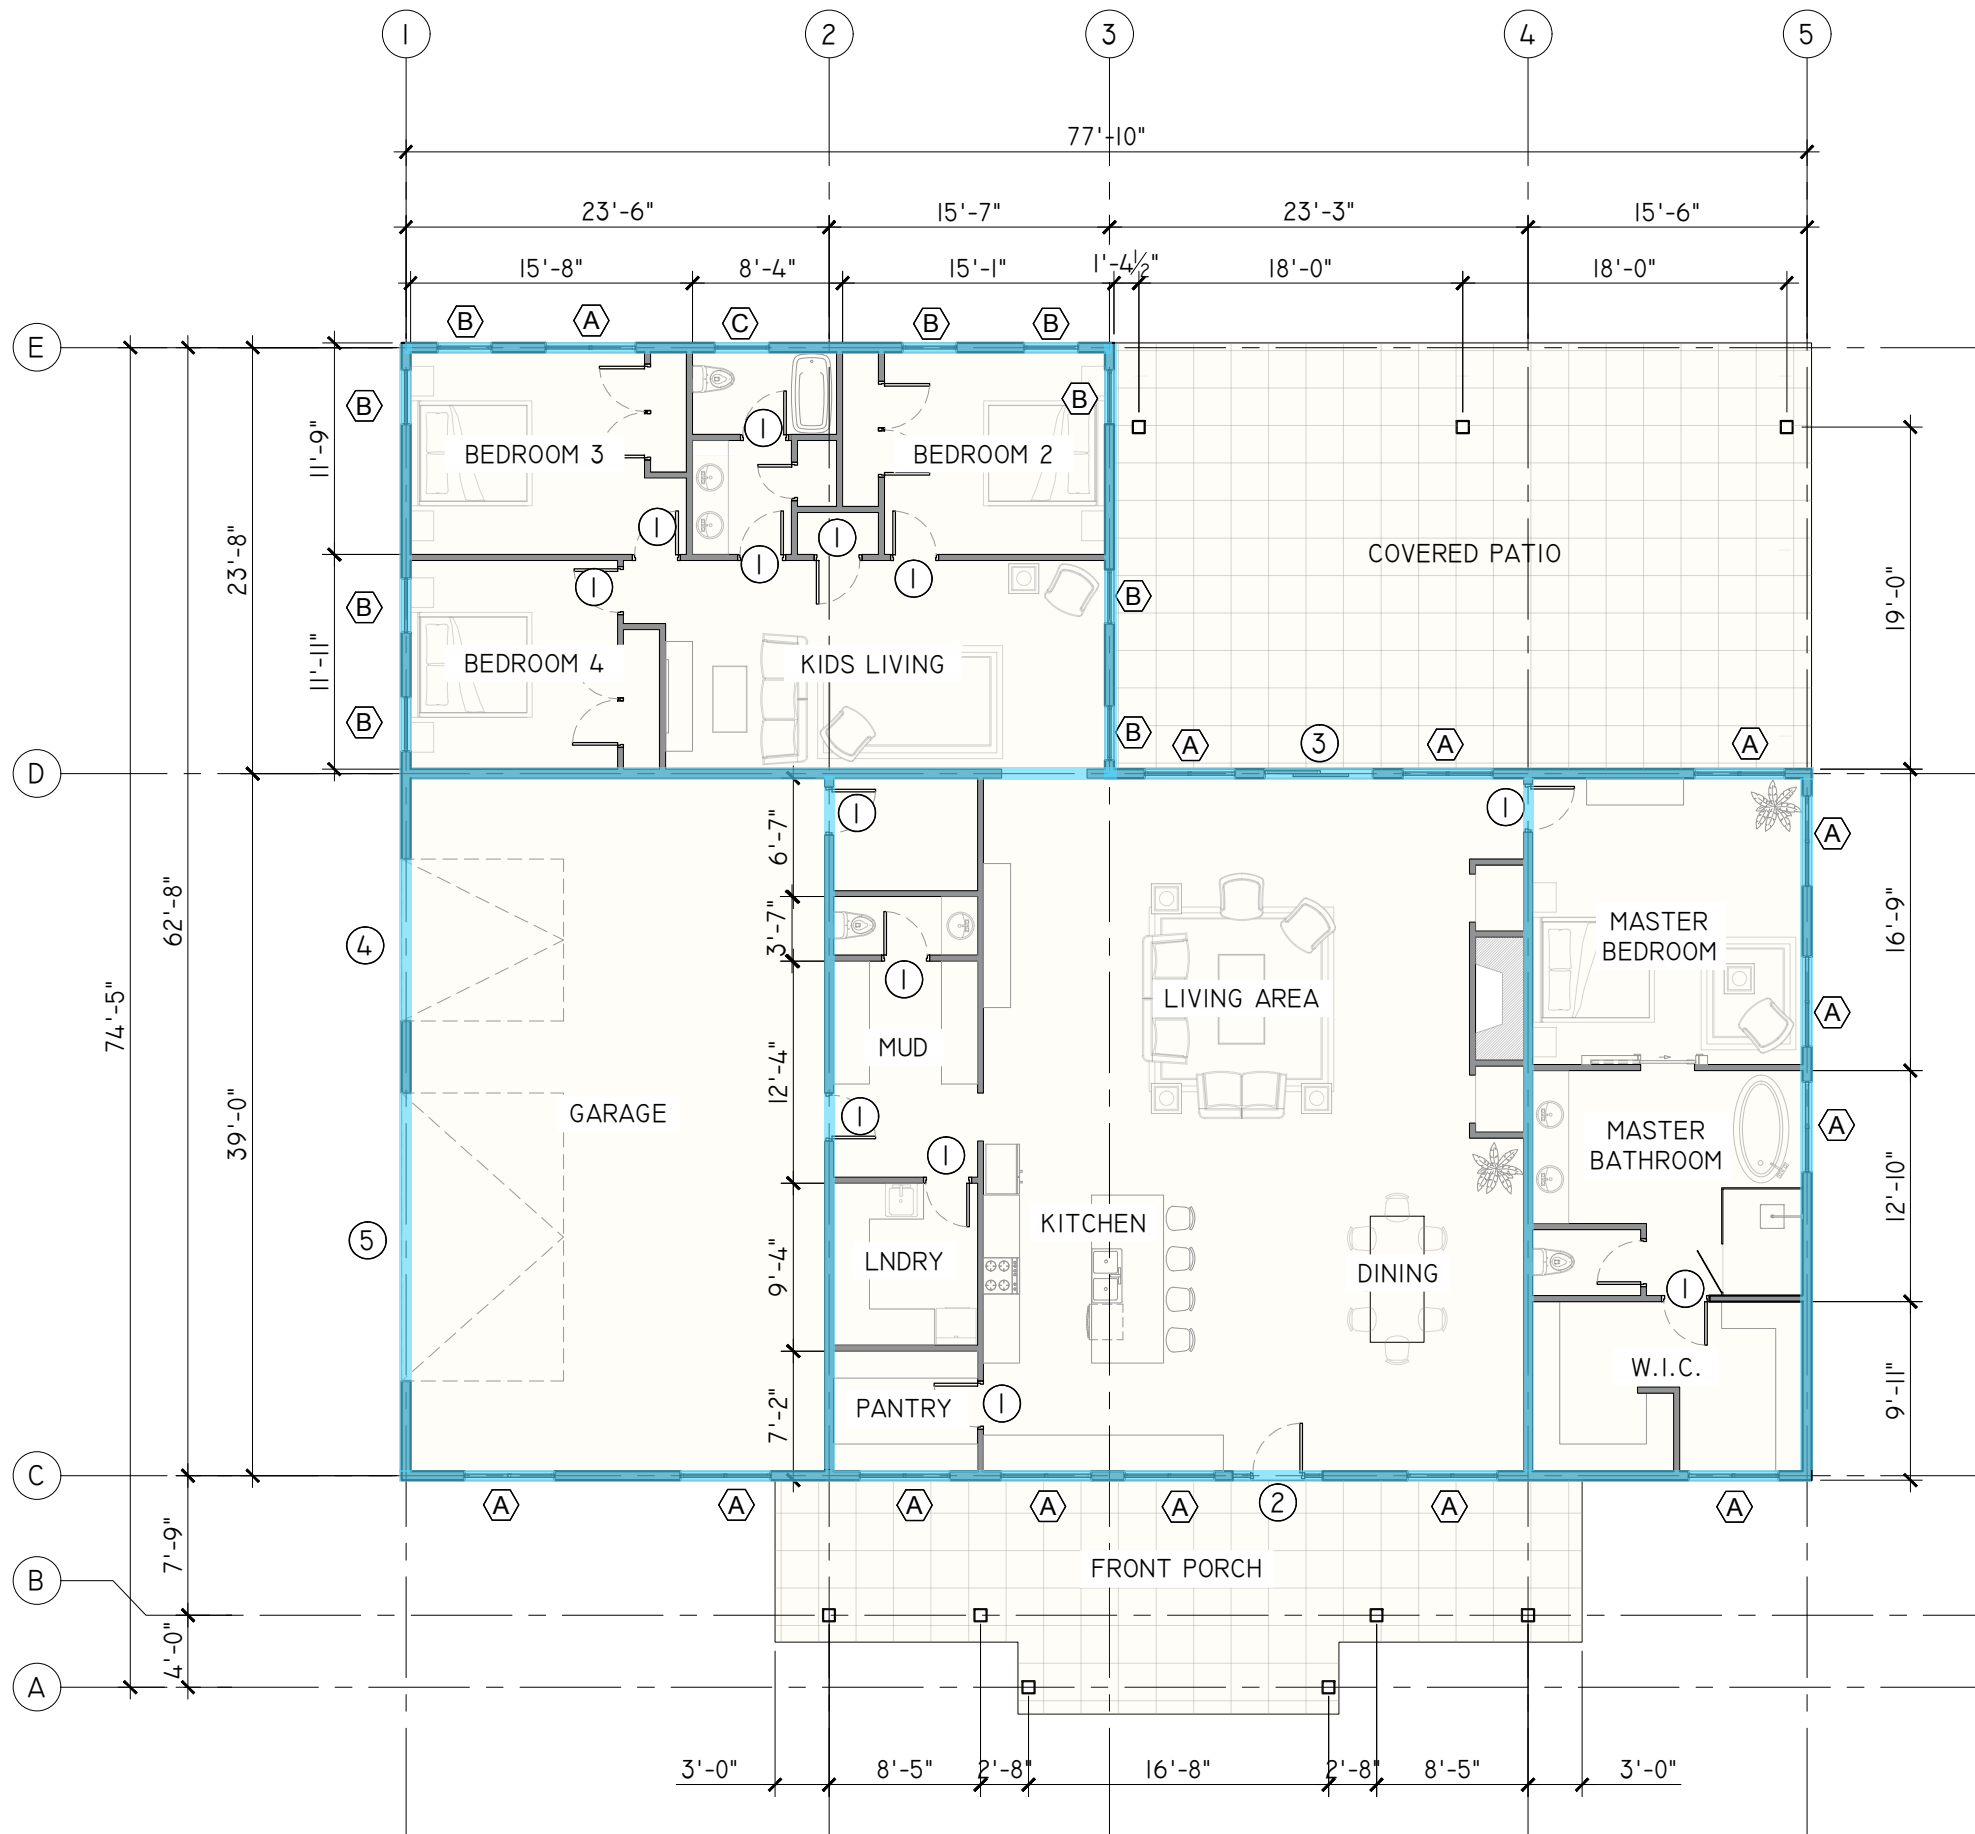

FLOOR PLAN

SCALE

3/32"=1'-0"

Bauen Consultants
ENGINEERING & ARCHITECTURE

CONTACT: 773-937-0712
ADDRESS: 128 DAV LN LONDON KY 40741

THIS DRAWING IS PROVIDED AS AN INSTRUMENT OF SERVICE BY THE ARCHITECT AND IS INTENDED FOR USE ON THIS PROJECT ONLY. THE DRAWING REMAINS THE PROPERTY OF THE ARCHITECT AND SHALL BE RETURNED TO HIM/HER UPON COMPLETION OF THE CONSTRUCTION WORK. PURSUANT TO THE ARCHITECTURAL WORKS COPYRIGHT PROTECTION ACT OF 1990, ALL DRAWINGS, SPECIFICATIONS, IDEAS, AND DESIGNS, INCLUDING THE OVERALL FORM, ARRANGEMENT, AND COMPOSITION OF THE SPACES, AND ELEMENTS APPEARING HEREIN, CONSTITUTES THE COPYRIGHT WORK OF THE ARCHITECT. ANY REPRODUCTION, USE, OR DISCLOSURE OF INFORMATION CONTAINED HEREIN WITHOUT PRIOR WRITTEN CONSENT OF THE ARCHITECT IS STRICTLY PROHIBITED.

GENERAL PLAN NOTES

- OWNER TO PERFORM THE FOLLOWING BEFORE CONSTRUCTION COMMENCES. DESIGNER ASSUMES NO LIABILITY FOR CONSTRUCTION:
- BUILDER OR CONTRACTOR SHALL VERIFY ALL DIMENSIONS PRIOR TO PROCEEDING WITH CONSTRUCTION.
 - BUILDER OR CONTRACTOR SHALL VERIFY COMPLIANCE WITH CITY AMENDMENTS TO IRC.
 - DO NOT USE SCALED DIMENSIONS; USE ONLY DIMENSIONS AS CALLED OUT. WHEN NO DIMENSION IS PROVIDED, CONSULT WITH THE OWNER BEFORE PROCEEDING WITH WORK.
 - CONTRACTOR SHALL VERIFY ALL EXISTING CONDITIONS, SITE UTILITY SERVICES AND DIMENSIONS AND NOTIFY ARCHITECT OF DISCREPANCIES THAT MAY AFFECT THE EXECUTION OF THE WORK BEFORE PROCEEDING.
 - OMISSIONS OR CONFLICTS WITHIN THE DRAWINGS, NOTES OR DETAILS SHALL BE REPORTED THE OWNER BEFORE PROCEEDING WITH WORK.
 - DETAILS TAKE PRECEDENCE DRAWING NOTES

REVISION SCHEDULE

REV. #	NAME	DATE

PROPOSED ONE STORY FARM HOUSE


264 CROCKETT RD WEATHERFORD TX 76088

FLOOR PLAN

DATE 01.31.2025

A100

SCALE AS INDICATED ON I1X17

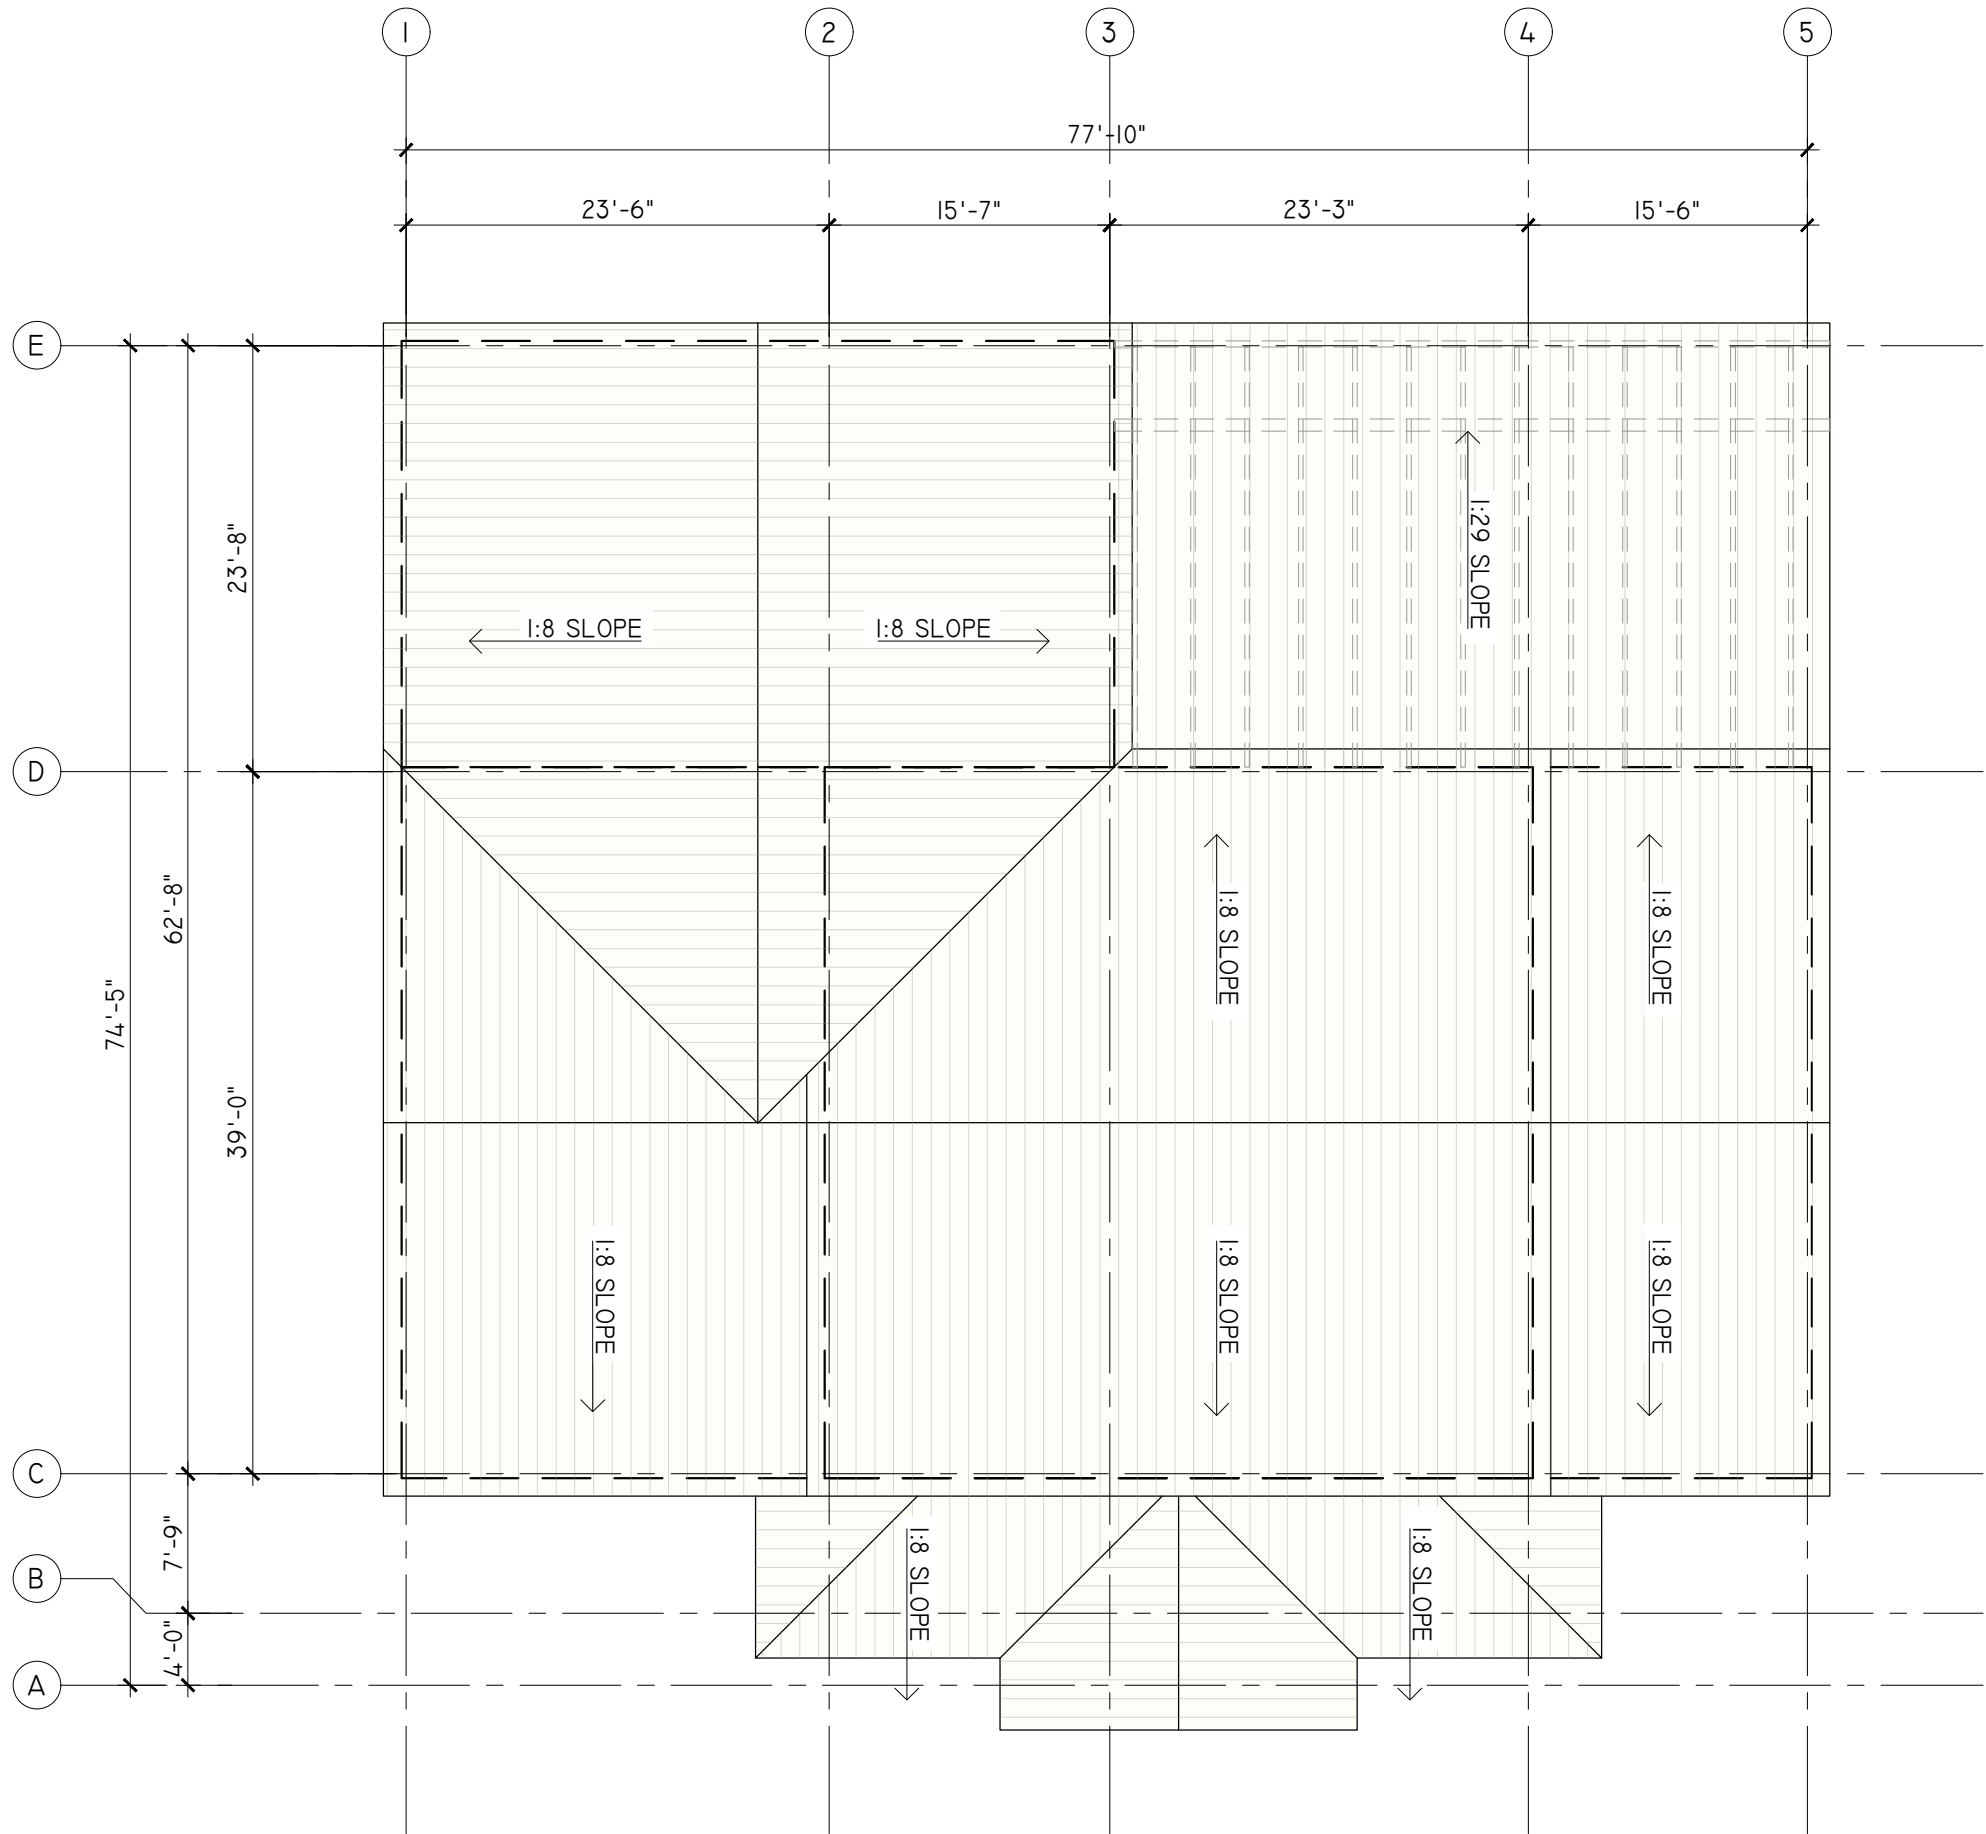

ROOF PLAN
SCALE 3/32"=1'-0"

Bauen Consultants
ENGINEERING & ARCHITECTURE
CONTACT: 773-937-0712
ADDRESS: 128 DAV LN LONDON KY 40741

THIS DRAWING IS PROVIDED AS AN INSTRUMENT OF SERVICE BY THE ARCHITECT AND IS INTENDED FOR USE ON THIS PROJECT ONLY. THE DRAWING REMAINS THE PROPERTY OF THE ARCHITECT AND SHALL BE RETURNED TO HIM/HER UPON COMPLETION OF THE CONSTRUCTION WORK. PURSUANT TO THE ARCHITECTURAL WORKS COPYRIGHT PROTECTION ACT OF 1990, ALL DRAWINGS, SPECIFICATIONS, IDEAS, AND DESIGNS, INCLUDING THE OVERALL FORM, ARRANGEMENT, AND COMPOSITION OF THE SPACES, AND ELEMENTS APPEARING HEREIN, CONSTITUTES THE COPYRIGHT WORK OF THE ARCHITECT. ANY REPRODUCTION, USE, OR DISCLOSURE OF INFORMATION CONTAINED HEREIN WITHOUT PRIOR WRITTEN CONSENT OF THE ARCHITECT IS STRICTLY PROHIBITED.

- GENERAL PLAN NOTES**
OWNER TO PERFORM THE FOLLOWING BEFORE CONSTRUCTION COMMENCES. DESIGNER ASSUMES NO LIABILITY FOR CONSTRUCTION:
1. BUILDER OR CONTRACTOR SHALL VERIFY ALL DIMENSIONS PRIOR TO PROCEEDING WITH CONSTRUCTION.
 2. BUILDER OR CONTRACTOR SHALL VERIFY COMPLIANCE WITH CITY AMENDMENTS TO IRC.
 3. DO NOT USE SCALED DIMENSIONS; USE ONLY DIMENSIONS AS CALLED OUT. WHEN NO DIMENSION IS PROVIDED, CONSULT WITH THE OWNER BEFORE PROCEEDING WITH WORK.
 4. CONTRACTOR SHALL VERIFY ALL EXISTING CONDITIONS, SITE UTILITY SERVICES AND DIMENSIONS AND NOTIFY ARCHITECT OF DISCREPANCIES THAT MAY AFFECT THE EXECUTION OF THE WORK BEFORE PROCEEDING.
 5. OMISSIONS OR CONFLICTS WITHIN THE DRAWINGS, NOTES OR DETAILS SHALL BE REPORTED THE OWNER BEFORE PROCEEDING WITH WORK.
 6. DETAILS TAKE PRECEDENCE DRAWING NOTES

REVISION SCHEDULE		
REV. #	NAME	DATE

PROPOSED ONE STORY
FARM HOUSE
264 CROCKETT RD WEATHERFORD TX
76088

ROOF PLAN	
DATE	01.31.2025
A101	
SCALE	AS INDICATED ON I1X17

THIS DRAWING IS PROVIDED AS AN INSTRUMENT OF SERVICE BY THE ARCHITECT AND IS INTENDED FOR USE ON THIS PROJECT ONLY. THE DRAWING REMAINS THE PROPERTY OF THE ARCHITECT AND SHALL BE RETURNED TO HIM/HER UPON COMPLETION OF THE CONSTRUCTION WORK. PURSUANT TO THE ARCHITECTURAL WORKS COPYRIGHT PROTECTION ACT OF 1990, ALL DRAWINGS, SPECIFICATIONS, IDEAS, AND DESIGNS, INCLUDING THE OVERALL FORM, ARRANGEMENT, AND COMPOSITION OF THE SPACES, AND ELEMENTS APPEARING HEREIN, CONSTITUTE THE COPYRIGHT WORK OF THE ARCHITECT. ANY REPRODUCTION, USE, OR DISCLOSURE OF INFORMATION CONTAINED HEREIN WITHOUT PRIOR WRITTEN CONSENT OF THE ARCHITECT IS STRICTLY PROHIBITED.

GENERAL PLAN NOTES

OWNER TO PERFORM THE FOLLOWING BEFORE CONSTRUCTION COMMENCES. DESIGNER ASSUMES NO LIABILITY FOR CONSTRUCTION:

- BUILDER OR CONTRACTOR SHALL VERIFY ALL DIMENSIONS PRIOR TO PROCEEDING WITH CONSTRUCTION.
- BUILDER OR CONTRACTOR SHALL VERIFY COMPLIANCE WITH CITY AMENDMENTS TO IRC.
- DO NOT USE SCALED DIMENSIONS; USE ONLY DIMENSIONS AS CALLED OUT. WHEN NO DIMENSION IS PROVIDED, CONSULT WITH THE OWNER BEFORE PROCEEDING WITH WORK.
- CONTRACTOR SHALL VERIFY ALL EXISTING CONDITIONS, SITE UTILITY SERVICES AND DIMENSIONS AND NOTIFY ARCHITECT OF DISCREPANCIES THAT MAY AFFECT THE EXECUTION OF THE WORK BEFORE PROCEEDING.
- OMISSIONS OR CONFLICTS WITHIN THE DRAWINGS, NOTES OR DETAILS SHALL BE REPORTED TO THE OWNER BEFORE PROCEEDING WITH WORK.
- DETAILS TAKE PRECEDENCE DRAWING NOTES

REVISION SCHEDULE

REV. #	NAME	DATE

PROPOSED ONE STORY FARM HOUSE


264 CROCKETT RD WEATHERFORD TX 76088

ELEVATION

DATE 01.31.2025

A200

SCALE AS INDICATED ON IIX17

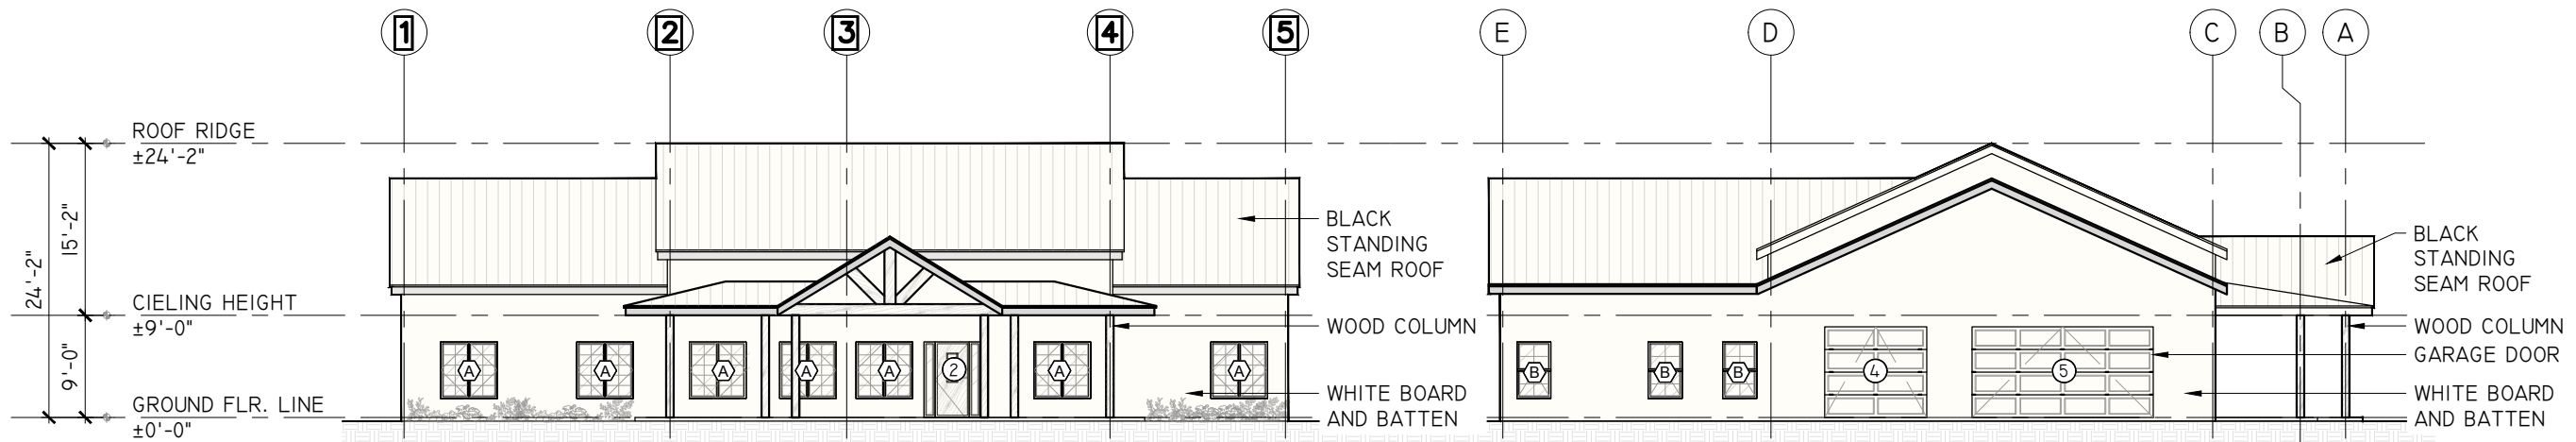


FRONT ELEVATION

SCALE 1/16"=1'-0"

LEFT ELEVATION

SCALE 1/16"=1'-0"

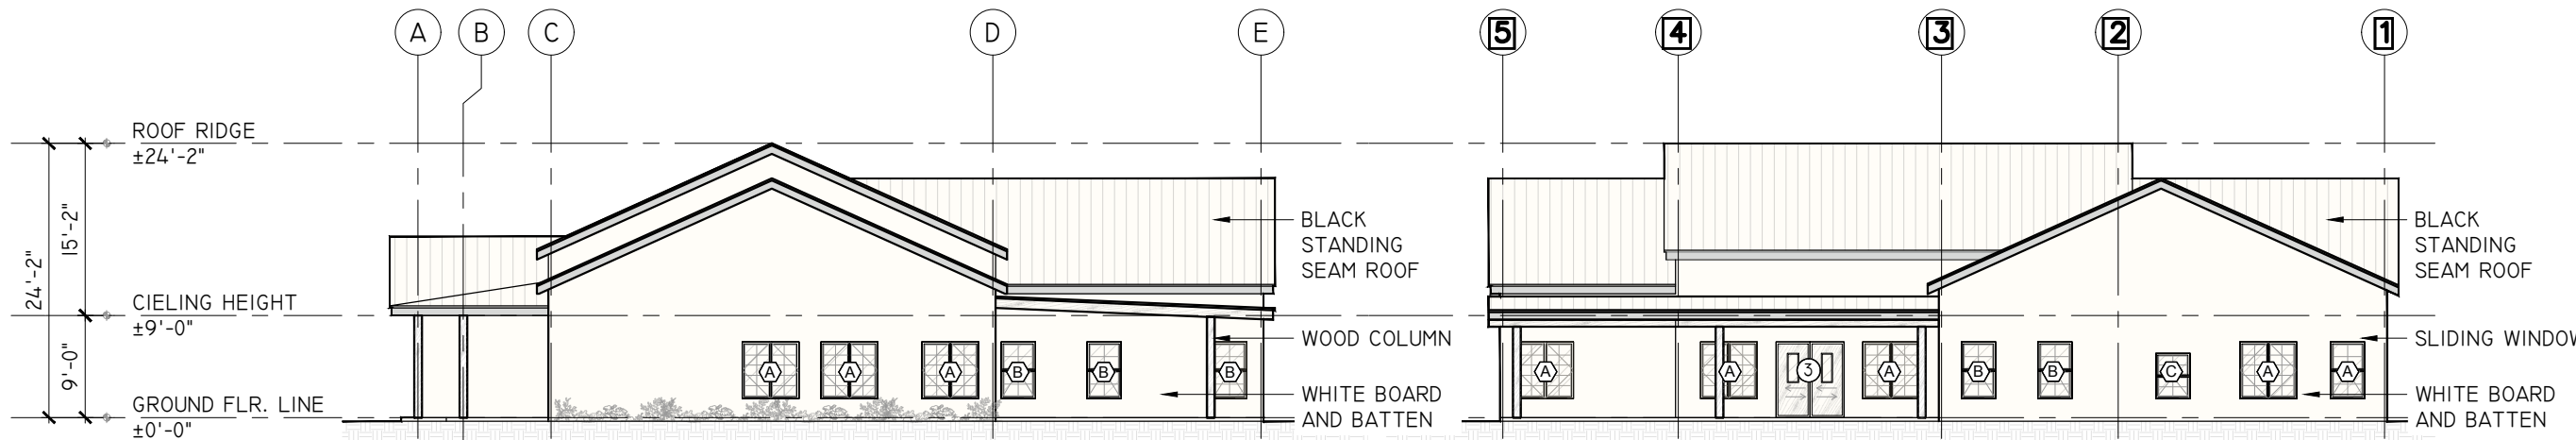


RIGHT ELEVATION

SCALE 1/16"=1'-0"


REAR ELEVATION

SCALE 1/16"=1'-0"

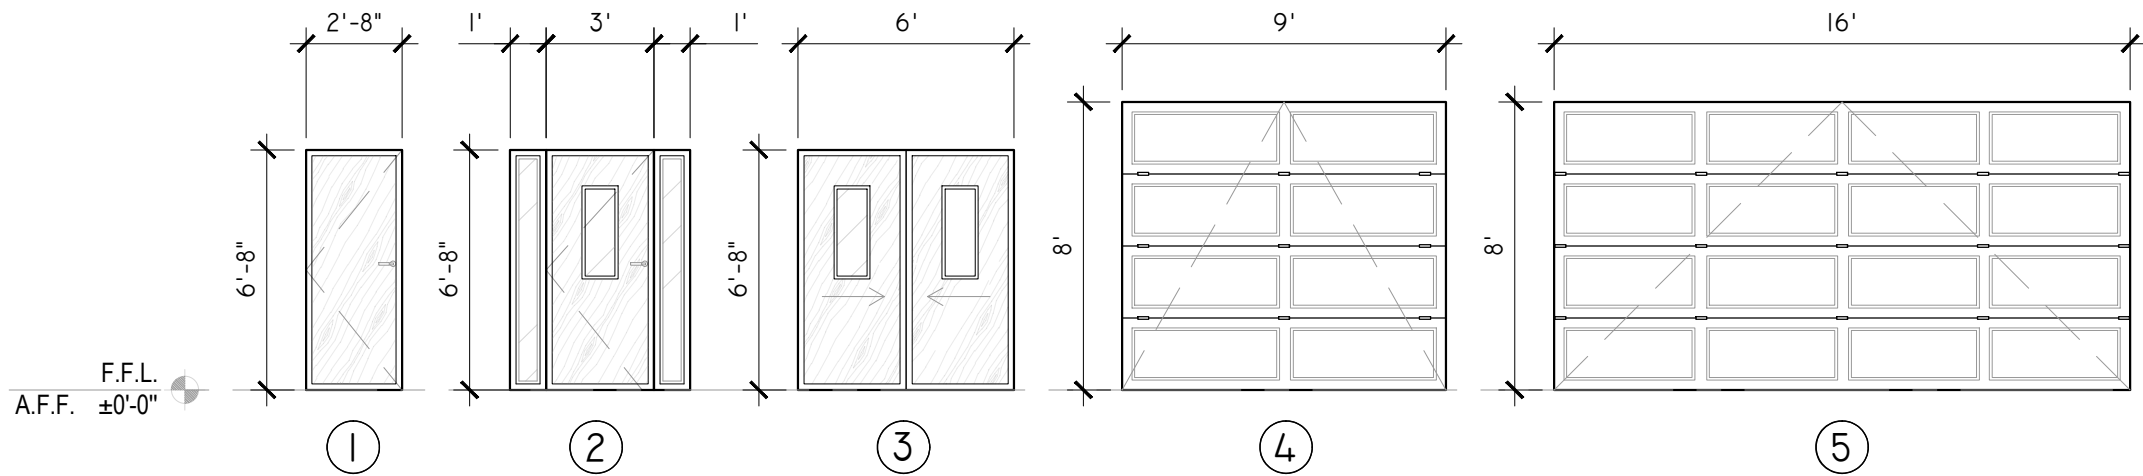

DOOR TYPES

SCALE 3/16"=1'-0"

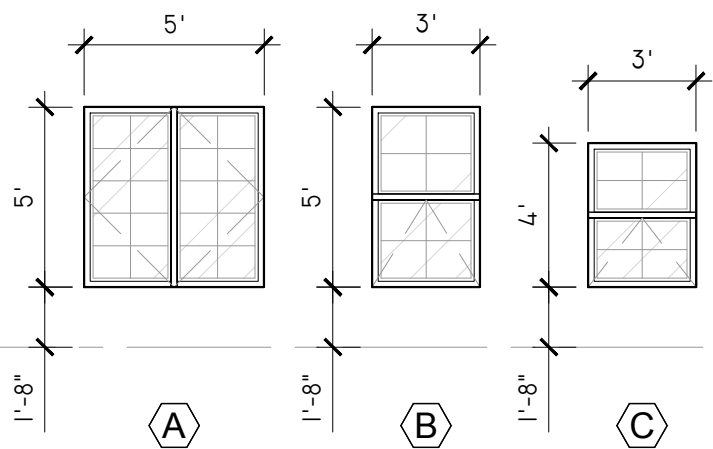

WINDOW TYPES

SCALE 3/16"=1'-0"

Bauen Consultants
ENGINEERING & ARCHITECTURE

CONTACT: 773-937-0712
ADDRESS: 128 DAV LN LONDON KY 40741

THIS DRAWING IS PROVIDED AS AN INSTRUMENT OF SERVICE BY THE ARCHITECT AND IS INTENDED FOR USE ON THIS PROJECT ONLY. THE DRAWING REMAINS THE PROPERTY OF THE ARCHITECT AND SHALL BE RETURNED TO HIM/HER UPON COMPLETION OF THE CONSTRUCTION WORK. PURSUANT TO THE ARCHITECTURAL WORKS COPYRIGHT PROTECTION ACT OF 1990, ALL DRAWINGS, SPECIFICATIONS, IDEAS, AND DESIGNS, INCLUDING THE OVERALL FORM, ARRANGEMENT, AND COMPOSITION OF THE SPACES, AND ELEMENTS APPEARING HEREIN, CONSTITUTES THE COPYRIGHT WORK OF THE ARCHITECT. ANY REPRODUCTION, USE, OR DISCLOSURE OF INFORMATION CONTAINED HEREIN WITHOUT PRIOR WRITTEN CONSENT OF THE ARCHITECT IS STRICTLY PROHIBITED.

GENERAL PLAN NOTES

OWNER TO PERFORM THE FOLLOWING BEFORE CONSTRUCTION COMMENCES. DESIGNER ASSUMES NO LIABILITY FOR CONSTRUCTION:

1. BUILDER OR CONTRACTOR SHALL VERIFY ALL DIMENSIONS PRIOR TO PROCEEDING WITH CONSTRUCTION.
2. BUILDER OR CONTRACTOR SHALL VERIFY COMPLIANCE WITH CITY AMENDMENTS TO IRC.
3. DO NOT USE SCALED DIMENSIONS; USE ONLY DIMENSIONS AS CALLED OUT. WHEN NO DIMENSION IS PROVIDED, CONSULT WITH THE OWNER BEFORE PROCEEDING WITH WORK.
4. CONTRACTOR SHALL VERIFY ALL EXISTING CONDITIONS, SITE UTILITY SERVICES AND DIMENSIONS AND NOTIFY ARCHITECT OF DISCREPANCIES THAT MAY AFFECT THE EXECUTION OF THE WORK BEFORE PROCEEDING.
5. OMISSIONS OR CONFLICTS WITHIN THE DRAWINGS, NOTES OR DETAILS SHALL BE REPORTED THE OWNER BEFORE PROCEEDING WITH WORK.
6. DETAILS TAKE PRECEDENCE DRAWING NOTES

REVISION SCHEDULE

REV. #	NAME	DATE

PROPOSED ONE STORY FARM HOUSE

264 CROCKETT RD WEATHERFORD TX 76088

DOOR AND WINDOWS TYPE

DATE 01.31.2025

A300

SCALE AS INDICATED ON IIXI7

DOOR AND FRAME SCHEDULE												
DOOR/FRAME	TYPE	DOOR					FRAME			QUANTITY	RATING	BRAND
NO.		WIDTH	HEIGHT	MAT'L	FINISH	GLASS	TYPE	MAT'L	FINISH			
D1	SWING DOOR	2'-8"	6'-8"	WOOD	PRE-FIN			WOOD	PRE-FIN	13		
D2	SWING DOOR	5'-0"	6'-8"	GLASS	PRE-FIN			WOOD	PRE-FIN	1		
D3	SLIDING DOOR	6'-0"	6'-8"	WOOD	PRE-FIN			WOOD	PRE-FIN	1		
D4	GARAGE DOOR	9'-0"	8'-0"	ALUM	PRE-FIN			ALUM	PRE-FIN	1		
D5	GARAGE DOOR	16'-4"	8'-0"	ALUM	PRE-FIN			ALUM	PRE-FIN	1		

WINDOW SCHEDULE							
WINDOW	NO.	WINDOW					
NO.	LEAVES	WIDTH	HEIGHT	TYPE	FRAME	GLASS	QTY.
A	2	5'-0"	5'-0"	SWING	VINYL	TEMPERED	14
B	2	3'-0"	5'-0"	AWNING	VINYL	TEMPERED	9
C	2	3'-0"	4'-0"	AWNING	VINYL	TEMPERED	1
NOTES: ALL WIDTH AND HEIGHT MEASUREMENTS IN THE WINDOW SCHEDULE ARE ROUGH OPENINGS MEASURES.							

Bauen Consultants
ENGINEERING & ARCHITECTURE

CONTACT: 773-937-0712
ADDRESS:128 DAV LN LONDON KY 40741

THIS DRAWING IS PROVIDED AS AN INSTRUMENT OF SERVICE BY THE ARCHITECT AND IS INTENDED FOR USE ON THIS PROJECT ONLY. THE DRAWING REMAINS THE PROPERTY OF THE ARCHITECT AND SHALL BE RETURNED TO HIM/HER UPON COMPLETION OF THE CONSTRUCTION WORK. PURSUANT TO THE ARCHITECTURAL WORKS COPYRIGHT PROTECTION ACT OF 1990, ALL DRAWINGS, SPECIFICATIONS, IDEAS, AND DESIGNS, INCLUDING THE OVERALL FORM, ARRANGEMENT, AND COMPOSITION OF THE SPACES, AND ELEMENTS APPEARING HEREIN, CONSTITUTES THE COPYRIGHT WORK OF THE ARCHITECT. ANY REPRODUCTION, USE, OR DISCLOSURE OF INFORMATION CONTAINED HEREIN WITHOUT PRIOR WRITTEN CONSENT OF THE ARCHITECT IS STRICTLY PROHIBITED.

GENERAL PLAN NOTES

OWNER TO PERFORM THE FOLLOWING BEFORE CONSTRUCTION COMMENCES. DESIGNER ASSUMES NO LIABILITY FOR CONSTRUCTION:

- BUILDER OR CONTRACTOR SHALL VERIFY ALL DIMENSIONS PRIOR TO PROCEEDING WITH CONSTRUCTION.
- BUILDER OR CONTRACTOR SHALL VERIFY COMPLIANCE WITH CITY AMENDMENTS TO IRC.
- DO NOT USE SCALED DIMENSIONS; USE ONLY DIMENSIONS AS CALLED OUT. WHEN NO DIMENSION IS PROVIDED, CONSULT WITH THE OWNER BEFORE PROCEEDING WITH WORK.
- CONTRACTOR SHALL VERIFY ALL EXISTING CONDITIONS, SITE UTILITY SERVICES AND DIMENSIONS AND NOTIFY ARCHITECT OF DISCREPANCIES THAT MAY AFFECT THE EXECUTION OF THE WORK BEFORE PROCEEDING.
- OMISSIONS OR CONFLICTS WITHIN THE DRAWINGS, NOTES OR DETAILS SHALL BE REPORTED THE OWNER BEFORE PROCEEDING WITH WORK.
- DETAILS TAKE PRECEDENCE DRAWING NOTES

REVISION SCHEDULE		
REV. #	NAME	DATE

PROPOSED ONE STORY FARM HOUSE	
264 CROCKETT RD WEATHERFORD TX 76088	
DOORS AND WINDOWS SCHEDULE	
DATE	01.31.2025
A301	
SCALE	AS INDICATED ON I1X17

ELECTRICAL GENERAL NOTES

- 1- ALL CONDUCTORS SHALL BE COPPER RATED 75C WET/DRY EXCEPT WHERE OTHERWISE REQUIRED BY U.L. OR CODES, U.O.N. MINIMUM WIRE SIZE SHALL BE #14 AWG. EXCLUDING CONTROL WIRING.
- 2- ALL CONDUIT RISERS SHALL BE RIGID GALVANIZED STEEL (RGS) WHERE CONDUIT BENDS UPWARD FROM UNDERGROUND TO ABOVE GROUND, USE AND APPROVED PVC TO RGS COUPLER, AS REQUIRED. RGS CONDUITS SHALL EXTEND A MINIMUM OF 18" BELOW GRADE.
- 3- ALL EQUIPMENT, WIRING DEVICES, ETC. SHALL BE NEW.
- 4- ENTIRE INSTALLATION SHALL BE IN ACCORDANCE WITH THE NATIONAL ELECTRICAL CODE, 2002 EDITION (NEC), FBC 2004 AND THE APPLICABLE EDITIONS OF ALL LOCAL CODES, RULES AND ORDINANCES HAVING JURISDICTION.
- 5- ALL CONDUITS RUNS ARE SHOWN DIAGRAMMATICALLY, EXACT ROUTING SHALL BE DETERMINED IN THE FIELD, UNLESS OTHERWISE NOTED.
- 6- ALL DISCONNECT SWITCHES SHALL BE SIZED BY NEC TO ACCOMMODATE EQUIPMENT SERVED INCLUDING REQUIRED FUSES, UON. SWITCHES SHALL BE HORSE POWER RATED AND SIZED AS PER MOTOR NAMEPLATE CURRENT. HEAVY DUTY TYPE.
- 7- ALL ELECTRICAL EQUIPMENTS SHALL BE RAINLIGHT (NEMA 3R) WHERE EXPOSED TO THE WEATHER. ALL FLEX. CONDUITS CONNECTED TO SUCH EQUIPMENT SHALL BE LIQUID TIGHT. USE NEMA 4X (STAINLESS STEEL) AT CORROSIVE LOCATIONS (POOL EQUIPMENT ROOM).
- 8- WIRE WAYS SHALL BE SIZED AS REQUIRED, PER NEC. UNLESS OTHERWISE NOTED.
- 9- COORDINATE ALL ELECTRICAL SITE WORK WITH GENERAL CONTRACTOR.
- 10- FOR UNDERGROUND ELECTRICAL CONDUITS, PROVIDE PULL BOXES SUCH THAT NO SINGLE CONDUIT RUN HAS BEND IN EXCESS OF THREE 90 BENDS. PULL BOXES SHALL BE SUITABLE AND APPROVED FOR THE INTENDED USE. WARNING TAPE WHICH SAYS "WARNING BURIED ELECTRIC" SHALL BE PLACED IN TRENCHES ABOVE ALL UNDERGROUND ELECTRIC CONDUITS. WHERE CONDUITS PASS UNDERNEATH PAVED AREAS, THEY SHALL BE RGS. WHERE UNDERGROUND CONDUITS ARE NOT EXPOSED TO MECHANICAL DAMAGE OR ARE NOT UNDER PAVED AREAS, THEY SHALL BE SCHEDULE 40 PVC. ALL CONDUITS RISERS SHALL BE RGS.
- 11- FOR SIGNAL SYSTEMS:

A- PROVIDE BOXES AND GROUNDING FOR ALL SIGNAL OUTLETS AND EQUIPMENT.

B- COORDINATE INSTALLATION OF ALL SIGNAL OUTLETS, RACEWAYS, ENCLOSURES AND BACKBOARDS.

C- SIGNAL CONDUITS SHALL NOT BE INSTALLED IN THE SAME TRENCH WITH POWER AND LIGHTING CONDUITS.

D- MARK TERMINATIONS OF SIGNAL CONDUITS AS DIRECTED BY TELEPHONE COMPANY.
- 12- ALL CIRCUIT BREAKERS SHALL BE INVERSE TIME TYPE (THERMAL MAGNETIC). TWO AND THREE POLE CIRCUIT BREAKERS SHALL BE COMMON TRIP. NO TIE HANDLES PERMITTED.
- 13- ALL ELECTRICAL EQUIPMENT, DEVICES WIRE, ETC., SHALL BE LISTED FOR THE INTENDED USE, WITH UNDERWRITER'S LABORATORIES, INC. (UL) WHERE STANDARDS HAVE BEEN ESTABLISHED BY UL.
- 14- ALL CONDUCTORS SHALL BE IN CONDUITS, ALL CONDUITS SHALL BE INTERMEDIATED (MC), OR RIGID GALVANIZED STEEL (RGS) EXCEPT THAT: (A) POLY VINYL CHLORIDE (PVC) CONDUITS MAY BE USED INSIDE CONCRETE SLABS AND UNDERGROUND PROVIDED ELBOWS AND RISERS ARE RGS; (B) ELECTRICAL METALLIC TUBING (EMT) MAY BE USED IN OR ON WALLS OR CEILINGS WHERE NOT SUBJECT TO MECHANICAL DAMAGE, DAMP CONDITIONS OR CORROSIVE CONDITIONS; (C) LIQUID TIGHT FLEXIBLE CONDUIT WHERE REQUIRED; (D) FLEXIBLE METALLIC CONDUIT WHERE REQUIRED IN DRY LOCATIONS. ALL CONDUITS IN HAZARDOUS AREAS SHALL MEET THE REQUIREMENTS OF NEC CHAPTER 5.
- 15- PROVIDE LAMPS WITH ALL FIXTURES, VERIFY LAMP TYPE WITH MANUFACTURER.
- 16- CONTRACTOR SHALL COORDINATE ELECTRIC SERVICE WITH POWER COMPANY.
- 17- ELECTRICAL CONTRACTOR SHALL NOT SCALE DRAWINGS. CONTRACTOR SHALL REFER TO ARCHITECTURAL PLANS AND ELEVATIONS FOR EXACT LOCATIONS OF ALL EQUIPMENT UNLESS NOTED OTHERWISE.
- 18- ELECTRICAL CONTRACTOR SHALL VISIT THE JOB SITE AND VERIFY ALL CONDITIONS, LOCATIONS, DIMENSIONS AND COUNTS AS SHOWN AND/OR NOTED ON THE DRAWINGS. THIS SHALL INCLUDE ANY AND ALL FABRICATIONS PRIOR TO INSTALLATION.
- 19- IT SHALL BE THE RESPONSIBILITY OF THE ELECTRICAL CONTRACTOR FOR THE ADVANCED ORDERING OF LONG LEAD ITEMS, AS NOT TO INTERFERE WITH THE PRODUCTION OF OTHER TRADES RESULTING IN ANY DOWN OR LAG TIME.
- 20- IT SHALL BE THE RESPONSIBILITY OF THE ELECTRICAL CONTRACTOR TO PROVIDE ALL LABOR, MATERIALS AND SUPERVISION NECESSARY TO ACCOMPLISH THE WORK AS SHOWN AND/OR NOTED ON THE DRAWINGS.
- 21- IT SHALL BE UNDERSTOOD THAT ALL WORK PERFORMED SHALL BE DONE BY A LICENSED ELECTRICAL CONTRACTOR AND IN A FIRST-CLASS WORKMANLIKE MANNER, SAID CONTRACTOR SHALL MEET ALL REQUIREMENTS SET FORTH BY ANY LOCAL ORDINANCE AND GOVERNING AUTHORITIES.

- 22- THE ELECTRICAL CONTRACTOR SHALL BE RESPONSIBLE TO REPAIR TO ORIGINAL CONDITIONS ANY AND ALL DAMAGED TO BUILDING SURFACES, EQUIPMENT AND FURNISHING CAUSED DURING PERFORMANCE OF WORK.
- 23- THE ELECTRICAL CONTRACTOR SHALL KEEP ALL AREAS IN WHICH WORK IS BEING PERFORMED, FREE FROM DEBRIS AT ALL TIMES AND SAID AREAS SHALL BE LEFT BROOM CLEAN AT THE END OF EACH WORKING DAY.
- 24- IT SHALL NOT BE THE INTENT OF THESE PLANS AND/OR SPECIFICATION TO SHOW EVERY MINOR DETAIL OF CONSTRUCTION THE ELECTRICAL CONTRACTOR SHALL BE EXPECTED TO FURNISH AND INSTALL ALL ITEMS FOR A COMPLETE ELECTRICAL SYSTEM AND PROVIDE ALL REQUIREMENTS NECESSARY FOR EQUIPMENT TO BE PLACED IN PROPER WORKING ORDER AND IN ACCORDANCE TO APPLICABLE CODES.
- 25- WHERE CORE DRILLING OF FLOOR/WALLS IS REQUIRED, CONTRACTOR SHALL SEAL OPENING WATERTIGHT AFTER UTILITIES HAVE BEEN INSTALLED. LOCATION OF CORED HOLES SHALL COORDINATE WITH LOCATION OF EQUIPMENT IN A MANNER TO BE CLEAN AND FUNCTIONAL. THE CONTRACTOR SHALL INSTALL ONLY ONE CONDUIT PER HOLE AND SEAL THE OPENING AROUND THE CONDUIT AS SPECIFIED.
- 26- ELECTRICAL CONTRACTOR SHALL VERIFY AND COORDINATE THE CIRCUIT PROTECTIVE DEVICE RATING FOR EQUIPMENT PRIOR TO ORDERING AND CONSTRUCTION.
- 27- ALL FUSES SHALL BE CURRENT LIMITING, PER U.L. RATED 600V. UON.

A- NONTIME DELAY FUSES IN MAIN SWITCHES AND SWITCHES FEEDING PANELS.

B- TIME DELAY FUSES FOR MOTOR AND A/C CIRCUITS.
- 28- OUTLET BOXES SHALL BE PRESSED STEEL IN DRY LOCATIONS, CAST ALLOY WITH THREADED HUBS IN WET OR DAMP LOCATIONS AND SPECIAL ENCLOSURE FOR OTHER CLASSIFIED AREAS.
- 29- MOTOR STARTERS SHALL BE MANUAL OR MAGNETIC, AS INDICATED OR REQUIRED, WITH OVERLOAD RELAYS OR FUSES IN EACH HOT LEG. SEE MECHANICAL PLANS (MECHANICAL EQUIPMENT SCHEDULE) FOR ADDITIONAL REQUIREMENTS.
- 30- FURNISH AND INSTALL DISCONNECT SWITCHES AND WIRING FOR AIR CONDITIONING SYSTEM AS PER MANUFACTURER RECOMMENDATIONS. CONTROLS ARE TO BE SUPPLIED BY AIR CONDITIONING CONTRACTOR AND CONNECTED BY ELECTRICAL CONTRACTOR.
- 31- CONTRACTOR SHALL GUARANTEE ALL MATERIALS AND WORKMANSHIP ARE FREE FROM DEFECTS FOR A PERIOD OF NOT LESS THAN ONE YEAR FROM DATE OF ACCEPTANCE, UNLESS INDICATED OR SPECIFIED OTHERWISE.
- 32- CORRECTION OF ANY DEFECTS ON NEW EQUIPMENT SHALL BE COMPLETE WITHOUT ADDITIONAL CHARGE AND SHALL INCLUDE REPLACEMENT OF REPAIR OF ANY OTHER PHASE OF THE INSTALLATION WHICH MAY HAVE BEEN DAMAGED THEREBY.
- 33- ALL REQUIRED INSURANCE SHALL BE PROVIDED FOR PROTECTION AGAINST PUBLIC LIABILITY AND PROPERTY DAMAGE FOR THE DURATION OF THIS WORK.
- 34- AS A MINIMUM, ALL EQUIPMENT SHALL MEET APPLICABLE STANDARDS, FOR THE TYPE OF EQUIPMENT AND INTENDED USE, OF THE FOLLOWING:


A. AMERICAN NATIONAL STANDARDS INSTITUTE (ANSI)

B. ILLUMINATING ENGINEERS SOCIETY (IES)

C. AMERICAN SOCIETY FOR TESTING AND MATERIALS (ASTM)

D. NATIONAL ELECTRICAL MANUFACTURER'S ASSOCIATES. (NEMA)

NOTE: THESE STANDARDS ARE SUBORDINATE TO CODES AND STANDARDS SET BY U.L.
- 35- CONTRACTOR SHALL SUBMIT SHOP DRAWINGS FOR NORMAL AND EMERGENCY SWITCHGEAR TOGETHER WITH OVERCURRENT DEVICES SELECTIVITY AND COORDINATION STUDY FROM MANUFACTURER IN COMPLIANCE WITH N.E.C. ART. 700.27
- 36- ALL BALLASTS SHALL HAVE MINIMUM. POWER FACTOR OF 0.90 ALL BALLAST FOR HID FIXTURES SHALL BE CONSTANT WATTAGE TYPE WITH +/-5% LAMP WATTS FOR +/-10% NOMINAL UNE VOLTAGE VARIATION.
- 37- ELECTRICAL CONTRACTOR SHALL SUBMIT (6 COPIES) OF THE EQUIPMENT LAYOUT FOR ALL ELECTRICAL SPACES, ROOMS, ETC. LAYOUT SHALL CONSIST OF PAN VIEWS (SCALED AT 1/2"=1'-0") AND ELEVATIONS (DIMENSIONED) FOR EACH SUCH SPACE, ROOM, ETC.
- 38- ALL CONNECTIONS TO GROUND RODS SHALL BE MADE WITH UL APPROVED WELDED CONNECTIONS, UNLESS NOTED OTHERWISE.
- 39- PROPER PLASTER RINGS SHALL BE USED WITH OUTLET BOXES, PLASTER RING SHALL BE A MAXIMUM OF 1/8" FROM THE FINISHED SURFACE OF THE DRYWALL AFTER DRYWALL IS INSTALLED. PROPER COORDINATION BETWEEN ELECTRICAL SUBCONTRACTOR AND GENERAL CONTRACTOR FOR PLASTER RING INSTALLATION WILL BE REQUIRED. NO "GOOF" RINGS WILL BE ALLOWED. ALL OUTLET BOXES SHALL BE SECURELY FASTENED. ANY AND ALL IMPROPERLY INSTALLED PLASTER RINGS OR OUTLET BOXES SHALL BE REMOVED AND A NEW RING OR OUTLET INSTALLED AT CONTRACTOR'S EXPENSE. NO GANGABLE BOXES WILL BE ACCEPTED.
- 40- ALL OPENINGS FOR LIGHT FIXTURES IN CEILING SHALL BE PROTECTED IN A MANNER (PER ALL GOVERNING CODES) THAT WILL PROVIDE THE SAME RATING AS THE CEILING (THIS APPLIES TO ALL FIRE RATED CEILINGS).
- 41- PROVIDE FIRE RETARDANT U.L. APPROVED SEALANT ON ALL PENETRATIONS OF FIRE RATED PARTITIONS, WALL AND STRUCTURAL SLABS. IT SHALL BE THE RESPONSIBILITY OF THE ELECTRICAL CONTRACTOR TO VERIFY, PRIOR TO SUBMITTING BID, LOCATION OF ALL SUCH FIRE RATED PARTITIONS, WALL AND STRUCTURAL SLABS.
- 42- USE 3/4" FIRE RESISTANT PLYWOOD BACKBOARDS FOR TELEPHONE TERMINAL BOARDS AND FOR SURFACE MOUNTING GROUPED ELECTRICAL EQUIPMENT, PAINTED ON BOTH SIDES AND EDGES WITH TWO COATS OF FLAT BLACK ASPHALT PAINT.
- 43- CONTRACTOR TO VERIFY VOLTAGES OF ALL LIGHT FIXTURES PRIOR TO BIDDING RELATIVE TO THEIR SPECIFIC APPLICATION OF FLOOR PLANS. CONTRACTOR TO COORDINATE FIXTURES WITH ARCHITECTURAL DRAWINGS AND VERIFY APPROPRIATE CLEARANCES AND APPLICATION WITH ALL ARCHITECTURAL FINISHES PRIOR TO BIDDING.

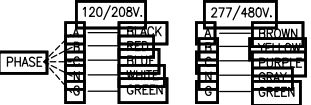- 44- A SEPARATE, DEDICATED AND SEPARATELY GROUNDING CIRCUIT WITH AND ISOLATED GROUNDING RECEPTACLE SHALL BE PROVIDED FOR ALL COMPUTER EQUIPMENT.
- 45- CONTRACTOR TO VERIFY AVAILABLE SERVICE VOLTAGE AND PHASES WITH F.P.&L. PRIOR TO BID. AND PROVIDE BID ALLOWANCE FOR ALTERNATES.
- 46- METER CANS, HUBS, & LUGS FOR SAME ARE TO BE FURNISHED AND INSTALLED BY ELECTRICAL CONTRACTOR. ELECTRICAL CONTRACTOR TO VERIFY SPECIFIC TYPE OF METER CAN TO BE USED WITH F.P.L. PRIOR TO BID.
- 47- PROVIDE A 4" STEEL REINFORCED CONCRETE HOUSEKEEPING PAD UNDER ALL FLOOR MOUNTED SWITCHGEAR.
- 48- CONTRACTOR SHALL PROVIDE A TYPE WRITTEN DIRECTORY OF EACH PANEL SCHEDULE, INSIDE EACH PANEL BOARD. HAND WRITTEN DIRECTORY IS NOT ACCEPTABLE.
- 49- ALL CIRCUITS INDICATED ON PANEL SCHEDULES AS 1 POLE CIRCUIT BREAKERS SHALL BE PROVIDED WITH A HOT, NEUTRAL CONDUCTORS AND EQUIPMENT GROUND WIRE. CIRCUITS INDICATED WITH A 2 POLE CIRCUIT BREAKER SHALL BE PROVIDED WITH 2 HOT CONDUCTORS, A NEUTRAL CONDUCTOR AND EQUIPMENT GROUND WIRE. CIRCUITS THAT ARE INDICATED WITH A 3 POLE CIRCUIT BREAKER SHALL BE PROVIDED WITH 3 HOT CONDUCTORS, 1 NEUTRAL CONDUCTOR AND EQUIPMENT GROUND WIRE. IF COMMON NEUTRALS ARE USED THE NEXT LARGER CONDUCTOR SIZE SHALL BE USED FOR THE NEUTRAL CONDUCTOR.
- 50- ALL SUPPLY FANS AND AIR HANDLERS THAT ARE SHOWN ON THE MECHANICAL DRAWINGS, THAT ARE RATED 2000 CFM AND LARGER SHALL BE FURNISHED WITH A DUCT SMOKE DETECTOR THAT SHALL BE WIRED TO THE FIRE ALARM PANEL AND TO 120V, 20AMP. EMERGENCY CIRCUIT IN THE NEAREST EMERGENCY PANEL.
- 51- ALL FIRE SMOKE DAMPERS OR MOTORIZED DAMPERS SHOWN ON THE MECHANICAL DRAWINGS SHALL BE CONNECTED BOTH TO THE FIRE ALARM PANEL AND TO A 120 VOLT 20 AMP. EMERGENCY CIRCUIT IN THE NEAREST EMERGENCY PANEL.
- 52- ALL FLOW AND TAMPER SWITCHES SHOWN ON THE FIRE SPRINKLER DRAWINGS SHALL BE CONNECTED TO THE FIRE ALARM PANEL.
- 53- HE CONTRACTOR SHALL PROVIDE AND INFRARED (THERMOGRAPH) SCAN TEST OF ALL ALUMINUM CONDUCTORS AND BUS BARS ONCE ALL SYSTEMS ARE ON LINE AND HOT THE RESULTS OF THE TESTS SHALL BE FORWARDED TO THE ENGINEER OF RECORD FOR REVIEW AND APPROVAL.
- 54- ALL DISCONNECT SWITCHES INDICATED AS W.P. ARE NEMA 3R TYPE. ALL THE OTHER DISCONNECT SWITCHES LOCATED INSIDE THE BUILDING ARE NEMA 1 TYPE UON.
- 55- EMERGENCY WIRING CIRCUITS SHALL BE LOCATED TO MINIMIZE HAZARDS THAT MIGHT CAUSE FAILURE DUE TO FLOODING, FIRE, VANDALISM, AND OTHER ADVERSE CONDITIONS.
- 56- CODING:
- 57- ALL CABLES IN OR BELOW GRADE SHALL BE SUITABLE FOR WET LOCATIONS AS PER NEC 310.10 (C). CONDUCTORS USED FOR DIRECT BURIAL APPLICATIONS SHALL BE OF A TYPE IDENTIFIED FOR SUCH USE.
- 58- PROVIDE PERMANENT SIGNAGE ON ALL EMERGENCY MAINS AND WHERE REQUIRED AS PER NEC. 700.8 (A).
- 59- PROVIDE SHUNT TRIP BUTTON FOR ALL MAINS IN THE FIRE COMMAND ROOM.
- 60- THE CONTRACTOR SHALL USE CAUTION AND BE SOLELY RESPONSIBLE FOR LOCATION OF ALL EXISTING UTILITIES AND SYSTEMS PRIOR TO COMMENCING ANY EXCAVATION, CORE DRILLING, ETC... EMPLOY AN UNDERGROUND SERVICE LOCATOR FIRM TO ENSURE THAT EXISTING UTILITIES ARE
- CONTRACTOR SHALL REPAIR ANY DAMAGE TO EXISTING UTILITIES AND SYSTEMS WHICH OCCURS AS A RESULT OF OPERATIONS PERFORMED UNDER THIS CONTRACT. REPAIRS TO EXISTING SHALL BE BY THE ENGINEER PRIOR TO RE-COVERING.
- 61- THE CONTRACTOR SHALL SUPPLY AND INSTALL ALL THE REQUIRED GROUNDING CONDUCTORS, CONNECTORS AND RODS TO COMPLETE THE GROUNDING ELECTRODE SYSTEM AND GROUND RING AS PER NEC 250.50 THROUGH NEC 250.64 INCLUSIVE.
- 62- ALL MULTIBRANCH CIRCUITS SHALL BE INSTALLED PER NEC.210.4 (A,B&C).
- 63- INSTALL ALL VERTICAL CONDUITS & RELATED WIRES SUPPORTED PER NEC.300.11.
- 64- GENERAL CONTRACTOR SHALL COORDINATE WITH THE ELEVATOR SUPPLIER/INSTALLER TO PROVIDE THE REQUIRED ELEVATOR HOISTWAYS ILLUMINATION AS PER ELEVATOR SAFETY CODE ASME A17.1.
- 65- THE CONTRACTOR SHALL FURNISH AND INSTALL PADLOCKING TYPE CIRCUIT BREAKER MECHANISMS ON CIRCUIT BREAKERS SERVING DWELLING UNIT'S PERMANENTLY CONNECTED APPLIANCES AS REQUIRED BY NEC 422.31 AND 422.33.
- 66- ALL FIRE SMOKE DAMPERS, MOTORIZED DAMPERS AND MAGNETIC RELEASE SMOKE DOORS SHOWN ON MECHANICAL AND ARCHITECTURAL DRAWINGS RESPECTIVELY SHALL BE CONNECTED BOTH TO THE FIRE ALARM PANEL AND TO A 120 VOLT – 20 AMP EMERGENCY CIRCUIT IN THE NEAREST EMERGENCY PANEL UON.
- 67- CONTRACTOR SHALL FURNISH AND INSTALL SINGLE TUBE (28W-T5) CONTINUOUS FLUORESCENT STRIP LIGHT FIXTURE (ONE LIGHT AT EACH FLOOR) WITH LENS AND WIRE GUARD ALONG THE ELEVATOR HOISTWAY. THESE LIGHT FIXTURES SHALL BE RATED FOR WET LOCATION. ELECTRICAL EQUIPMENT PLACEMENT AND INSTALLATION SHALL BE COORDINATED WITH THE ELEVATOR CONTRACTOR.

GEN. LIGHT. NOTES

1. ALL LUMINARIES SHALL BEAR THE LISTING # FROM NATIONALLY RECOGNIZED TESTING LABORATORY.
2. LIGHTING FIXTURE SUPPLIER SHALL FURNISH FOUR (4) COPIES OF LIGHTING FIXTURE CATALOG CUTS AND RECEIVE APPROVAL BY ELECTRICAL ENGINEER AND ARCHITECT PRIOR TO SUPPLYING FIXTURES. ANY PROPOSED SUBSTITUTION MUST BE SUBMITTED FOR PRIOR APPROVAL.
3. CONTRACTOR SHALL VERIFY THE QUANTITY AND LOCATION OF THE OCCUPANCY SENSORS AS PER MANUFACTURER'S SPECIFICATIONS.
4. CONTRACTOR SHALL COORDINATE THE EXACT LOCATION AND TYPE OF THE LIGHT FIXTURES WITH ARCHITECTURAL AND INTERIOR DESIGNER DRAWINGS AND VERIFY APPROPRIATE CLEARANCE AND APPLICATION WITH ALL ARCHITECTURAL FINISHES PRIOR BID.
5. CONTRACTOR SHALL VERIFY VOLTAGE OF ALL LIGHT FIXTURES PRIOR TO BIDDING.

Bauen Consultants
ENGINEERING & ARCHITECTURE

CONTACT: 773-937-0712
ADDRESS:128 DAV LN LONDON KY 40741

THIS DRAWING IS PROVIDED AS AN INSTRUMENT OF SERVICE BY THE ARCHITECT AND IS INTENDED FOR USE ON THIS PROJECT ONLY. THE DRAWING REMAINS THE PROPERTY OF THE ARCHITECT AND SHALL BE RETURNED TO HIM/HER UPON COMPLETION OF THE CONSTRUCTION WORK. PURSUANT TO THE ARCHITECTURAL WORKS COPYRIGHT PROTECTION ACT OF 1990, ALL DRAWINGS, SPECIFICATIONS, IDEAS, AND DESIGNS, INCLUDING THE OVERALL FORM, ARRANGEMENT, AND COMPOSITION OF THE SPACES, AND ELEMENTS APPEARING HEREIN, CONSTITUTES THE COPYRIGHT WORK OF THE ARCHITECT. ANY REPRODUCTION, USE, OR DISCLOSURE OF INFORMATION CONTAINED HEREIN WITHOUT PRIOR WRITTEN CONSENT OF THE ARCHITECT IS STRICTLY PROHIBITED.

GENERAL PLAN NOTES

OWNER TO PERFORM THE FOLLOWING BEFORE CONSTRUCTION COMMENCES. DESIGNER ASSUMES NO LIABILITY FOR CONSTRUCTION:

1. BUILDER OR CONTRACTOR SHALL VERIFY ALL DIMENSIONS PRIOR TO PROCEEDING WITH CONSTRUCTION.
2. BUILDER OR CONTRACTOR SHALL VERIFY COMPLIANCE WITH CITY AMENDMENTS TO IRC.
3. DO NOT USE SCALED DIMENSIONS; USE ONLY DIMENSIONS AS CALLED OUT. WHEN NO DIMENSION IS PROVIDED, CONSULT WITH THE OWNER BEFORE PROCEEDING WITH WORK.
4. CONTRACTOR SHALL VERIFY ALL EXISTING CONDITIONS, SITE UTILITY SERVICES AND DIMENSIONS AND NOTIFY ARCHITECT OF DISCREPANCIES THAT MAY AFFECT THE EXECUTION OF THE WORK BEFORE PROCEEDING.
5. OMISSIONS OR CONFLICTS WITHIN THE DRAWINGS, NOTES OR DETAILS SHALL BE REPORTED THE OWNER BEFORE PROCEEDING WITH WORK.
6. DETAILS TAKE PRECEDENCE DRAWING NOTES

REVISION SCHEDULE		
REV. #	NAME	DATE

PROPOSED ONE STORY
FARM HOUSE

264 CROCKETT RD WEATHERFORD TX
76088

ELECTRICAL NOTES

DATE 01.31.2025


E001

SCALE AS INDICATED ON IIX17



LOAD CALCULATION "A"		
GENERAL LIGHTING LOAD SQ FT @ 3VA/SQ FT		12450 VA
SMALL APPLIANCE CIRCUIT		3000 VA
COOKTOP AND OVEN UNITS		5100 VA
WASHER		1500 VA
DRYER		5000 VA
MICROWAVE		1400 VA
REFRIGERATOR		1500 VA
DISH-WASHER		1200 VA
GARBAGE DISPOSAL		1600 VA
HOOD		400 VA
SMOKE DETECTORS		500 VA
WATER HEATER		9000 VA
AIR CONDITIONING UNITS		7425.6 VA
TOTAL		50076 VA
DEMAND LOAD NFPA 70 (NEC) (220.82)		
AIR CONDITIONING UNITS		7425.60 VA
28221.65 x 0.4 DF		11288.66 VA
10000 x 1.0 DF		10000.00 VA
TOTAL DEMAND LOAD		28714.26 VA
		138.05 A



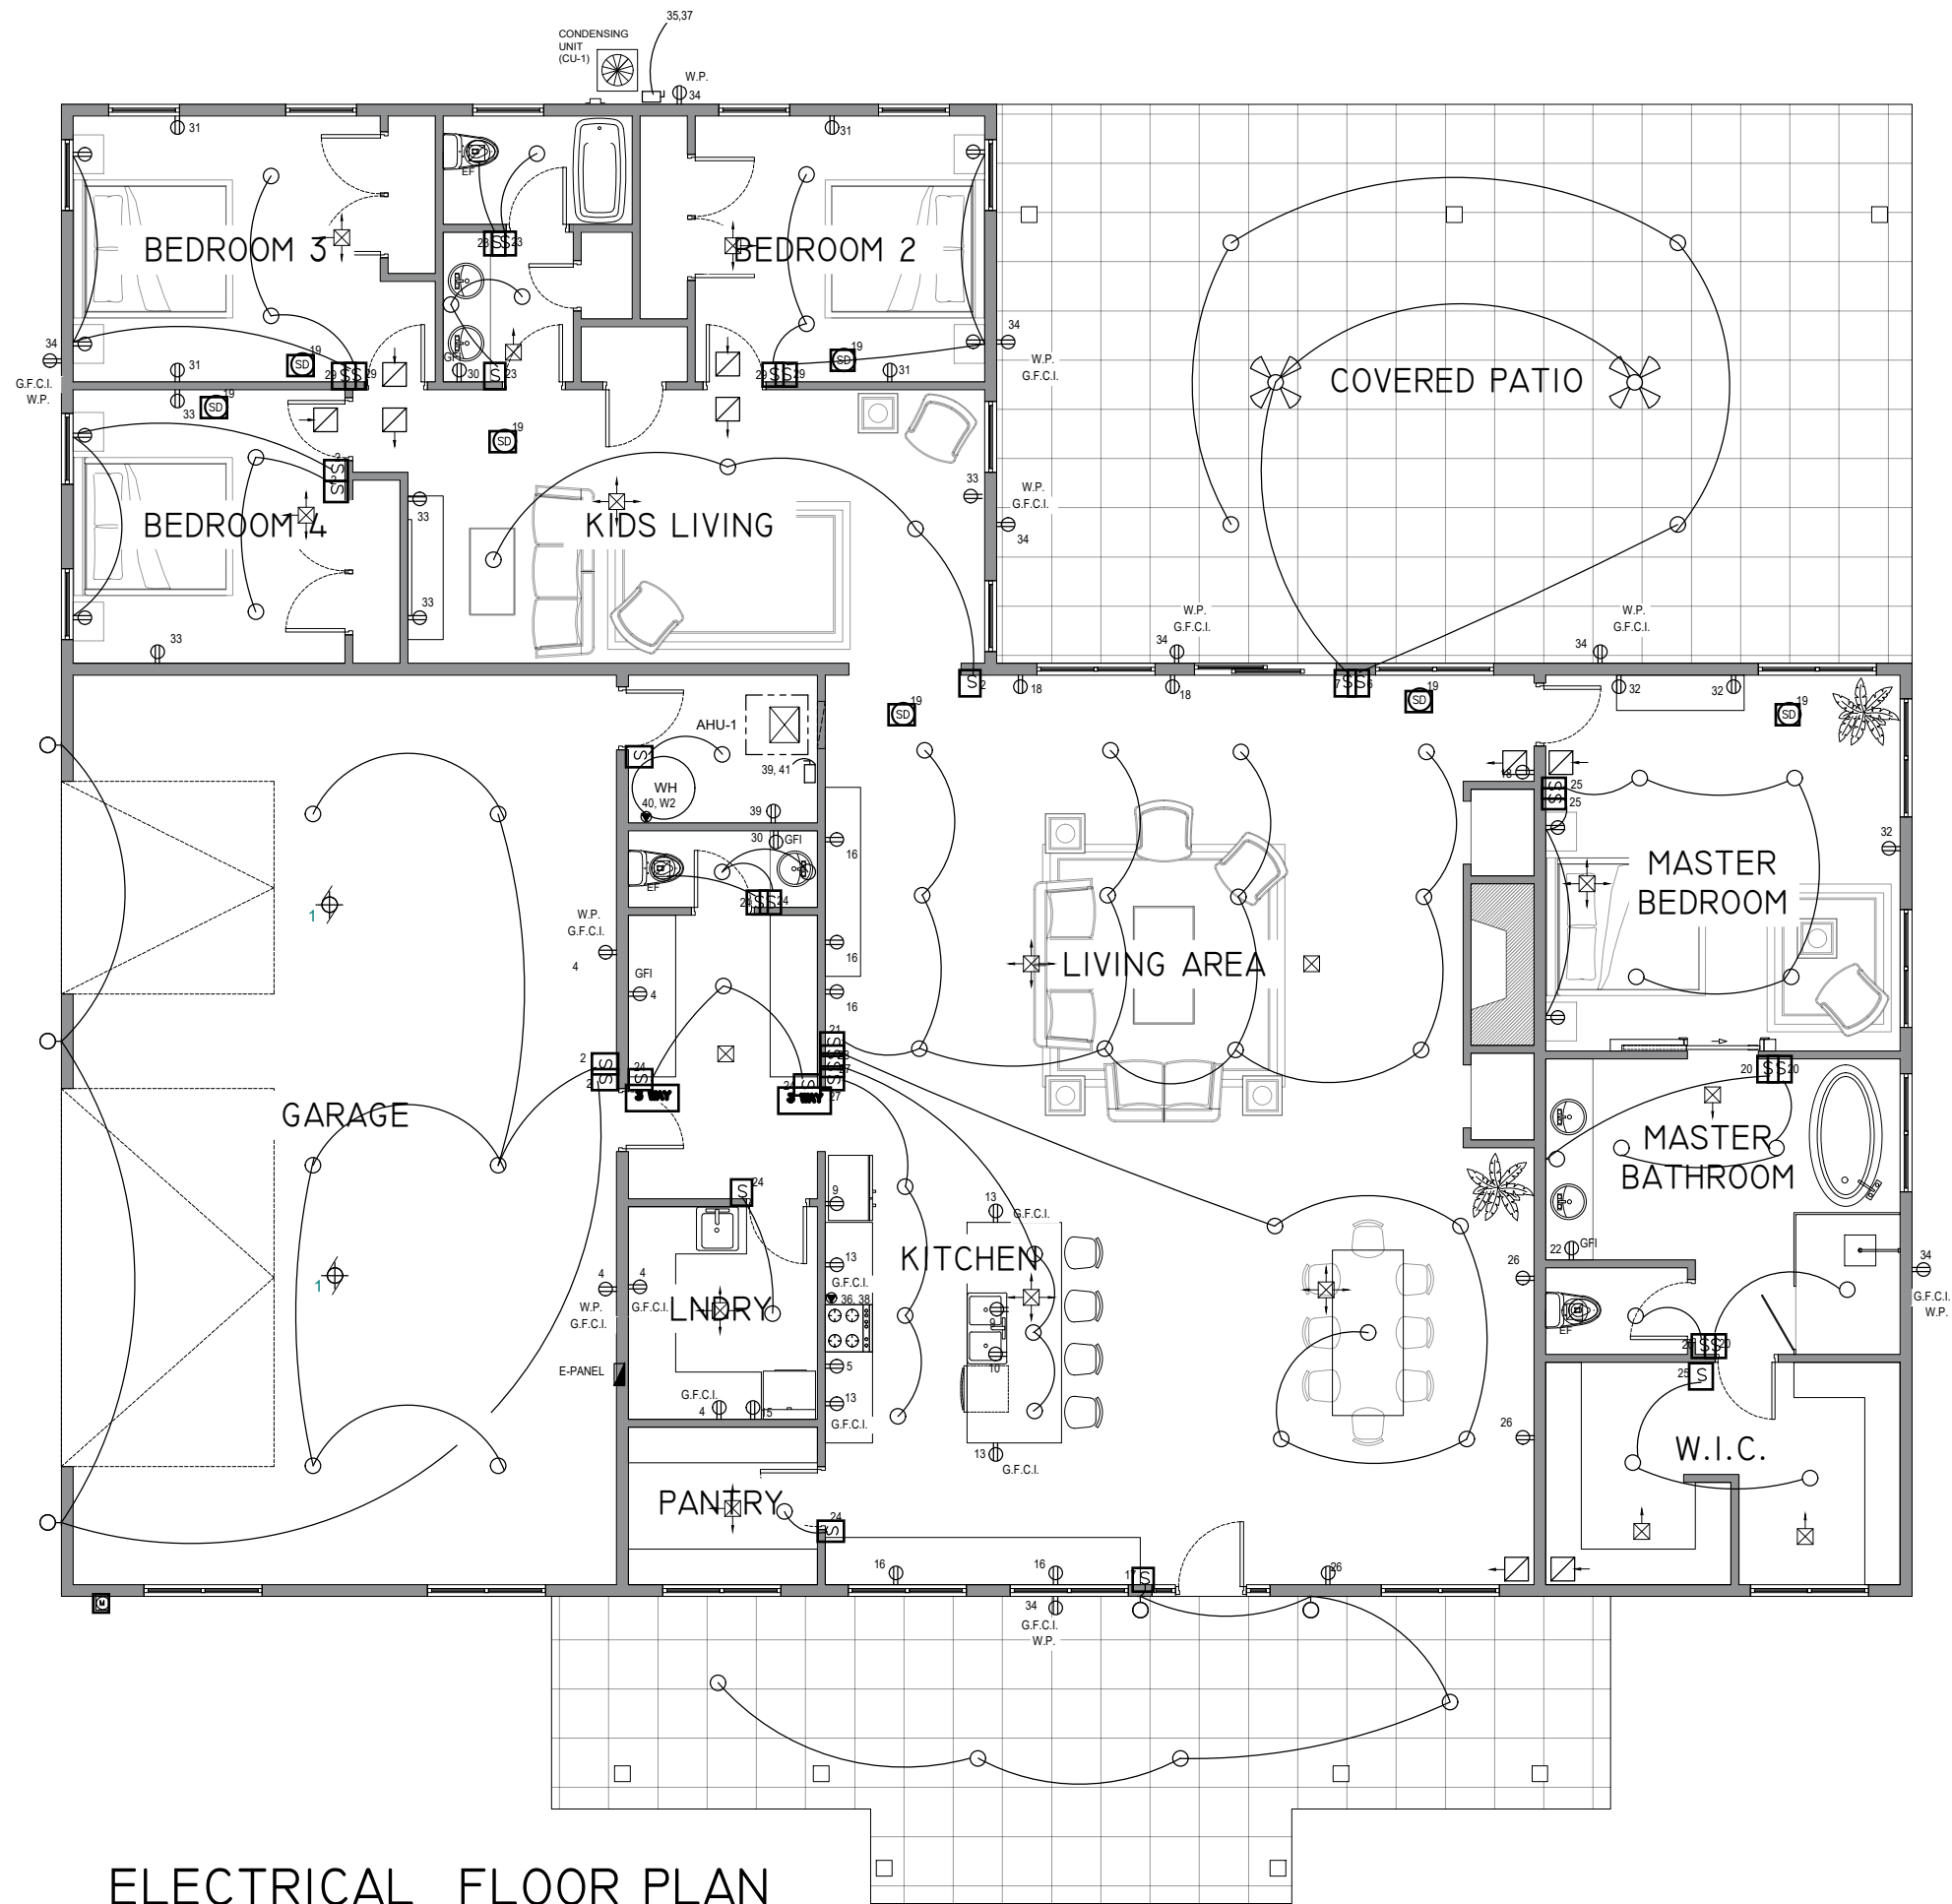

ELECTRICAL FLOOR PLAN
SCALE 1/8"=1'-0"

Bauen Consultants
ENGINEERING & ARCHITECTURE

CONTACT: 773-937-0712
ADDRESS: 128 DAV LN LONDON KY 40741

THIS DRAWING IS PROVIDED AS AN INSTRUMENT OF SERVICE BY THE ARCHITECT AND IS INTENDED FOR USE ON THIS PROJECT ONLY. THE DRAWING REMAINS THE PROPERTY OF THE ARCHITECT AND SHALL BE RETURNED TO HIM/HER UPON COMPLETION OF THE CONSTRUCTION WORK. PURSUANT TO THE ARCHITECTURAL WORKS COPYRIGHT PROTECTION ACT OF 1990, ALL DRAWINGS, SPECIFICATIONS, IDEAS, AND DESIGNS, INCLUDING THE OVERALL FORM, ARRANGEMENT, AND COMPOSITION OF THE SPACES, AND ELEMENTS APPEARING HEREIN, CONSTITUTES THE COPYRIGHT WORK OF THE ARCHITECT. ANY REPRODUCTION, USE, OR DISCLOSURE OF INFORMATION CONTAINED HEREIN WITHOUT PRIOR WRITTEN CONSENT OF THE ARCHITECT IS STRICTLY PROHIBITED.

GENERAL PLAN NOTES

- OWNER TO PERFORM THE FOLLOWING BEFORE CONSTRUCTION COMMENCES. DESIGNER ASSUMES NO LIABILITY FOR CONSTRUCTION:
1. BUILDER OR CONTRACTOR SHALL VERIFY ALL DIMENSIONS PRIOR TO PROCEEDING WITH CONSTRUCTION.
 2. BUILDER OR CONTRACTOR SHALL VERIFY COMPLIANCE WITH CITY AMENDMENTS TO **IRC**.
 3. DO NOT USE SCALED DIMENSIONS; USE ONLY DIMENSIONS AS CALLED OUT. WHEN NO DIMENSION IS PROVIDED, CONSULT WITH THE OWNER BEFORE PROCEEDING WITH WORK.
 4. CONTRACTOR SHALL VERIFY ALL EXISTING CONDITIONS, SITE UTILITY SERVICES AND DIMENSIONS AND NOTIFY ARCHITECT OF DISCREPANCIES THAT MAY AFFECT THE EXECUTION OF THE WORK BEFORE PROCEEDING.
 5. OMISSIONS OR CONFLICTS WITHIN THE DRAWINGS, NOTES OR DETAILS SHALL BE REPORTED THE OWNER BEFORE PROCEEDING WITH WORK.
 6. DETAILS TAKE PRECEDENCE DRAWING NOTES

REVISION SCHEDULE

REV. #	NAME	DATE

PROPOSED ONE STORY FARM HOUSE


264 CROCKETT RD WEATHERFORD TX 76088

ELECTRICAL FLOOR PLAN

DATE 01.31.2025

E101


SCALE AS INDICATED ON I1X17

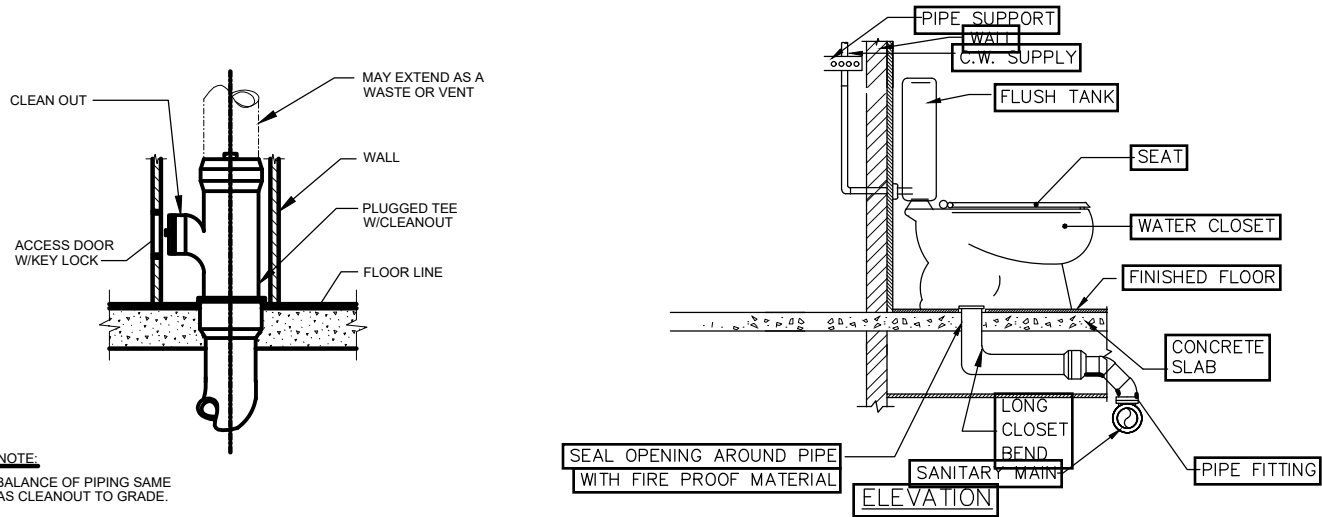

NOTE:
BALANCE OF PIPING SAME
AS CLEANOUT TO GRADE.


1 WALL CLEANOUT DETAIL
NTS

2 FLOOR MOUNTED WATER CLOSET DETAIL
NTS

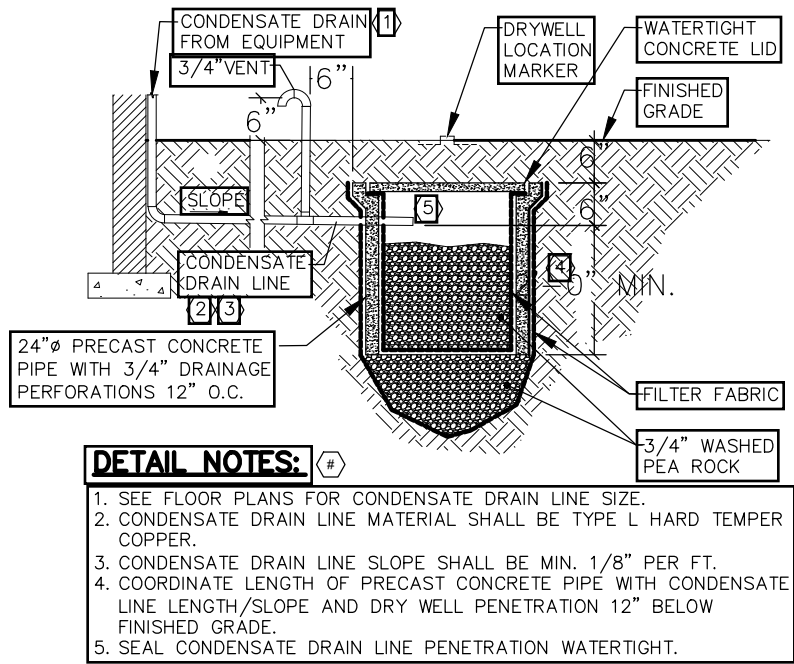

DETAIL NOTES:

1. SEE FLOOR PLANS FOR CONDENSATE DRAIN LINE SIZE.
2. CONDENSATE DRAIN LINE MATERIAL SHALL BE TYPE L HARD TEMPER COPPER.
3. CONDENSATE DRAIN LINE SLOPE SHALL BE MIN. 1/8" PER FT.
4. COORDINATE LENGTH OF PRECAST CONCRETE PIPE WITH CONDENSATE LINE LENGTH/SLOPE AND DRY WELL PENETRATION 12" BELOW FINISHED GRADE.
5. SEAL CONDENSATE DRAIN LINE PENETRATION WATERTIGHT.

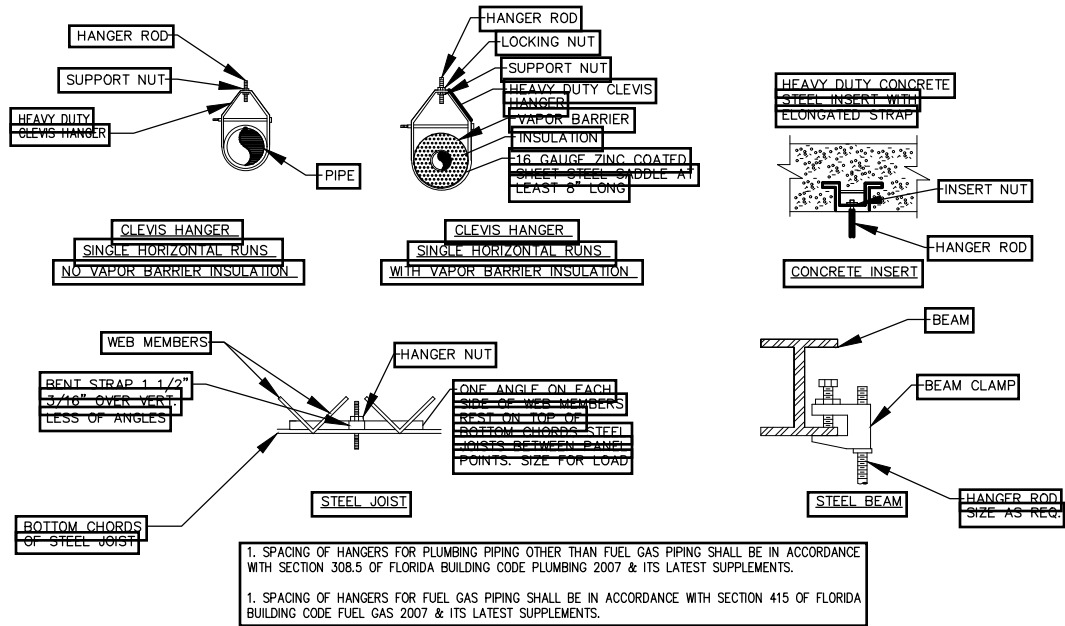

4 PIPE SUPPORTS DETAILS
NTS

PLUMBING NOTES:

1. THE PLUMBING SYSTEM DESIGN, INSTALLATION, AND MATERIALS SHALL CONFORM TO THE PLUMBING CODE AND AUTHORITIES HAVING JURISDICTION. IN CASE OF CONFLICTS WITH CODES, DRAWINGS, OR SPECIFICATIONS, THE MOST STRINGENT SHALL PREVAIL.
2. BEFORE COMMENCEMENT OF WORK, THE CONTRACTOR SHALL VERIFY THE EXACT LOCATIONS, ELEVATIONS, AND CHARACTERISTICS OF ALL UTILITIES AND PIPING, AND SHALL IMMEDIATELY NOTIFY THE ARCHITECT OF ANY DISCREPANCIES.
3. THE PLUMBING CONTRACTOR SHALL PROVIDE THE WATER, SEWER, AND STORM DRAIN SYSTEMS TO A POINT OF CONNECTION OUTSIDE OF THE BUILDING AND SHALL MEET THE INVERT ELEVATION SHOWN ON THE CIVIL DRAWINGS. COORDINATE WITH LOCAL UTILITIES, CIVIL DRAWINGS AND ADDITIONAL CONSTRUCTION DOCUMENTS AS REQUIRED.
4. THE CONTRACTOR SHALL MAKE ALL ARRANGEMENTS WITH UTILITY COMPANIES FOR SERVICES AND CONNECTION AND SHALL MAKE APPLICATION FOR SERVICE AND PERMITS IN THE NAME OF THE OWNER AND SHALL PAY ALL FEES AND CHARGES INCLUDING THE COST OF VAULTS AND METERS. CONTRACTOR SHALL MAKE VARIATIONS PER UTILITY COMPANY'S REQUIREMENT WITHOUT CHARGING EXTRA TO THE BID CONTRACT.
5. ALL PLUMBING WORK SHALL BE INSTALLED SO AS TO AVOID INTERFERENCE WITH ELECTRICAL EQUIPMENT, MECHANICAL EQUIPMENT, AND STRUCTURAL FRAMING, SKYLIGHT, ETC.
6. COORDINATE ALL LOCATIONS, SIZES, AND ELEVATIONS OF ALL SLEEVES THROUGH WALLS, BEAMS, SLABS, AND FOOTING WITH STRUCTURAL AND ARCHITECTURAL DRAWINGS. ALL PIPES SLEEVING THROUGH BEAM SHALL HAVE A SLEEVE DIAMETER OF TWO PIPE SIZES OVER THE PIPE PASSING THROUGH THE FOOTING OR PER STRUCTURAL DRAWING. THE MOST STRINGENT SHALL PREVAIL.
7. PIPING SUPPORTS. ALL PIPING TO BE SUPPORTED WITH HANGERS AND BRACKETS WHICH PROVIDE ISOLATION FROM FRAMING. CONTACT BETWEEN PIPE AND SUPPORT TO BE LINED WITH PLASTIC OR FELT.
8. ALL FLOOR AND WALL PENETRATIONS MUST BE SEALED WATERTIGHT AND VERMIN PROOF.
9. EXACT LOCATIONS AND MOUNTING HEIGHTS OF PLUMBING FIXTURES SHALL BE OBTAINED FROM THE ARCHITECTURAL DRAWINGS.
10. SEE ARCHITECTURAL DRAWINGS FOR HANDICAP FIXTURE LOCATIONS AND MOUNTING HEIGHTS. INSULATE ALL EXPOSED HOT WATER AND DRAIN PIPING BELOW HANDICAP LAVATORIES AND SINKS WITH INSULATING TAPE AND OFFSET P-TRAP AGAINST WALL. ALL FLUSH VALVES FOR HANDICAP SHALL BE LOCATED ON HANDICAP WHEELCHAIR ACCESS SIDE OF STALL.
11. ALL CLEAN OUTS SHALL BE INSTALLED WHERE READILY ACCESSIBLE. THE CONTRACTOR SHALL COORDINATE ALL CLEAN OUT LOCATIONS OF EQUIPMENT, CABINETS, ETC. WITH THE ARCHITECT PRIOR TO ANY INSTALLATION.
12. ALL VALVES, TRAP PRIMERS, WATER HAMMER ARRESTORS OR OTHER EQUIPMENT SHOWN IN WALLS OR ABOVE NON-ACCESSIBLE CEILINGS SHALL BE INSTALLED BEHIND AN ACCESS PANEL. COORDINATE LOCATION WITH ARCHITECT.
13. PLUMBING CONTRACTOR SHALL VISIT THE JOB SITE PRIOR TO BASE BID. HE SHALL FAMILIARIZE HIMSELF WITH ALL EXISTING CONDITIONS AND FUTURE WORK TO BE DONE. HE SHALL INCLUDE ALL HIS SITE INFORMATION AND CONDITIONS WITHIN HIS BASE BID. HE SHALL BE RESPONSIBLE FOR COMPLETE AND FULLY FUNCTIONING PLUMBING SYSTEMS.
14. PLUMBING CONTRACTOR SHALL COORDINATE COMPLETE PLUMBING INSTALLATION AND REQUIREMENTS PRIOR TO BASE BID WITH ALL LOCAL DISTRICTS AND GOVERNING AUTHORITIES. INCLUDE ALL FINDINGS WITHIN THE BASE BID.
15. ALL DRY SYSTEM PIPING SHALL BE INSTALLED WITH PROPER PITCH FOR DRAINING OF SYSTEM.
16. PROVIDE ALL WORK IN COMPLIANCE WITH ALL LOCAL, STATE, AND FEDERAL CODES. OBTAIN ALL REQUIRED PERMITS.
17. FIELD VERIFY EXACT LOCATION, COMPOSITION AND CONDITION OF ALL PIPING, VALVES AND SYSTEMS AS REQUIRED FOR WORK OF THE CONTRACT.
18. PROVIDE CUTTING, CORING, AND PATCHING OF ALL WALLS, SLABS, AND DECKS AS REQUIRED FOR WORK SHOWN. COORDINATE ALL WORK WITH OWNER AND GENERAL CONTRACTOR.
19. PROVIDE ALL REQUIRED EXCAVATION, BACKFILL, AND COMPACTION FOR ALL UNDERGROUND WORK.
20. REMOVE AND REPLACE EXISTING CEILINGS AS REQUIRED FOR WORK SHOWN. REPLACE ALL DAMAGED CEILINGS; PROVIDE NEW CEILINGS. FIELD VERIFY CEILING TYPES AND EXTENT OF THIS WORK PRIOR TO BID DATE AND INCLUDE IT IN THE BID.
21. COORDINATE ALL VENT TERMINATIONS ABOVE ROOF WITH HVAC CONTRACTOR. ALL VENT TERMINATIONS ABOVE ROOF SHALL BE A MINIMUM 10'-0" AWAY FROM ANY HVAC OUTSIDE AIR INTAKE (ROOFTOP UNIT, LOUVER, ETC.).
22. PROVIDE HOSE BIBB (HB) UNDER LAVATORY IN ALL TOILET ROOMS WITH FLOOR DRAINS.
23. CONNECT TO SITE PIPING OUTSIDE BUILDING AS SHOWN. PROVIDE ALL REQUIRED OFFSETS, FITTINGS, AND CONNECTIONS. FIELD VERIFY EXACT LOCATION, DEPTH, AND COMPOSITION OF SITE SERVICES AND COORDINATE ALL WORK WITH SITE CONTRACTOR.
24. PROVIDE SCHEDULE 40 BLACK STEEL PIPE SLEEVES FOR ALL UNDERGROUND PIPING PASSING THROUGH OR UNDER FOOTINGS, WALLS, FOUNDATION WALLS, SLABS, FLOORS, AND/OR UNDERGROUND STRUCTURES. REFER TO THE PROJECT SPECIFICATIONS FOR ADDITIONAL REQUIREMENTS.
25. WHERE PIPING IS LOCATED OVER FOOTINGS AND/OR OTHER UNDERGROUND STRUCTURES, ROLL DOWN AS REQUIRED TO CONNECT TO SYSTEMS NOTED. PROVIDE ALL REQUIRED OFFSETS, FITTINGS, AND CONNECTIONS.
26. PITCH ALL SANITARY, WASTE, AND STORM PIPING AS FOLLOWS: PIPING 2 1/2" AND SMALLER, PITCH AT 2 PERCENT (1/4" PER FOOT) MINIMUM. PIPING 3" AND LARGER, PITCH AT 1 PERCENT (1/8" PER FOOT) MINIMUM.
27. WATER OR WASTE PIPE BELOW GRADE OUTSIDE THE BUILDING SHALL HAVE MINIMUM COVER AS RECOMMENDED BY LOCAL AUTHORITIES.
28. SUBMITTALS AND SHOP DRAWINGS. AS SOON AS POSSIBLE AND WITHIN 31 DAYS AFTER AWARD OF THE CONTRACT, AND BEFORE THEIR PURCHASE, THE CONTRACTOR SHALL PROVIDE THE ARCHITECT COMPLETE SUBMITTALS FOR APPROVAL AND CONTAINING A COMPLETE LIST OF MATERIALS, SPECIALITIES, AND EQUIPMENT HE IS TO FURNISH FOR THE INSTALLATION. ALL SUBMITTALS SHALL BE MADE AT ONE TIME.
29. PLATFORMS, CURBS, AND FLUSHINGS FOR PLUMBING EQUIPMENT SHALL BE AS INDICATED ON THE STRUCTURAL AND ARCHITECTURAL PLANS, UNLESS NOTED OTHERWISE, COORDINATE EXACT SIZES OF REQUIRED OPENINGS AND SUPPORTS FOR FURNISHED EQUIPMENT.
30. ALL HOSE BIBBS, WALL HYDRANTS, AND MOP SERVICE BASINS SHALL BE EQUIPPED WITH APPROVED, PROPERLY INSTALLED, ATMOSPHERIC TYPE VACUUM BREAKERS.
31. EACH PLUMBING VENT SHALL TERMINATE NOT LESS THAN 10'-0" FEET FROM OR AT LEAST 3 FEET ABOVE ANY WINDOW, DOOR, OPENING, AIR INTAKE OR VENT SHAFT.
32. CONTRACTOR SHALL INSULATE TRAP AND TRAP ARM AND HOT WATER STOP AND SUPPLY FOR ALL HANDICAPPED LAVATORIES.
33. PROVIDE SHUT OFF VALVE (BALL VALVE) FOR EACH C, H, HWR, AND HAS RISER TO UNITS AND BRANCH TO PUBLIC AREAS OR FIXTURES.
34. ALL VALVES, UNIONS, ETC. TO BE SAME SIZE AS PIPE UNLESS OTHERWISE INDICATED ON DRAWINGS.
35. UNIONS SHALL BE PROVIDED AND INSTALLED AFTER EACH SCREW - TYPE VALVE AND PRIOR TO EQUIPMENT CONNECTIONS.
36. THE PLUMBING CONTRACTOR SHALL COORDINATE ALL REQUIREMENTS FOR ALL POINTS OF CONNECTION.
37. CONTRACTOR SHALL PROVIDE ALL VALVES AND BACKFLOW PREVENTION DEVICES AS REQUIRED BY STATE AND LOCAL CODES.
38. PVC PIPING SHALL BE USED FOR SANITARY PIPING WHERE APPROVED BY LOCAL AUTHORITY HAVING JURISDICTION AND ALL OTHER APPLICABLE CODES.
39. PEX PIPING SHALL BE USED FOR DOMESTIC WATER SUPPLY LINES WHERE APPROVED BY LOCAL AUTHORITY HAVING JURISDICTION AND ALL OTHER APPLICABLE CODES.

Bauen Consultants
ENGINEERING & ARCHITECTURE

CONTACT: 773-937-0712
ADDRESS: 128 DAV LN LONDON KY 40741

THIS DRAWING IS PROVIDED AS AN INSTRUMENT OF SERVICE BY THE ARCHITECT AND IS INTENDED FOR USE ON THIS PROJECT ONLY. THE DRAWING REMAINS THE PROPERTY OF THE ARCHITECT AND SHALL BE RETURNED TO HIM/HER UPON COMPLETION OF THE CONSTRUCTION WORK. PURSUANT TO THE ARCHITECTURAL WORKS COPYRIGHT PROTECTION ACT OF 1990, ALL DRAWINGS, SPECIFICATIONS, IDEAS, AND DESIGNS, INCLUDING THE OVERALL FORM, ARRANGEMENT, AND COMPOSITION OF THE SPACES, AND ELEMENTS APPEARING HEREIN, CONSTITUTES THE COPYRIGHT WORK OF THE ARCHITECT. ANY REPRODUCTION, USE, OR DISCLOSURE OF INFORMATION CONTAINED HEREIN WITHOUT PRIOR WRITTEN CONSENT OF THE ARCHITECT IS STRICTLY PROHIBITED.

GENERAL PLAN NOTES

- OWNER TO PERFORM THE FOLLOWING BEFORE CONSTRUCTION COMMENCES. DESIGNER ASSUMES NO LIABILITY FOR CONSTRUCTION:
1. BUILDER OR CONTRACTOR SHALL VERIFY ALL DIMENSIONS PRIOR TO PROCEEDING WITH CONSTRUCTION.
 2. BUILDER OR CONTRACTOR SHALL VERIFY COMPLIANCE WITH CITY AMENDMENTS TO IRC.
 3. DO NOT USE SCALED DIMENSIONS; USE ONLY DIMENSIONS AS CALLED OUT. WHEN NO DIMENSION IS PROVIDED, CONSULT WITH THE OWNER BEFORE PROCEEDING WITH WORK.
 4. CONTRACTOR SHALL VERIFY ALL EXISTING CONDITIONS, SITE UTILITY SERVICES AND DIMENSIONS AND NOTIFY ARCHITECT OF DISCREPANCIES THAT MAY AFFECT THE EXECUTION OF THE WORK BEFORE PROCEEDING.
 5. OMISSIONS OR CONFLICTS WITHIN THE DRAWINGS, NOTES OR DETAILS SHALL BE REPORTED THE OWNER BEFORE PROCEEDING WITH WORK.
 6. DETAILS TAKE PRECEDENCE DRAWING NOTES

REVISION SCHEDULE

REV. #	NAME	DATE

PROPOSED ONE STORY
FARM HOUSE


264 CROCKETT RD WEATHERFORD TX
76088

PLUMBING NOTES
AND DETAILS


DATE 01.31.2025

P001

SCALE AS INDICATED ON I/IX/7

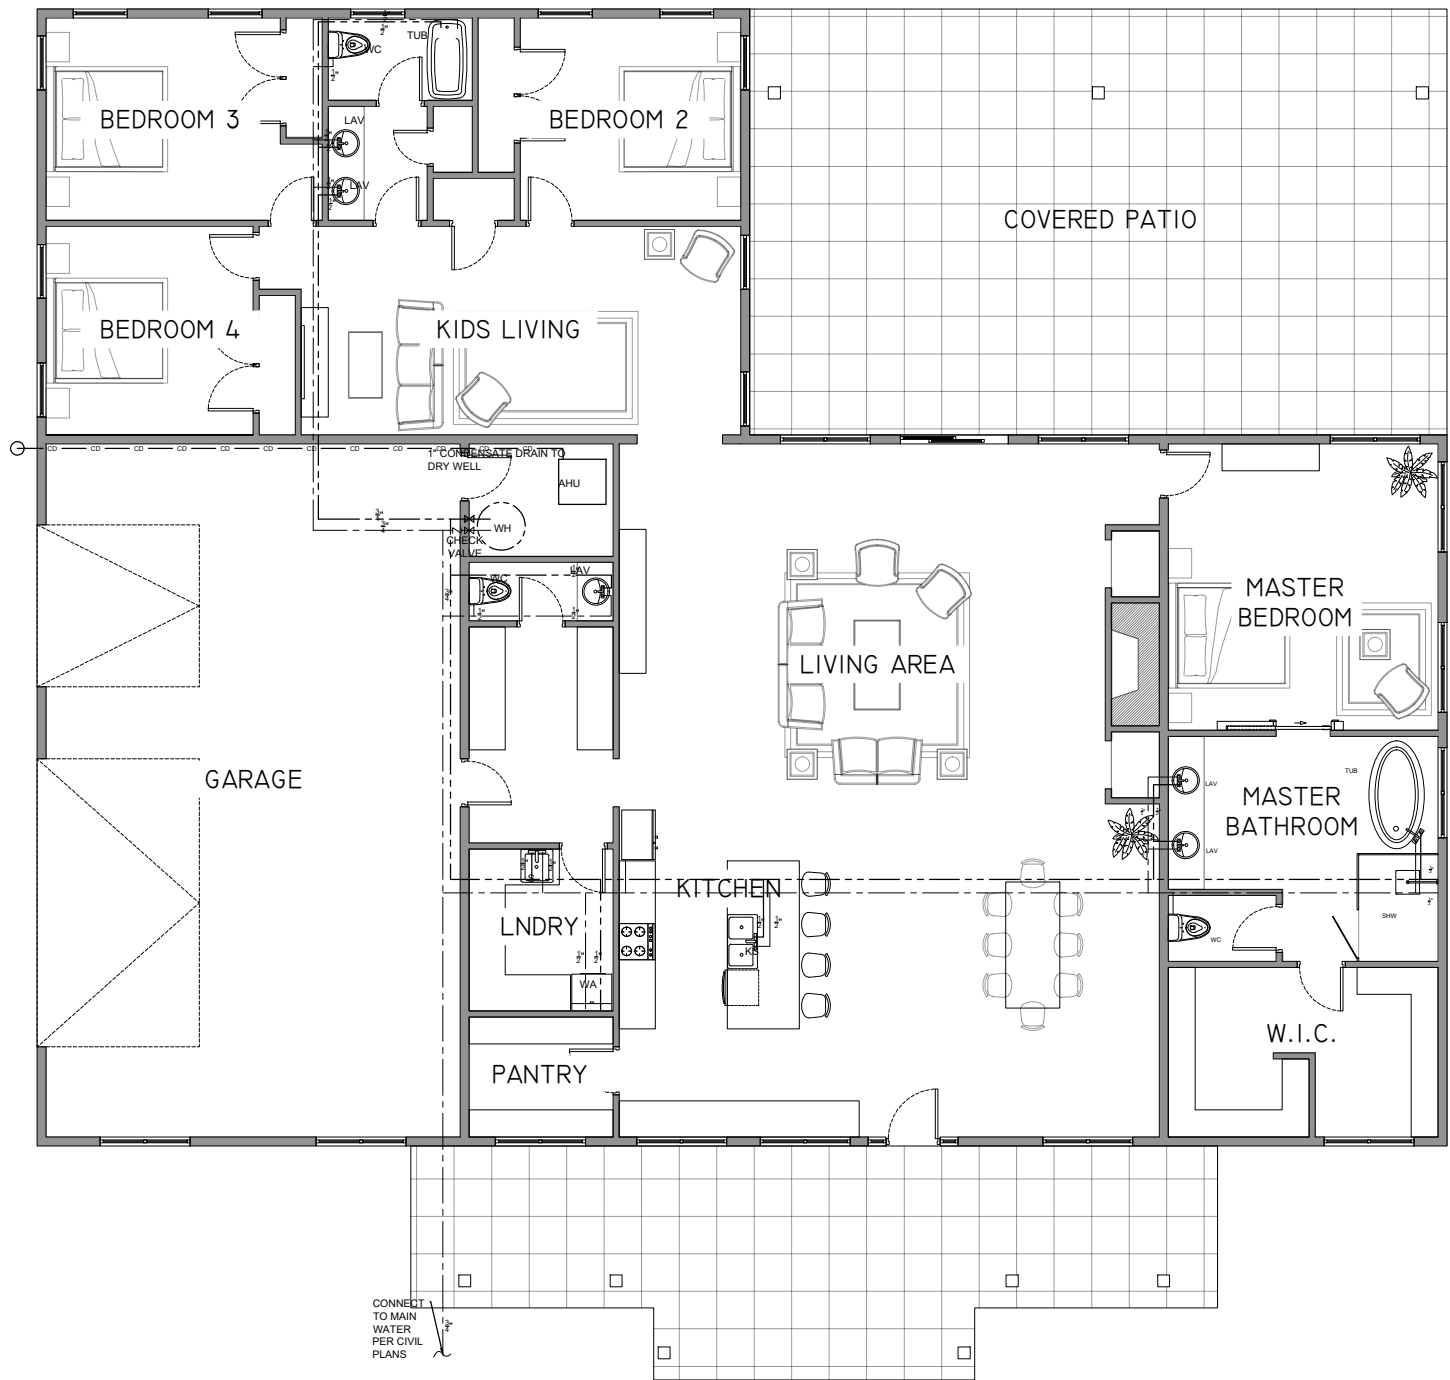

PLUMBING - WATER FLOOR PLAN
SCALE 3/32"=1'-0"

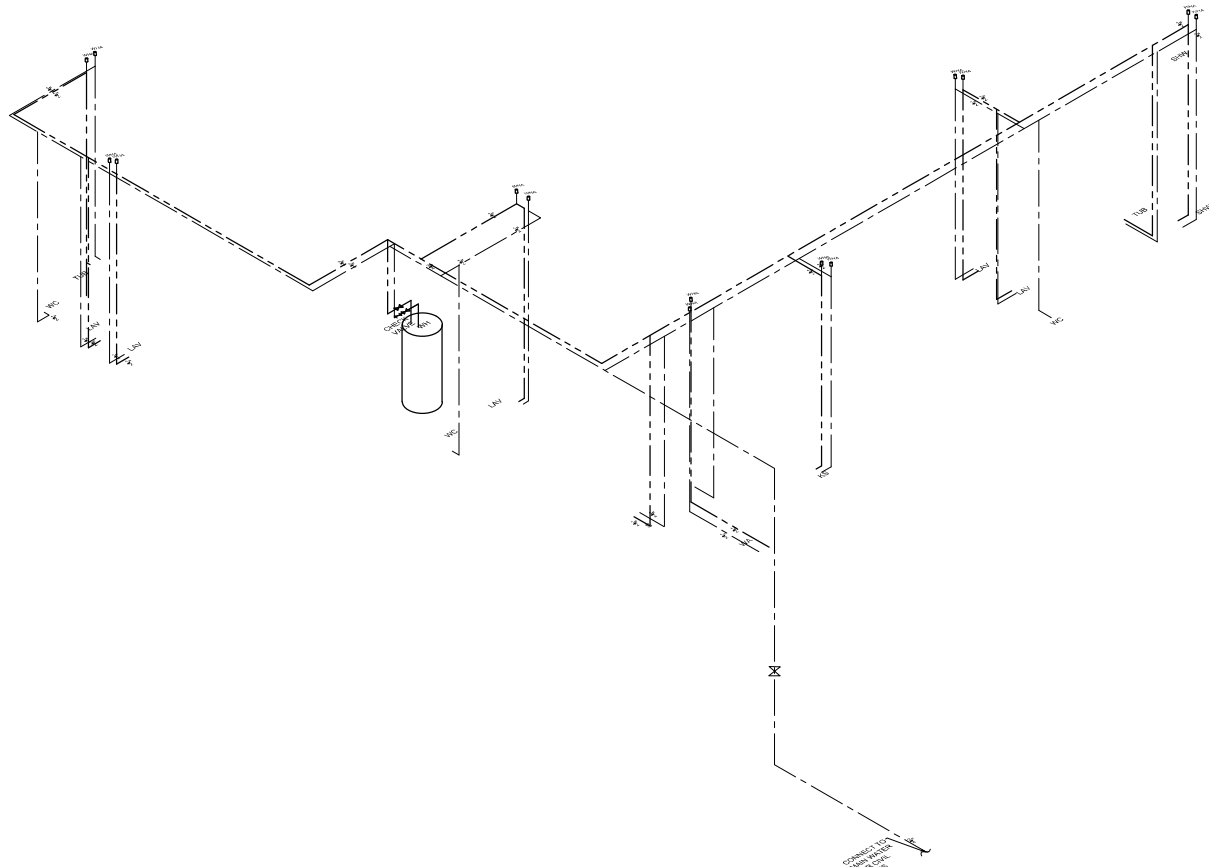

WATER RISER DIAGRAM
SCALE NTS

Bauen Consultants
ENGINEERING & ARCHITECTURE

CONTACT: 773-937-0712
ADDRESS: 128 DAV LN LONDON KY 40741

THIS DRAWING IS PROVIDED AS AN INSTRUMENT OF SERVICE BY THE ARCHITECT AND IS INTENDED FOR USE ON THIS PROJECT ONLY. THE DRAWING REMAINS THE PROPERTY OF THE ARCHITECT AND SHALL BE RETURNED TO HIM/HER UPON COMPLETION OF THE CONSTRUCTION WORK. PURSUANT TO THE ARCHITECTURAL WORKS COPYRIGHT PROTECTION ACT OF 1990, ALL DRAWINGS, SPECIFICATIONS, IDEAS, AND DESIGNS, INCLUDING THE OVERALL FORM, ARRANGEMENT, AND COMPOSITION OF THE SPACES, AND ELEMENTS APPEARING HEREIN, CONSTITUTES THE COPYRIGHT WORK OF THE ARCHITECT. ANY REPRODUCTION, USE, OR DISCLOSURE OF INFORMATION CONTAINED HEREIN WITHOUT PRIOR WRITTEN CONSENT OF THE ARCHITECT IS STRICTLY PROHIBITED.

GENERAL PLAN NOTES

OWNER TO PERFORM THE FOLLOWING BEFORE CONSTRUCTION COMMENCES. DESIGNER ASSUMES NO LIABILITY FOR CONSTRUCTION:

1. BUILDER OR CONTRACTOR SHALL VERIFY ALL DIMENSIONS PRIOR TO PROCEEDING WITH CONSTRUCTION.
2. BUILDER OR CONTRACTOR SHALL VERIFY COMPLIANCE WITH CITY AMENDMENTS TO **IRC**.
3. DO NOT USE SCALED DIMENSIONS; USE ONLY DIMENSIONS AS CALLED OUT. WHEN NO DIMENSION IS PROVIDED, CONSULT WITH THE OWNER BEFORE PROCEEDING WITH WORK.
4. CONTRACTOR SHALL VERIFY ALL EXISTING CONDITIONS, SITE UTILITY SERVICES AND DIMENSIONS AND NOTIFY ARCHITECT OF DISCREPANCIES THAT MAY AFFECT THE EXECUTION OF THE WORK BEFORE PROCEEDING.
5. OMISSIONS OR CONFLICTS WITHIN THE DRAWINGS, NOTES OR DETAILS SHALL BE REPORTED TO THE OWNER BEFORE PROCEEDING WITH WORK.
6. DETAILS TAKE PRECEDENCE DRAWING NOTES

REVISION SCHEDULE

REV. #	NAME	DATE

PROPOSED ONE STORY FARM HOUSE


264 CROCKETT RD WEATHERFORD TX 76088

PLUMBING WATER FLOOR PLAN

DATE 01.31.2025


P100

SCALE AS INDICATED ON IIX17

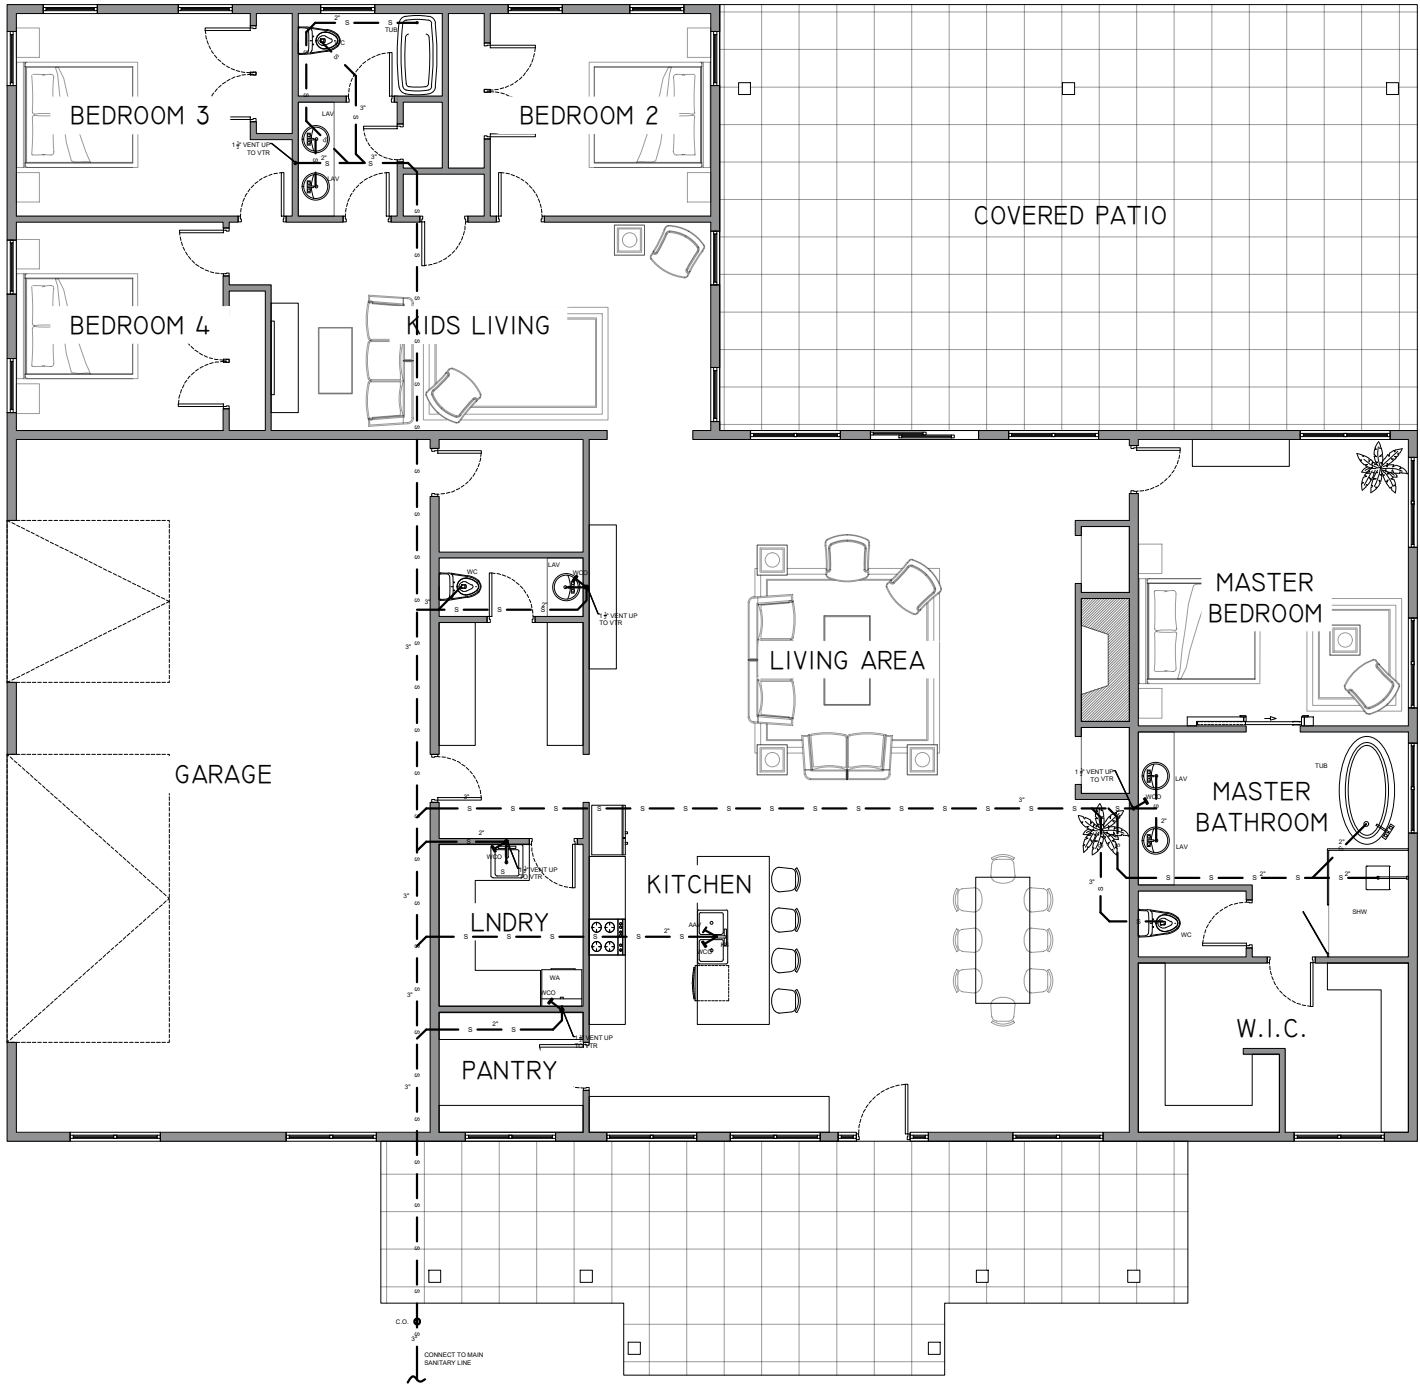

PLUMBING - SANITARY FLOOR PLAN

SCALE 3/32"=1'-0"

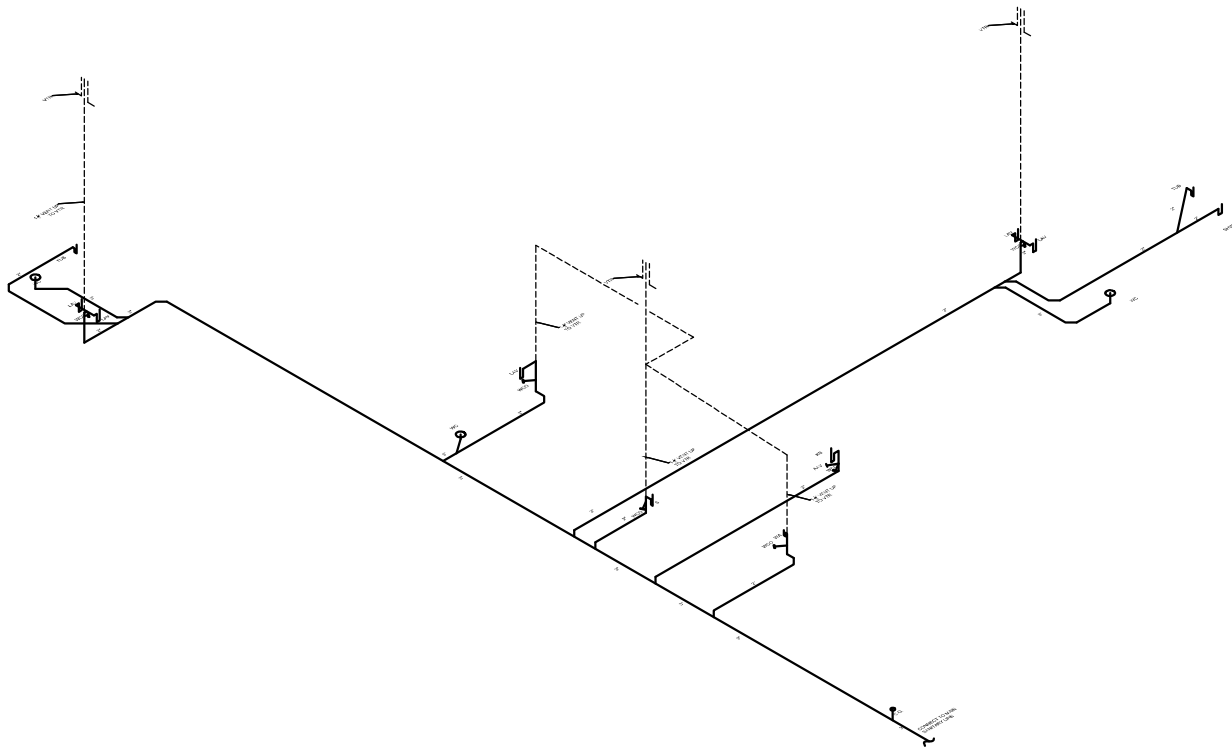

SANITARY RISER DIAGRAM

SCALE NTS

Bauen Consultants
ENGINEERING & ARCHITECTURE

CONTACT: 773-937-0712
ADDRESS: 128 DAV LN LONDON KY 40741

THIS DRAWING IS PROVIDED AS AN INSTRUMENT OF SERVICE BY THE ARCHITECT AND IS INTENDED FOR USE ON THIS PROJECT ONLY. THE DRAWING REMAINS THE PROPERTY OF THE ARCHITECT AND SHALL BE RETURNED TO HIM/HER UPON COMPLETION OF THE CONSTRUCTION WORK. PURSUANT TO THE ARCHITECTURAL WORKS COPYRIGHT PROTECTION ACT OF 1990, ALL DRAWINGS, SPECIFICATIONS, IDEAS, AND DESIGNS, INCLUDING THE OVERALL FORM, ARRANGEMENT, AND COMPOSITION OF THE SPACES, AND ELEMENTS APPEARING HEREIN, CONSTITUTES THE COPYRIGHT WORK OF THE ARCHITECT. ANY REPRODUCTION, USE, OR DISCLOSURE OF INFORMATION CONTAINED HEREIN WITHOUT PRIOR WRITTEN CONSENT OF THE ARCHITECT IS STRICTLY PROHIBITED.

- GENERAL PLAN NOTES**
- OWNER TO PERFORM THE FOLLOWING BEFORE CONSTRUCTION COMMENCES. DESIGNER ASSUMES NO LIABILITY FOR CONSTRUCTION:
1. BUILDER OR CONTRACTOR SHALL VERIFY ALL DIMENSIONS PRIOR TO PROCEEDING WITH CONSTRUCTION.
 2. BUILDER OR CONTRACTOR SHALL VERIFY COMPLIANCE WITH CITY AMENDMENTS TO **IRC**.
 3. DO NOT USE SCALED DIMENSIONS; USE ONLY DIMENSIONS AS CALLED OUT. WHEN NO DIMENSION IS PROVIDED, CONSULT WITH THE OWNER BEFORE PROCEEDING WITH WORK.
 4. CONTRACTOR SHALL VERIFY ALL EXISTING CONDITIONS, SITE UTILITY SERVICES AND DIMENSIONS AND NOTIFY ARCHITECT OF DISCREPANCIES THAT MAY AFFECT THE EXECUTION OF THE WORK BEFORE PROCEEDING.
 5. OMISSIONS OR CONFLICTS WITHIN THE DRAWINGS, NOTES OR DETAILS SHALL BE REPORTED THE OWNER BEFORE PROCEEDING WITH WORK.
 6. DETAILS TAKE PRECEDENCE DRAWING NOTES

REVISION SCHEDULE		
REV. #	NAME	DATE

PROPOSED ONE STORY FARM HOUSE

264 CROCKETT RD WEATHERFORD TX 76088

PLUMBING SANITARY FLOOR PLAN	
DATE	01.31.2025
PI01	
SCALE	AS INDICATED ON IIX17

GENERAL NOTES:

1. CONTRACTOR SHALL COORDINATE THE EFFORT WITH ALL TRADES.
2. PROVIDE A MINIMUM OF 4 INCH CLEARANCE AROUND DUCTWORK AND EQUIPMENT. ADJUST FRONT AND/OR MAINTENANCE SIDE CLEARANCES TO EQUIPMENT MANUFACTURER REQUIREMENTS. PROVIDE A MINIMUM OF 36 INCHES OF CLEARANCE AT ANY SIDE USED TO ACCESS ENERGIZED ELECTRICAL AND/OR CONTROL COMPONENTS.
3. ALL MECHANICAL SYSTEMS SHALL BE INSTALLED IN ACCORDANCE WITH ALL APPLICABLE SECTIONS OF THE NFPA STANDARDS, ANSI STANDARDS, THE LOCAL BUILDING CODE, LOCAL NOISE AND HEIGHT ORDINANCES, PLANS AND SPECIFICATIONS.
4. ALL MATERIALS SHALL BE NEW AND ALL WORKMANSHIP AND MATERIALS SHALL BE IN STRICT ACCORDANCE WITH APPLICABLE LOCAL CODES, PRODUCT APPROVAL, RULES AND ORDINANCES, ANY DAMAGED EQUIPMENT SHALL BE REPLACED OR RESTORED TO ORIGINAL CONDITION.
5. THE CONTRACTOR SHALL PROVIDE ALL LABOR, MATERIALS, EQUIPMENT, ACCESS PANELS, CONTROL SYSTEMS, DEVICES, PERMITS AND SERVICES NECESSARY FOR FURNISHING AND INSTALLING A COMPLETE OPERABLE MECHANICAL SYSTEM.
6. ALL LOUVERS, GRILLES, PIPING, ETC., SHALL BE PAINTED TO MATCH SURROUNDING COLOR AND TEXTURES AS REQUIRED BY ARCHITECT. VERIFY COLOR AND TEXTURE WITH ARCHITECT.
7. ALL CUTTING, PATCHING, STRUCTURAL STEEL, WEATHER PROOFING, PAINTING, AND WALL OPENINGS SHALL BE BY THE CONTRACTOR. ALL MODIFICATIONS TO THE EXISTING BUILDING STRUCTURE SHALL BE APPROVED BY THE OWNER OR HIS AUTHORIZED REPRESENTATIVE.
8. ALL OPENINGS IN BUILDING STRUCTURE, PIPING, ETC. TO BE 1/2" LARGER (ON ALL SIDES) THAN THE OUTSIDE DIMENSIONS. ALL FIRE RATED FLOOR AND WALL PENETRATIONS SHALL BE PROPERLY PROTECTED FROM FIRE, SMOKE AND WATER PENETRATION BY FILLING VOIDS BETWEEN PIPE AND WALL/FLOOR SLEEVES WITH UL APPROVED FIRE/SMOKE/WATER SEALANT.
9. NO COMBUSTIBLE MATERIAL IS ALLOWED IN MECHANICAL ROOMS OR IN CEILING/ATTIC SPACES.
10. ALL EXPOSED DUCTWORK, PIPING, ETC. SHALL BE FINISHED AND PAINTED AS REQUIRED BY ARCHITECT. VERIFY COLOR AND TEXTURE WITH ARCHITECT.
11. PROVIDE 10' MINIMUM CLEARANCE BETWEEN OUTSIDE AIR INTAKE DEVICES OR OPENINGS AND EXHAUST DISCHARGE OPENINGS OR DEVICES AND PLUMBING VENTS.
12. PROVIDE 5 SETS OF SUBMITTALS ON ALL HVAC EQUIPMENT. SUBMITTALS SHALL HAVE A SUMMARY SHEET SHOWING ALL SCHEDULED INFORMATION.
13. CONTRACTOR SHALL WARRANTY ALL MECHANICAL SYSTEMS, DUCTWORK, THERMOSTATS, AND ALL OTHER EQUIPMENT, PARTS AND LABOR UNDER THESE DWGS AND SPECIFICATIONS FOR A PERIOD OF ONE (1) YEAR AFTER C.O. OF BUILDING. ANY REPAIRS REQUIRING SYSTEM SHUT DOWN WILL BE DONE DURING NON OPERATIONAL PERIODS. HVAC CONTRACTOR SHALL COORDINATE WITH ALL OTHER TRADES PRIOR TO BIDDING AND PURCHASING ANY EQUIPMENT.

EQUIPMENT NOTES:

1. ALL MECHANICAL EQUIPMENT SHALL BE AHRI AND UL LISTED WHERE APPLICABLE AND RATED FOR THE REQUIRED SERVICE, PRESSURES, TEMPERATURES, AND SHALL BE PROVIDED WITH ALL NECESSARY TRANSFORMERS, SEALS, VALVES, CONNECTIONS, ETC. TO FUNCTION PROPERLY.
2. PROVIDE VIBRATION ISOLATORS ON ALL MECHANICAL EQUIPMENT AS CALLED FOR IN THE SPECIFICATIONS. PROVIDE NEOPRENE VIBRATION ISOLATION PADS SERVING EQUIPMENT MOUNTED ON CONCRETE HOUSEKEEPING PADS.
3. PROVIDE FIRE DAMPERS AS REQUIRED BY CODE IN ALL DUCT PENETRATIONS THROUGH FIRE RATED WALLS.
4. TEST AND BALANCE ALL MECHANICAL EQUIPMENT AIR DEVICES, DAMPERS, DX-SPLIT SYSTEMS AND FANS RATES ETC., TO PROVIDE THE DESIGN QUANTITIES AS SHOWN ON THE PLANS OR SCHEDULES. PROVIDE T&B REPORT IN ACCORDANCE WITH THE AIR BALANCE COUNCIL STANDARDS. PROVIDE FINAL BALANCING FOR ALL SYSTEMS TO SATISFACTION OF OWNER. TEST AND BALANCE SHALL BE PERFORMED BY AN INDEPENDENT CONTRACTOR OR THE OWNER SHALL, AT THEIR DISCRETION, CONTRACT AN INDEPENDENT T&B FIRM TO PERFORM THE SYSTEM BALANCING.
5. THERMOSTAT AND HUMIDISTAT LOCATION SHALL BE APPROVED BY OWNER AND ARCHITECT BEFORE INSTALLATION. MATCH HEIGHT, TYPE AND STYLE OF EXISTING THERMOSTAT AND HUMIDISTAT (IF APPLICABLE).
6. CONDENSATE DRAIN PIPING, USE HARD DRAWN COPPER TO ASTM B 88, TYPE "L". SCH 40 PVC MAY ALSO BE AN APPROVED EQUIVALENT.
7. ALL PIPING AND DUCTWORK PENETRATIONS THRU WALLS, BEAMS, SLABS, ETC, SHALL BE SLEEVED AS REQUIRED AND COORDINATED WITH THE STRUCTURAL ENGINEER. REWORK BAR JOIST CROSS BRACING AND PROVIDE NECESSARY TRANSITIONS AS REQUIRED FOR DUCTWORK INSTALLATION.
8. ALL INSULATION WILL HAVE FIRE/SMOKE RATING LESS THAN 25/50.
9. ALL OUTDOOR EQUIPMENT SHALL COMPLY WITH LOCAL ZONING NOISE ORDINANCES. MIN. REQUIREMENT SHALL NOT EXCEED A NOISE LEVEL OF 65 DB AS MEASURED RADIALY 30 FT FROM THE EQUIPMENT IN ALL DIRECTIONS.
10. PROVIDE MOTOR STARTERS FOR ALL MOTOR DRIVEN EQUIPMENT.
11. PROVIDE ADJUSTABLE PULLEYS FOR ALL BELT DRIVEN HVAC EQUIPMENT.
12. PROVIDE FLEXIBLE DUCT CONNECTORS, RATED AS REQUIRED, TO CONNECT G90 SHEET METAL DUCTWORK TO THE HVAC EQUIPMENT.
13. PROVIDE DOOR UNDERCUTS FOR TRANSFER AIR AS SHOWN ON PLANS. DOOR UNDERCUTS SHALL BE THE COMPLETE WIDTH OF THE DOOR AT A HEIGHT NO LESS THAN 3/4" AFF.
14. PROVIDE A MINIMUM OF THREE SETS OF FILTERS. ONE SET OF FILTERS SHALL BE IN PLACE DURING CONSTRUCTION. ANOTHER NEW SET SHALL BE INSTALLED PRIOR TO TEST AND BALANCE. THE FINAL SET SHALL BE INSTALLED AT THE END OF ONE YEAR SERVICE PERIOD.
15. ALL BRANCH DUCTWORK (SUPPLY AND RETURN) SHALL HAVE MANUAL VOLUME DAMPERS WITH A 2" OFFSET LOCKABLE BRACKET TO CLEAR THE INSULATION THICKNESS.
16. ALL SUPPLY AND RETURN GRILLES AND DIFFUSERS SHALL HAVE OPPOSED BLADE DAMPERS IN THE NECK OF THE DEVICE.
17. NO HVAC EQUIPMENT SHALL BE USED DURING CONSTRUCTION FOR VENTILATION PURPOSES. ALL DUCTWORK, PRIOR TO AND AFTER INSTALLATION SHALL BE CLEANED FOR PROPER IAQ VIA STANDARD METHODS FOR DUCTWORK.

AIR DISTRIBUTION, DUCTWORK AND

ACCESSORIES NOTES:

1. REFER TO ARCHITECTURAL PLANS FOR CEILING AND WALL TYPES. ALL SUPPLY AIR DIFFUSERS AND REGISTERS MOUNTED ON THE EXPOSED G90 GALVANIZED STEEL DUCTWORK SHALL HAVE ALUMINUM FINISH TO MATCH THE DUCTWORK. ALL SUPPLY AIR DIFFUSERS IN AREAS HAVING DROP CEILING, TRANSFER AIR GRILLES AND RETURN AIR GRILLES SHALL HAVE WHITE FINISH SUBJECT TO ARCHITECT'S APPROVAL. ALL DIFFUSERS, REGISTERS AND GRILLES SHALL BE RATED FOR THE SPECIFIED TEMPERATURE AND PRESSURE AND AS REQUIRED BY THE CEILING SYSTEM RATING.
2. ALL AIR CONDITIONING DUCTWORK SHALL BE DESIGNED, FABRICATED AND INSTALLED IN ACCORDANCE WITH "SMACNA" HVAC DUCT CONSTRUCTION STANDARDS, METAL AND FLEXIBLE, 2ND EDITION 1995.
3. ALL SUPPLY AIR DUCTWORK SHALL BE FABRICATED FROM G90 GALVANIZED SHEET METAL DUCTWORK, EXTERNALLY WRAPPED WITH R-6 INSULATION. ALL OUTSIDE AIR AND VENTILATION DUCTWORK SHALL BE FABRICATED FROM G90 GALVANIZED SHEET METAL DUCTWORK. EXHAUST DUCTWORK SHALL BE ALUMINUM. DUCTWORK SHALL MEET NFPA 90A/90B AND INSTALLATION SHALL COMPLY WITH SMACNA AND FBC.
- A. WHERE INDICATED RECTANGULAR SUPPLY AND RETURN AIR DUCT
DESIGN PRESSURE = 2.0 INCH W.G. POSITIVE OR NEGATIVE
- B. WHERE INDICATED ROUND SUPPLY AND RETURN AIR DUCT
DESIGN PRESSURE = 4.0 INCH W.G. POSITIVE OR NEGATIVE
- C. WHERE INDICATED RECTANGULAR EXHAUST AIR DUCT
DESIGN PRESSURE = 1.0 INCH W.G. NEGATIVE
- D. WHERE INDICATED ROUND EXHAUST AIR DUCT
DESIGN PRESSURE = 2.0 INCH W.G. NEGATIVE
- E. WHERE INDICATED ROUND DUCT AND FITTINGS
ROUND DUCT SHALL BE SINGLE WALL, SPIRAL LOCK SEAM WITH STANDARD RIB AND FITTINGS SHALL BE SPOT OR TACK WELDED AND SEALED, LAP AND RIVETED/SCREWED AND SEALED, SOLID WELDED OR STANDING SEAM.
- F. FLEXIBLE AIR DUCT
FLEXIBLE DUCT SHALL BE UL 181, CLASS 1, ALUMINUM LAMINATE AND POLYESTER FILM WITH LATEX ADHESIVE SUPPORTED BY HELICALLY WOUND SPRING STEEL WIRE. MATCH INSULATION "R" VALUE WITH THAT OF FIBERGLASS DUCT WRAP.
4. PROVIDE ACCESS DOORS AS REQUIRED FOR ALL MECHANICAL EQUIPMENT TO SERVICE AND VISUALLY CHECK ROTATION OF FANS AND MOTORS, POSITION OF DAMPERS, REPLACE FIRE DAMPER LINKS, ADJUST OR REPLACE CONTROLS, ETC.
5. PROVIDE LONG SWEEP OR VANED ELBOWS IN ALL CASES, SPLITTER DAMPERS WHERE INDICATED ON DWGWS AND VOLUME CONTROL DAMPERS IN ALL BRANCH DUCTS OR DIFFUSER TAKE OFF CONNECTIONS.
6. ALL HVAC EQUIPMENT AND DUCTWORK SHALL BE PROTECTED FROM THE INTERIOR AND EXTERIOR ELEMENTS DURING CONSTRUCTION. DUCTWORK AND EQUIPMENT OPENINGS SHALL BE PROTECTED BY PLASTIC SHEATHING UNTIL FINAL CONNECTIONS ARE COMPLETED.

ABBREVIATIONS

AHU	AIR HANDLING UNIT
BTU	BRITISH THERMAL UNIT
CD	CONDENSATE DRAIN PIPE
CFM	CUBIC FEET PER MINUTE
EF	EXHAUST FAN
MAX	MAXIMUM
MD	MOTORIZED DAMPER
MIN	MINIMUM
NOT TO SCALE	NOT TO SCALE
O/A	OUTSIDE AIR
RA	RETURN AIR
T/A	TRANSFER AIR

Bauen Consultants
ENGINEERING & ARCHITECTURE

CONTACT: 773-937-0712
ADDRESS: 128 DAV LN LONDON KY 40741

THIS DRAWING IS PROVIDED AS AN INSTRUMENT OF SERVICE BY THE ARCHITECT AND IS INTENDED FOR USE ON THIS PROJECT ONLY. THE DRAWING REMAINS THE PROPERTY OF THE ARCHITECT AND SHALL BE RETURNED TO HIM/HER UPON COMPLETION OF THE CONSTRUCTION WORK. PURSUANT TO THE ARCHITECTURAL WORKS COPYRIGHT PROTECTION ACT OF 1990, ALL DRAWINGS, SPECIFICATIONS, IDEAS, AND DESIGNS, INCLUDING THE OVERALL FORM, ARRANGEMENT, AND COMPOSITION OF THE SPACES, AND ELEMENTS APPEARING HEREIN, CONSTITUTES THE COPYRIGHT WORK OF THE ARCHITECT. ANY REPRODUCTION, USE, OR DISCLOSURE OF INFORMATION CONTAINED HEREIN WITHOUT PRIOR WRITTEN CONSENT OF THE ARCHITECT IS STRICTLY PROHIBITED.

GENERAL PLAN NOTES

OWNER TO PERFORM THE FOLLOWING
BEFORE CONSTRUCTION COMMENCES,
DESIGNER ASSUMES NO LIABILITY FOR
CONSTRUCTION:

1. BUILDER OR CONTRACTOR SHALL VERIFY ALL DIMENSIONS PRIOR TO PROCEEDING WITH CONSTRUCTION.
2. BUILDER OR CONTRACTOR SHALL VERIFY COMPLIANCE WITH CITY AMENDMENTS TO **IRC**.
3. DO NOT USE SCALED DIMENSIONS; USE ONLY DIMENSIONS AS CALLED OUT. WHEN NO DIMENSION IS PROVIDED, CONSULT WITH THE OWNER BEFORE PROCEEDING WITH WORK.
4. CONTRACTOR SHALL VERIFY ALL EXISTING CONDITIONS, SITE UTILITY SERVICES AND DIMENSIONS AND NOTIFY ARCHITECT OF DISCREPANCIES THAT MAY AFFECT THE EXECUTION OF THE WORK BEFORE PROCEEDING.
5. OMISSIONS OR CONFLICTS WITHIN THE DRAWINGS, NOTES OR DETAILS SHALL BE REPORTED THE OWNER BEFORE PROCEEDING WITH WORK.
6. DETAILS TAKE PRECEDENCE DRAWING NOTES

REVISION SCHEDULE


REV. #	NAME	DATE

PROPOSED ONE STORY
FARM HOUSE

264 CROCKETT RD WEATHERFORD TX
76088

MECHANICAL NOTES

DATE	01.31.2025
M001	
SCALE	AS INDICATED ON I1x17

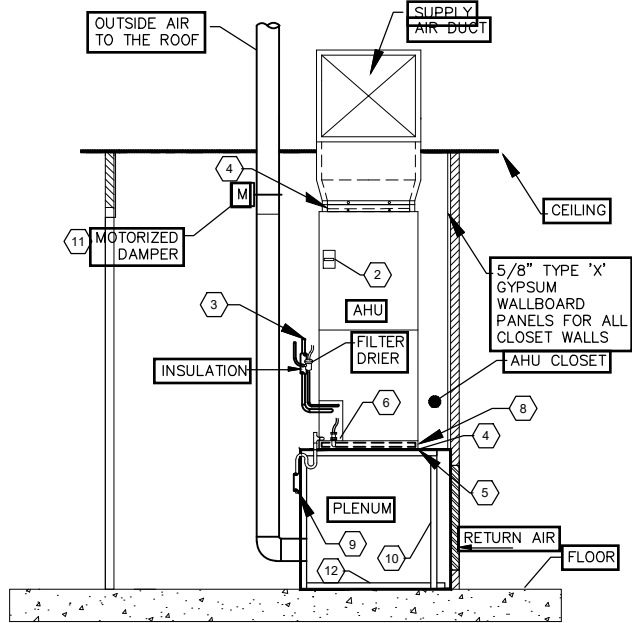


NOTES: #

1. ALL MATERIAL EXPOSED WITHIN PLENUMS SHALL BE NONCOMBUSTIBLE OR SHALL HAVE A FLAME SPREAD INDEX OF NOT MORE THAN 25 AND A SMOKE-DEVELOPED INDEX OF NOT MORE THAN 50 AS PER FMC 602.2.1..
2. DISCONNECT SWITCH. LOCATE SWITCH SUCH THAT OPERATING ARM IS NO HIGHER THAN 6'-0" AFF.
3. REFRIGERANT LINES. PROVIDE FILTER DRYER. PROVIDE INSULATION ON GAS LINE
4. MECHANICALLY ATTACH AHU TO SUPPLY DUCTWORK PER FMC R-M1601.6.3.2 AND R-M1601.3.6.
5. PROVIDE NEOPRENE STRIP ALONG THE PERIMETER OF AHU RESTING ON STAND.
6. FLOAT SWITCH. PROVIDE FLOAT SWITCH INTERLOCKED WITH BOTH THE AIR HANDLING UNIT AND THE OUTDOOR CONDENSING UNIT TO SHUTDOWN THE SYSTEM WHENEVER THE DRAIN PIPE IS CLOGGED. THE SYSTEM WILL NOT BE RESTARTED UNTIL MANUALLY RESET AFTER THE PAN AND DRAIN LINES ARE CLEANED BY A SERVICE TECHNICIAN.
7. PROVIDE FRONT ACCESS CLEARANCE AS PER MANUFACTURER RECOMMENDATIONS AND 4 INCH MINIMUM ALL OTHER SIDES AS PER FBC 13-610.1.ABC.3.0.3.
8. SHEET METAL FILTER RACK WITH HINGED ACCESS DOOR.
9. INSULATE CONDENSATE DRAIN. ROUTE IT OUTSIDE THE BUILDING & TERMINATE TO ANY APPROVED LOCATION.
10. MIAMI-TECH ALUMINUM AHU STAND MODEL AHE8.T.
- 11.MOTORIZED CONTROL DAMPER IN COMPLIANCE WITH FBC R-M1507.3.2. IT SHALL BE INSTALLED WITH AUTOMATIC CONTROLS CONFIGURED TO CLOSE WHEN THE SYSTEMS OR SPACES SERVED ARE NOT IN USE OR DURING UNOCCUPIED PERIOD WARM-UP AND SETBACK OPERATION. FBC R-M1507.3.2
12. DRIPPING PAN.

1 AIR HANDLING UNIT CONFIGURATION


NTS

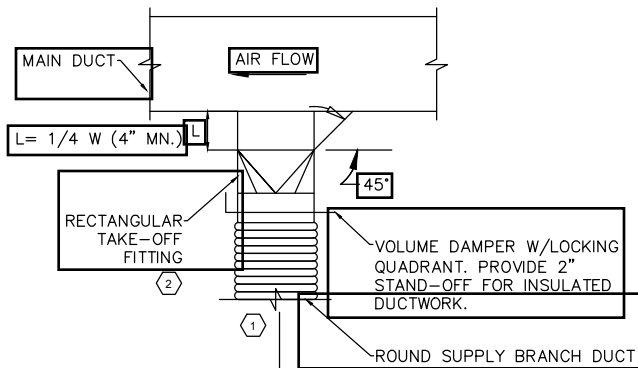

DETAIL NOTES: #

1. FLEXIBLE DUCT SIZE SAME AS DIFFUSER OR GRILLE NECK SIZE SERVED UNLESS NOTED OTHERWISE.
2. RECTANGULAR BRANCH TAKE-OFF SIZE IS THE SQUARE SIZE OF FLEXIBLE DUCT SIZE UNLESS NOTED OTHERWISE.
EXAMPLE: 10" ROUND FLEXIBLE DUCT WITH 10"X10" TAKE-OFF FITTING.

3 ROUND DUCT TAKE-OFF DETAIL

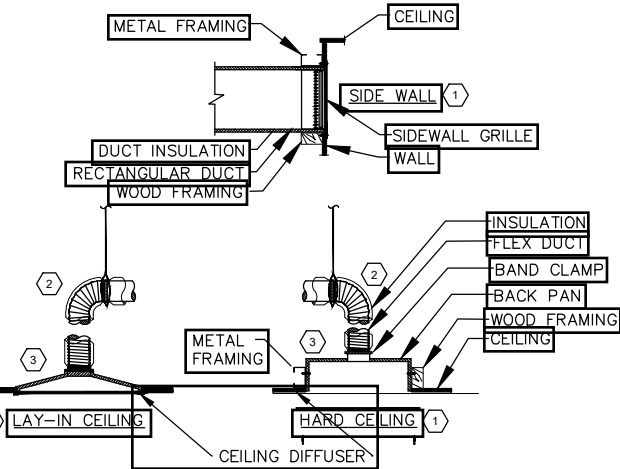


DETAIL NOTES: #

1. SEAL ALL JOINTS.
2. LIMIT FLEX DUCT TO 8 FEET MAX.
3. INSULATE BACK PANS OF CEILING DIFFUSERS.

6 SUPPLY AIR DEVICE DETAIL


NTS

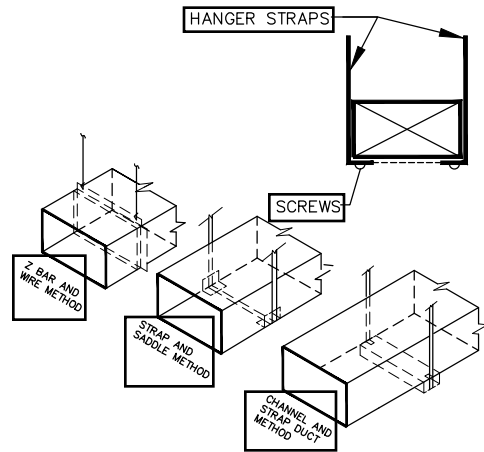

NOTE:


1. HANG DUCTS ACCORDING TO SMACNA STANDARDS.

4 DUCT HANGER DETAIL-LOWER ATTACHMENT

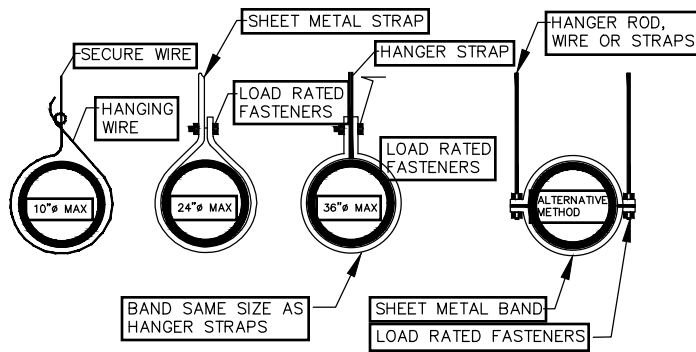

7 DUCT HANGER DETAIL-LOWER ATTACHMENT

NTS

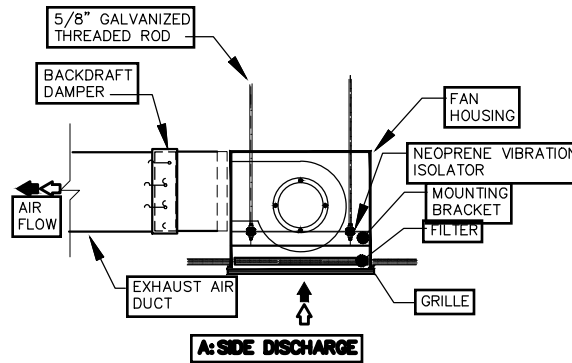


KEYED NOTE: #

1. RE: ARCHITECTURAL AND STRUCTURAL DWGS FOR DETAILS AND ATTACHMENTS TO STRUCTURE.
2. USE GALVANIZED SHEET METAL DUCT.


2 CEILING MOUNTED EXHAUST FAN DETAIL

NTS

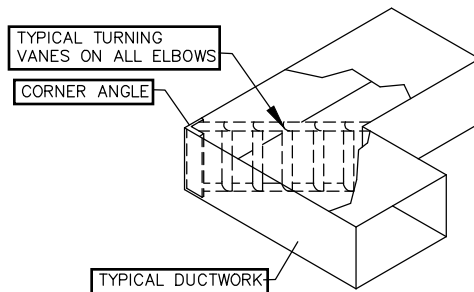

5 ELBOW WITH TURNING VANES DETAIL

NTS

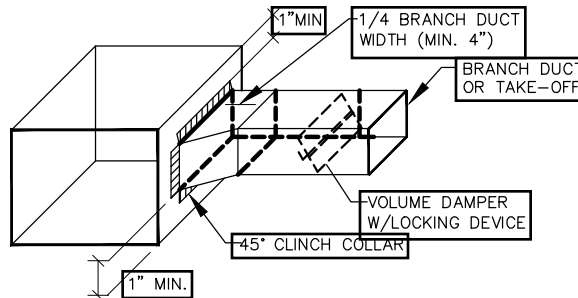

8 RECTANGULAR DUCT TAKE-OFF DETAIL

NTS

Bauen Consultants
ENGINEERING & ARCHITECTURE

CONTACT: 773-937-0712
ADDRESS: 128 DAV LN LONDON KY 40741

THIS DRAWING IS PROVIDED AS AN INSTRUMENT OF SERVICE BY THE ARCHITECT AND IS INTENDED FOR USE ON THIS PROJECT ONLY. THE DRAWING REMAINS THE PROPERTY OF THE ARCHITECT AND SHALL BE RETURNED TO HIM/HER UPON COMPLETION OF THE CONSTRUCTION WORK. PURSUANT TO THE ARCHITECTURAL WORKS COPYRIGHT PROTECTION ACT OF 1990, ALL DRAWINGS, SPECIFICATIONS, IDEAS, AND DESIGNS, INCLUDING THE OVERALL FORM, ARRANGEMENT, AND COMPOSITION OF THE SPACES, AND ELEMENTS APPEARING HEREIN, CONSTITUTES THE COPYRIGHT WORK OF THE ARCHITECT. ANY REPRODUCTION, USE, OR DISCLOSURE OF INFORMATION CONTAINED HEREIN WITHOUT PRIOR WRITTEN CONSENT OF THE ARCHITECT IS STRICTLY PROHIBITED.

GENERAL PLAN NOTES

OWNER TO PERFORM THE FOLLOWING BEFORE CONSTRUCTION COMMENCES. DESIGNER ASSUMES NO LIABILITY FOR CONSTRUCTION:

1. BUILDER OR CONTRACTOR SHALL VERIFY ALL DIMENSIONS PRIOR TO PROCEEDING WITH CONSTRUCTION.
2. BUILDER OR CONTRACTOR SHALL VERIFY COMPLIANCE WITH CITY AMENDMENTS TO IRC.
3. DO NOT USE SCALED DIMENSIONS; USE ONLY DIMENSIONS AS CALLED OUT. WHEN NO DIMENSION IS PROVIDED, CONSULT WITH THE OWNER BEFORE PROCEEDING WITH WORK.
4. CONTRACTOR SHALL VERIFY ALL EXISTING CONDITIONS, SITE UTILITY SERVICES AND DIMENSIONS AND NOTIFY ARCHITECT OF DISCREPANCIES THAT MAY AFFECT THE EXECUTION OF THE WORK BEFORE PROCEEDING.
5. OMISSIONS OR CONFLICTS WITHIN THE DRAWINGS, NOTES OR DETAILS SHALL BE REPORTED THE OWNER BEFORE PROCEEDING WITH WORK.
6. DETAILS TAKE PRECEDENCE DRAWING NOTES

REVISION SCHEDULE

REV. #	NAME	DATE

PROPOSED ONE STORY FARM HOUSE


264 CROCKETT RD WEATHERFORD TX 76088

MECHANICAL DETAILS

DATE 01.31.2025

M002

SCALE AS INDICATED ON IIX17

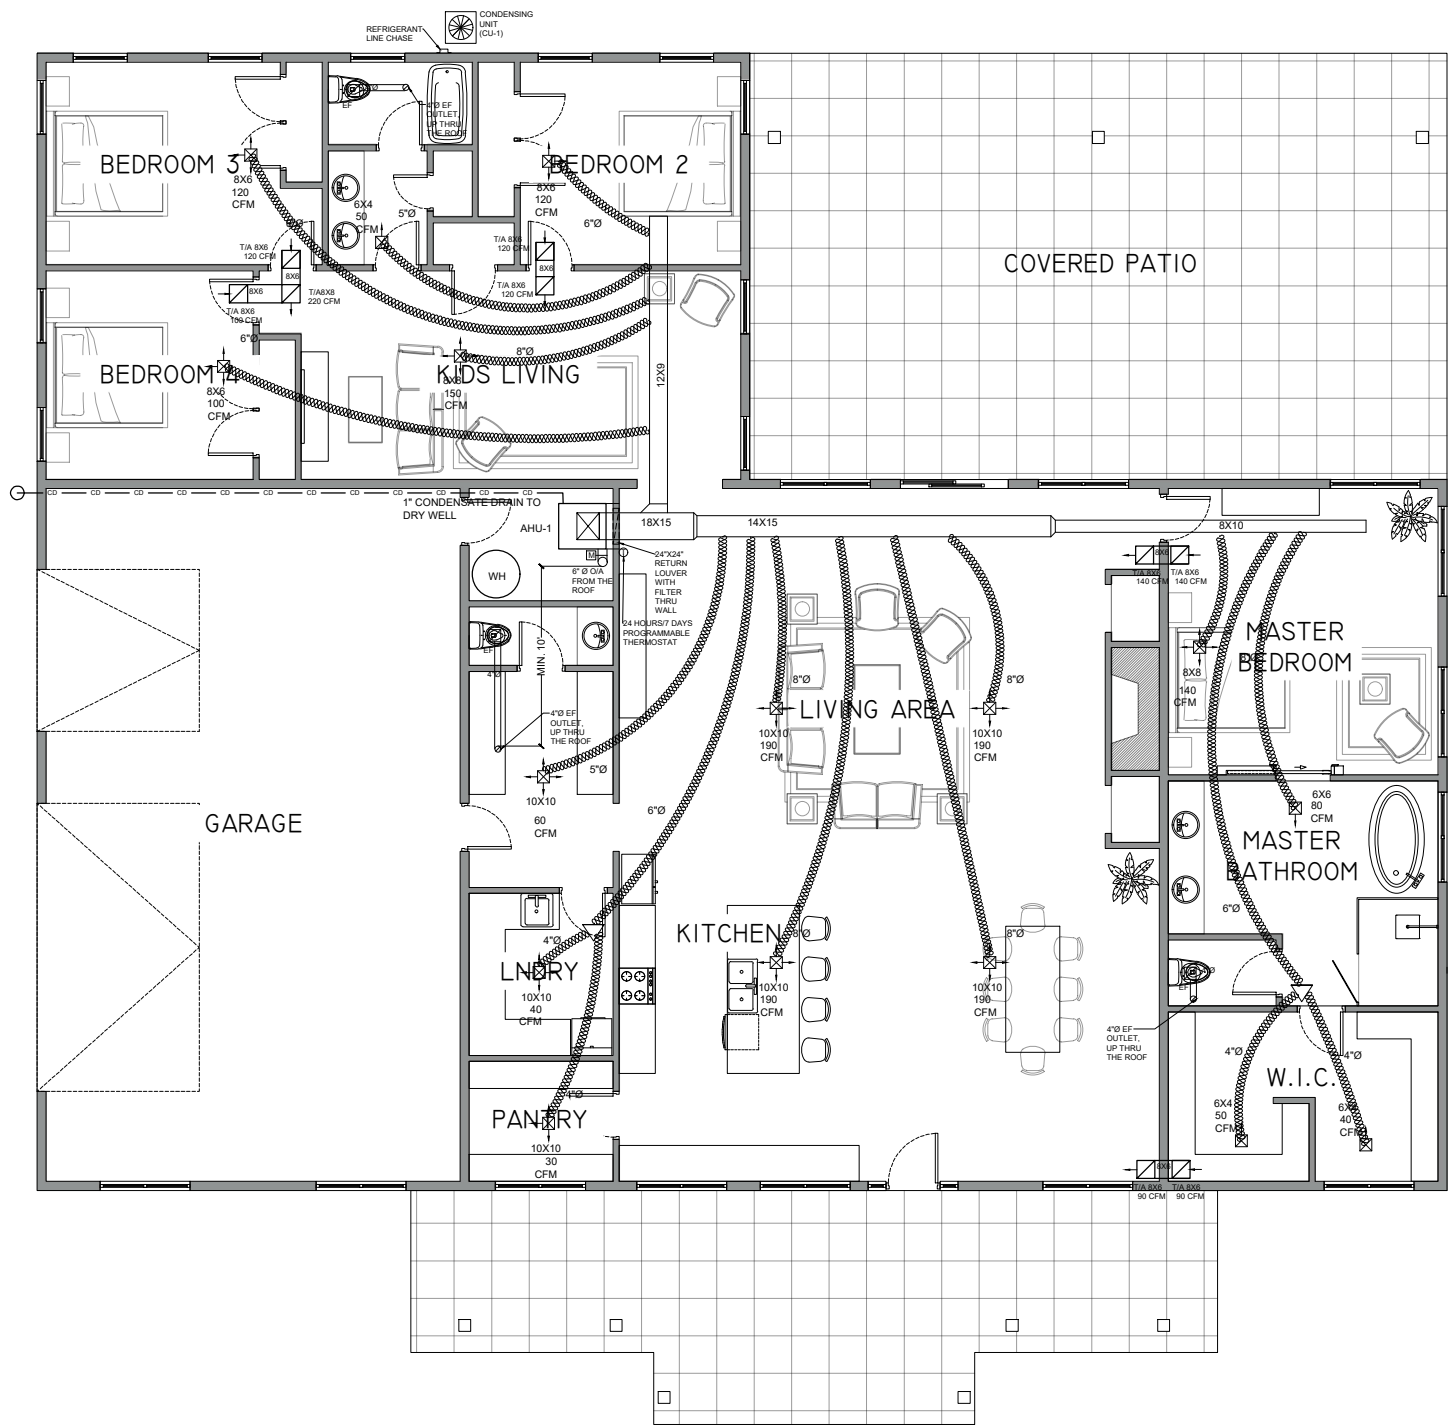

MECHANICAL FLOOR PLAN
SCALE 3/32"=1'-0"

Bauen Consultants
ENGINEERING & ARCHITECTURE

CONTACT: 773-937-0712
ADDRESS: 128 DAV LN LONDON KY 40741

THIS DRAWING IS PROVIDED AS AN INSTRUMENT OF SERVICE BY THE ARCHITECT AND IS INTENDED FOR USE ON THIS PROJECT ONLY. THE DRAWING REMAINS THE PROPERTY OF THE ARCHITECT AND SHALL BE RETURNED TO HIM/HER UPON COMPLETION OF THE CONSTRUCTION WORK. PURSUANT TO THE ARCHITECTURAL WORKS COPYRIGHT PROTECTION ACT OF 1990, ALL DRAWINGS, SPECIFICATIONS, IDEAS, AND DESIGNS, INCLUDING THE OVERALL FORM, ARRANGEMENT, AND COMPOSITION OF THE SPACES, AND ELEMENTS APPEARING HEREIN, CONSTITUTES THE COPYRIGHT WORK OF THE ARCHITECT. ANY REPRODUCTION, USE, OR DISCLOSURE OF INFORMATION CONTAINED HEREIN WITHOUT PRIOR WRITTEN CONSENT OF THE ARCHITECT IS STRICTLY PROHIBITED.

GENERAL PLAN NOTES

- OWNER TO PERFORM THE FOLLOWING BEFORE CONSTRUCTION COMMENCES. DESIGNER ASSUMES NO LIABILITY FOR CONSTRUCTION:
- BUILDER OR CONTRACTOR SHALL VERIFY ALL DIMENSIONS PRIOR TO PROCEEDING WITH CONSTRUCTION.
 - BUILDER OR CONTRACTOR SHALL VERIFY COMPLIANCE WITH CITY AMENDMENTS TO **IRC**.
 - DO NOT USE SCALED DIMENSIONS; USE ONLY DIMENSIONS AS CALLED OUT. WHEN NO DIMENSION IS PROVIDED, CONSULT WITH THE OWNER BEFORE PROCEEDING WITH WORK.
 - CONTRACTOR SHALL VERIFY ALL EXISTING CONDITIONS, SITE UTILITY SERVICES AND DIMENSIONS AND NOTIFY ARCHITECT OF DISCREPANCIES THAT MAY AFFECT THE EXECUTION OF THE WORK BEFORE PROCEEDING.
 - OMISSIONS OR CONFLICTS WITHIN THE DRAWINGS, NOTES OR DETAILS SHALL BE REPORTED THE OWNER BEFORE PROCEEDING WITH WORK.
 - DETAILS TAKE PRECEDENCE DRAWING NOTES

REVISION SCHEDULE		
REV. #	NAME	DATE

PROPOSED ONE STORY
FARM HOUSE

264 CROCKETT RD WEATHERFORD TX
76088

MECHANICAL FLOOR PLAN	
DATE	01.31.2025
MI01	
SCALE	AS INDICATED ON IIX17

FOUNDATION NOTES

1. CONC. MIX MINIMUM DESIGN STRENGTH 3500 PSI AT 28 DAYS
2. REINFORCING STEEL, BILLIT STEEL DEFORMED BARS, GRADE 60.
3. SEAL ALL VOIDS AROUND PENETRATIONS THRU FLOOR SLABS.
4. STEEL REBAR: ASTM A615 Gr 60. fy= 60 KSI
5. ANCHOR BOLTS A354 GrBD130 Fy= 130 Kip/in²
6. SLAB AND FOUNDATION SHALL BE LEVEL, SQUARE, AND SMOOTH UNLESS NOTED OTHERWISE.
7. VISQUEEN SHALL BE 6 MIL MINIMUM UNLESS NOTED OTHERWISE.

FIRE BLOCKING NOTES (IF APPLICABLE)

1. FIRE BLOCKING AT CONCEALED SPACES OF STUD WALLS AND PARTITIONS INCLUDING FURRED SPACES, AT THE CEILING FLOOR LEVELS AND AT 10 FOOT INTERVALS BOTH VERTICAL AND HORIZONTAL.
2. FIRE BLOCKING AT INTERCONNECTIONS BETWEEN CONCEALED VERTICAL AND HORIZONTAL SPACES SUCH AS SOFFITS, DROPPED CEILINGS, AND COVE CEILINGS.
3. FIRE BLOCKING IN CONCEALED SPACES BETWEEN STAR STRINGERS, AT THE TOP AND BOTTOM OF THE RUN AND BETWEEN STUDS ALONG AND IN LINE WITH THE RUN OF STAIRS, IF THE WALLS UNDER THE STAIRS ARE UNFINISHED.
4. FIRE BLOCKING IN OPENINGS AROUND VENTS, PIPES, DUCTS, CHIMNEYS, FIREPLACES, AND SIMILAR OPENINGS WHICH AFFORD A PASSAGE FOR FIRE AT CEILING AND FLOOR LEVELS, USE NON-COMBUSTIBLE MATERIALS.
5. FIRE BLOCKING AT OPENINGS BETWEEN ATTIC SPACES AND CHIMNEY CHASES FOR FACTORY-BUILT CHIMNEYS.
6. WALLS HAVING PARALLEL OR STAGGERED STUDS FOR SOUNDS CONTROL, SHALL HAVE FIRE BLOCKING OF MINERAL FIBER OR GLASS FIBER OR OTHER APPROVED NON-RIGID MATERIAL.
7. THE INTEGRITY OF ALL FIRE BLOCKING, AND DRAFT STOPS, SHALL BE MAINTAINED.

SOIL NOTES:

1. THE RESPONSIBLE CERTIFIED ENGINEER GEOLOGIST SHALL INSPECT AND APPROVE ALL AND EXCAVATIONS PRIOR TO PLACEMENT OF FORMS, REINFORCING STEEL OR CONCRETE. IN CASES INVOLVING CERTIFIED ENGINEERING FILL A SOIL ENGINEER SHALL PROVIDE THE INSPECTION AND APPROVAL.
2. IF THE BUILDING INSPECTOR SUSPECTS FILL, EXPANSIVE SOILS OR ANY GEOLOGIC INSTABILITY BASED UPON OBSERVATION OF THE FOUNDATION EXCAVATION, A SOILS OR GEOLOGICAL REPORT, AND RESUBMITTAL OF PLANS TO CHECK TO VERIFY THAT THE REPORT RECOMMENDATIONS HAVE BEEN INCORPORATED, MAY BE REQUIRED.

SPECIAL INSPECTION NOTES:

1. INSPECTION SHALL BE IN ACCORDANCE WITH 2012 IRC REQUIREMENTS FOR MASONRY, FOUNDATION, FIELD WELDING AND FRAMING WORK.
2. MATERIAL TESTING RESULTS AND/OR CERTIFICATIONS SHALL BE PROVIDED TO ARCHITECT FOR CONCRETE, STRUCTURAL STEEL AND FABRICATED FRAMING MEMBERS.
3. SPECIAL INSPECTION PER IRC STANDARD IS REQUIRED FOR THE FOLLOWING ITEMS:
 - ☐ POST-INSTALLED BOLTS IN CONCRETE
 - ☐ FIELD WELDING
 - ☐ MASONRY
 - ☐ CONCRETE MIX WITH f'c = 3000 PSI, OR GREATER
 - ☐ EPOXY ADHESIVES IN CONCRETE
4. THE SPECIAL INSPECTOR SHALL BE APPROVED BY THE BUILDING OFFICIAL PRIOR TO START OF WORK.

DESIGN DATA:

1. DESIGN LOADS:
 - A. ROOF DL = 20 psf
 - LL = 40 psf
 - SNOW = 5 psf
2. DESIGN CODE : IRC, 2018
3. SOILS ENGINEERING PARAMETERS: SOILD TYPE D (1,500 PSF)
4. WIND PARAMETERS:
 - Iw = 1.00
 - Speed: 106 MPH
 - Kz = 0.85
 - Kz = 0.85

ICF NOTES

FOOTING:

1. Getting the footing or slab as level as possible (preferably within +/- ¼") will minimize any adjustment needed on the first course.
2. It is the responsibility of the designer and/or end user to verify that structures built with CELBLOX® have been designed, engineered, and constructed in accordance with all applicable building codes and regulations.
3. Vertical dowels are inserted in the footing as specified to match vertical rebar spacing in the wall. If position is not shown on plan, consult the engineer or local building official, for correct placement. Dowels must extend vertically out of the footing to meet rebar overlap requirements (db*40).

LAYOUT GUIDLINES

4. Begin by snapping a chalk line where the outside of the CELBLOX® will sit on the footing.
5. Nailing 2"x2" lumber to the outside of the perimeter chalk line perpendicular to the sides of each corner will firmly locate where the corner CELBLOX® will sit. Make sure to remove this wood after the pour so it will not attract insects or create waterproofing issues later.
6. Alternately, a 2 ½" metal channel can be installed on the chalk line on the footing with a power nailer. When installing the first course, this channel will hold the **outside** panel of the block. For slab applications, the channel should be installed under the **inside** panel of the block to eliminate possible damage to the exterior edge of the slab.
7. Marking the location of your window and door openings on the footing will serve as a reminder of where to cut your forms as you build.

REBAR PLACEMENT.

8. Typical rebar overlaps are 40 times bar diameter on each end (db * 40) based on the diameter of the smaller bar (if two different bar sizes are used).
9. The first course horizontal rebar should be placed to the outside of the wall with the second course alternating to the inside. Rebar should continue to be alternated until the top of the wall is reached. This will ensure maximum wall strength in the wall. Typical horizontal placement is every 16" or as required by local code or engineering.

WINDOW & DOOR OPENINGS

10. Bucks are required to maintain correct opening size, to contain concrete during the pour, and to mount windows and doors in the structure.
11. All window and door bucks should be assembled prior to assembling the walls. Off-site assembly is preferable since it will increase on-site productivity and keep the jobsite clean. If you can't build them off-site, build them in an out-of-the-way location prior to assembling the walls.
12. Place your door bucks first. As soon as the foundation is cured, mark the location of all doors and secure the pre-built door bucks into place. The CELBLOX® ICF walls can then be started.
13. Once walls have reached the level of the bottom of the window, mark the height of the window bottom on the wall and cut the EPS down to window height with a hand saw.
14. Lift the window buck into place. Ensure the buck is level, adjusting if necessary, prior to fastening it into place. Place kickers to keep the bucks plumb. Once the bucks are in place, continue building until the top of the buck is reached.
15. All bucks must be supported properly before filling walls with concrete.

REINFORCEMENT NOTES

1. PROVIDE DETAILING, FABRICATION, AND INSTALLATION OF REINFORCING AND ACCESSORIES IN ACCORDANCE WITH ACI315 AND ACI 318.
2. PROVIDE STEEL REINFORCING BARS IN ACCORDANCE WITH ASTM A615, GRADE 60.
3. AND TIE SECURELY. PLACE WELDED WIRE FABRIC IN THE UPPER ONE-THIRD OF SLAB THICKNESS. WELDED WIRE FABRIC SHOULD BE DISCONTINUED AT ANY JOINTS. CONTRACTOR MUST ATTEND CLOSELY TO ESTABLISHING AND MAINTAINING ADEQUATE SUPPORT OF THE WELDED WIRE FABRIC REINFORCEMENT DURING THE CONCRETE PLACING OPERATIONS.
4. WELDED WIRE FABRIC REINFORCEMENT SHALL NOT BE LAID ON THE GROUND AND "PULLED UP" AFTER THE CONCRETE HAS BEEN PLACED, NOR SHOULD THE MATS BE "WALKED ON" AFTER PLACING THE CONCRETE. PROPER SUPPORT BAR PACING MUST BE PROVIDED FOR THE WELDED WIRE FABRIC REINFORCEMENT.
5. PROVIDE ANCHOR RODS CONFORMING TO THE STANDARDS OF ASTM F1554 GRADE 55 (WELDABLE) UNLESS OTHERWISE NOTED.
6. COORDINATE PLACEMENT OF CAST-IN-PLACE EMBEDS AND ANCHOR RODS. SET ANCHOR RODS WITH A TEMPLATE. SECURELY ATTACH EMBED ITEMS TO FORMWORK OR REINFORCING.
7. PROVIDE CLASS "B" REINFORCEMENT SPLICES FOR CONTINUOUS REINFORCEMENT. PROVIDE STANDARD 90-DEGREE HOOKS IN ACCORDANCE WITH ACI 318, UNLESS OTHERWISE NOTED. STAGGER SPLICES UNLESS SPECIFICALLY NOTED.
8. MAINTAIN THE FOLLOWING CONCRETE COVERAGE FOR REINFORCING STEEL UNLESS OTHERWISE NOTED:
 - 8.1. CONCRETE CAST AGAINST AND PERMANENTLY EXPOSED TO EARTH - 3 INCHES
 - 8.2. CONCRETE EXPOSED TO EARTH OR WEATHER
 - 8.2.1. NO. 6 AND LARGER - 2 INCHES
 - 8.2.2. NO. 5 AND SMALLER - 1-1/2 INCHES
 - 8.3. CONCRETE NOT EXPOSED TO WEATHER OR IN CONTACT WITH THE GROUND:
 - 8.3.1. SLABS AND WALLS
 - 8.3.2. NO. 14 AND NO. 18 - 1-1/2 INCHES
 - 8.3.3. NO. 11 AND SMALLER - 3/4 INCH
 - 8.4. BEAM STIRRUPS AND COLUMN TIES - 1-1/2 INCHES
9. DO NOT WELD OR BEND REINFORCEMENT IN THE FIELD UNLESS SPECIFICALLY SHOWN OR APPROVED BY STRUCTURAL ENGINEER.
10. WHEN SPECIFICALLY APPROVED, PROVIDE WELDED REINFORCEMENT IN ACCORDANCE WITH ASTM A 706. USE LOW HYDROGEN ELECTRODES FOR WELDING OF REINFORCEMENT IN CONFORMANCE WITH "WELDING REINFORCEMENT STEEL, METAL INSERTS AND CONNECTIONS IN REINFORCED CONCRETE CONSTRUCTION", AMERICAN WELDING SOCIETY,AWS D1.4.
11. WHERE REQUIRED, PROVIDE DOWELS TO MATCH SIZE AND SPACING OF MAIN REINFORCING.
12. PROVIDE CONTINUOUS HORIZONTAL WALL AND GRADE BEAM REINFORCEMENT WITH 90-DEGREE BENDS AND EXTENSIONS AT CORNERS AND INTERSECTIONS AS SHOWN ON TYPICAL BAR PLACING DETAILS.
13. PROVIDE BAR SUPPORT ACCESSORIES IN ACCORDANCE WITH THE LATEST ACI MANUAL OF STANDARD PRACTICE FOR DETAILING REINFORCED CONCRETE STRUCTURES. SUPPORT BEAM REINFORCING ON BEAM BOLSTERS SPACED NOT MORE THAN 4 FEET ON CENTER.
14. PROVIDE BAR SUPPORTS WITH PLASTIC COATED LEGS OR HOT DIP GALVANIZING AFTER FABRICATION FOR CONCRETE EXPOSED TO VIEW. PROVIDE STAINLESS STEEL BAR SUPPORTS FOR CONCRETE TO RECEIVE A SANDBLAST FINISH.

CONCRETE NOTES

1. PROVIDE CONCRETE AS SHOWN IN THE CONCRETE MATERIAL SCHEDULE BELOW. PROVIDE BATCH MIXING, TRANSPORTATION, PLACING AND CURING OF CONCRETE IN ACCORDANCE WITH RECOMMENDATIONS OF ACI 301, ACI 318 AND ASTM C94. USE TYPE I PORTLAND CEMENT UNLESS OTHERWISE NOTED. PROVIDE ADMIXTURES AND SPECIAL REQUIREMENTS AS SPECIFIED.
3. UNLESS SPECIFIED BELOW, CONCRETE MUST REACH THE FOLLOWING PERCENTAGES OF ITS 28 DAY COMPRESSIVE STRENGTH (F'c) BEFORE FORMS MAY BE REMOVED:
 - 3.1. WALLS, COLUMNS AND BEAM SIDES - 40 PERCENT
 - 3.2. BEAM BOTTOMS - 70 PERCENT
 - 3.3. SHORING FOR FLOOR SYSTEM - 85 PERCENT
 - 3.4. PROVIDE CONCRETE MIXES DESIGNED BY A QUALIFIED TESTING LABORATORY FOR REVIEW AND APPROVAL BY THE STRUCTURAL ENGINEER.
4. PROVIDE CONSTRUCTION AND CONTROL JOINTS AS INDICATED ON DRAWINGS. HORIZONTAL CONSTRUCTION JOINTS ARE NOT ALLOWED UNLESS SPECIFICALLY NOTED OR APPROVED BY STRUCTURAL ENGINEER. NOTIFY STRUCTURAL ENGINEER OF PROPOSED CONSTRUCTION JOINT OR CONTROL JOINT LOCATIONS WHICH ARE DIFFERENT OR IN ADDITION TO JOINTS INDICATED ON DRAWINGS.
5. PROVIDE 6,000-SQUARE FOOT MAXIMUM AREA OF CONCRETE PLACEMENT IN THE SLAB BETWEEN CONSTRUCTION JOINTS. PROVIDE 75-FOOT MAXIMUM SPACING OF CONSTRUCTION JOINTS IN GRADE BEAMS. PROVIDE GRADE BEAM CONSTRUCTION JOINTS IN MIDDLE 1/3 OF THE SPAN.
6. CHAMFER EXPOSED EDGES 3/4 INCH UNLESS OTHERWISE NOTED.
7. WIRE BRUSH AND CLEAN CONSTRUCTION JOINTS PRIOR TO POURING NEW CONCRETE.
8. REFERENCE THE APPROPRIATE DISCIPLINE'S DRAWINGS FOR SUB SLAB PIPING, FLOOR DRAINS, AND SLAB AND WALL PENETRATIONS.
9. THE GENERAL CONTRACTOR MUST COORDINATE EMBEDS AND ANCHORAGES WITH OTHER
10. APPROPRIATE CONTRACTORS FOR WORKS TO BE ATTACHED OR ANCHORED TO CAST-IN-PLACE STRUCTURES.
11. IN LOCATIONS WHERE NEW CONCRETE IS CAST AGAINST EXISTING CONCRETE OF MORE THAN 12.28 DAYS OF AGE, THE EXISTING CONCRETE MUST BE ROUGHENED TO 1/4" AMPLITUDE AND 13. THOROUGHLY CLEANED OF ANY LAITANCE OR FOREIGN MATERIALS, THEN SATURATED WITH 14. ALL STANDING WATER MUST BE REMOVED PRIOR TO PLACEMENT OF NEW CONCRETE.
15. EVERY EFFORT MUST BE EXERCISED TO AVOID CRACKS IN CONCRETE WORK. IN THE EVENT 16. OF SHRINKAGE CRACKS, ETC. THE GENERAL CONTRACTOR MUST BE RESPONSIBLE TO 17. REPAIR THESE CRACKS WITH EPOXY GROUT.
18. TOPPING CONCRETE MUST BE WET CURED FOR A MINIMUM OF 7 DAYS AND THEN A CONCRETE 19. SEALER SHALL BE APPLIED PER THE SPECIFICATIONS.
20. PROVIDE ADEQUATE STRUCTURAL FRAMING AS APPROVED BY STRUCTURAL ENGINEER FOR
21. MECHANICAL OPENINGS THROUGH THE SLABS, WALLS, AND FLOOR DECK. OPENINGS WILL NOT BE PERMITTED THROUGH BEAMS UNLESS SPECIFICALLY DETAILED.
22. FOR PIPE INSTALLED HORIZONTALLY WITHIN SLAB, PROVIDE MAXIMUM OUTSIDE DIAMETER OF 30 PERCENT OF THE SLAB THICKNESS. PLACE CONDUIT OR PIPE BETWEEN THE TOP AND BOTTOM LAYERS OF REINFORCEMENT WITHIN THE CENTER THIRD OF THE SLAB. DO NOT SPACE CONDUITS OR PIPES CLOSER THAN THREE DIAMETERS OR WIDTHS ON CENTER.

Bauen Consultants
ENGINEERING & ARCHITECTURE

CONTACT: 773-937-0712
ADDRESS: 128 DAV LN LONDON KY 40741

THIS DRAWING IS PROVIDED AS AN INSTRUMENT OF SERVICE BY THE ARCHITECT AND IS INTENDED FOR USE ON THIS PROJECT ONLY. THE DRAWING REMAINS THE PROPERTY OF THE ARCHITECT AND SHALL BE RETURNED TO HIM/HER UPON COMPLETION OF THE CONSTRUCTION WORK. PURSUANT TO THE ARCHITECTURAL WORKS COPYRIGHT PROTECTION ACT OF 1990, ALL DRAWINGS, SPECIFICATIONS, IDEAS, AND DESIGNS, INCLUDING THE OVERALL FORM, ARRANGEMENT, AND COMPOSITION OF THE SPACES, AND ELEMENTS APPEARING HEREIN, CONSTITUTES THE COPYRIGHT WORK OF THE ARCHITECT. ANY REPRODUCTION, USE, OR DISCLOSURE OF INFORMATION CONTAINED HEREIN WITHOUT PRIOR WRITTEN CONSENT OF THE ARCHITECT IS STRICTLY PROHIBITED.

GENERAL PLAN NOTES

- OWNER TO PERFORM THE FOLLOWING BEFORE CONSTRUCTION COMMENCES. DESIGNER ASSUMES NO LIABILITY FOR CONSTRUCTION:
1. BUILDER OR CONTRACTOR SHALL VERIFY ALL DIMENSIONS PRIOR TO PROCEEDING WITH CONSTRUCTION.
 2. BUILDER OR CONTRACTOR SHALL VERIFY COMPLIANCE WITH CITY AMENDMENTS TO IRC.
 3. DO NOT USE SCALED DIMENSIONS; USE ONLY DIMENSIONS AS CALLED OUT. WHEN NO DIMENSION IS PROVIDED, CONSULT WITH THE OWNER BEFORE PROCEEDING WITH WORK.
 4. CONTRACTOR SHALL VERIFY ALL EXISTING CONDITIONS, SITE UTILITY SERVICES AND DIMENSIONS AND NOTIFY ARCHITECT OF DISCREPANCIES THAT MAY AFFECT THE EXECUTION OF THE WORK BEFORE PROCEEDING.
 5. OMISSIONS OR CONFLICTS WITHIN THE DRAWINGS, NOTES OR DETAILS SHALL BE REPORTED THE OWNER BEFORE PROCEEDING WITH WORK.
 6. DETAILS TAKE PRECEDENCE DRAWING NOTES


REVISION SCHEDULE		
REV. #	NAME	DATE

PROPOSED ONE STORY
FARM HOUSE

264 CROCKETT RD WEATHERFORD TX
76088

FOUNDATION NOTES

DATE	01.31.2025
S100	
SCALE	AS INDICATED ON I1X17

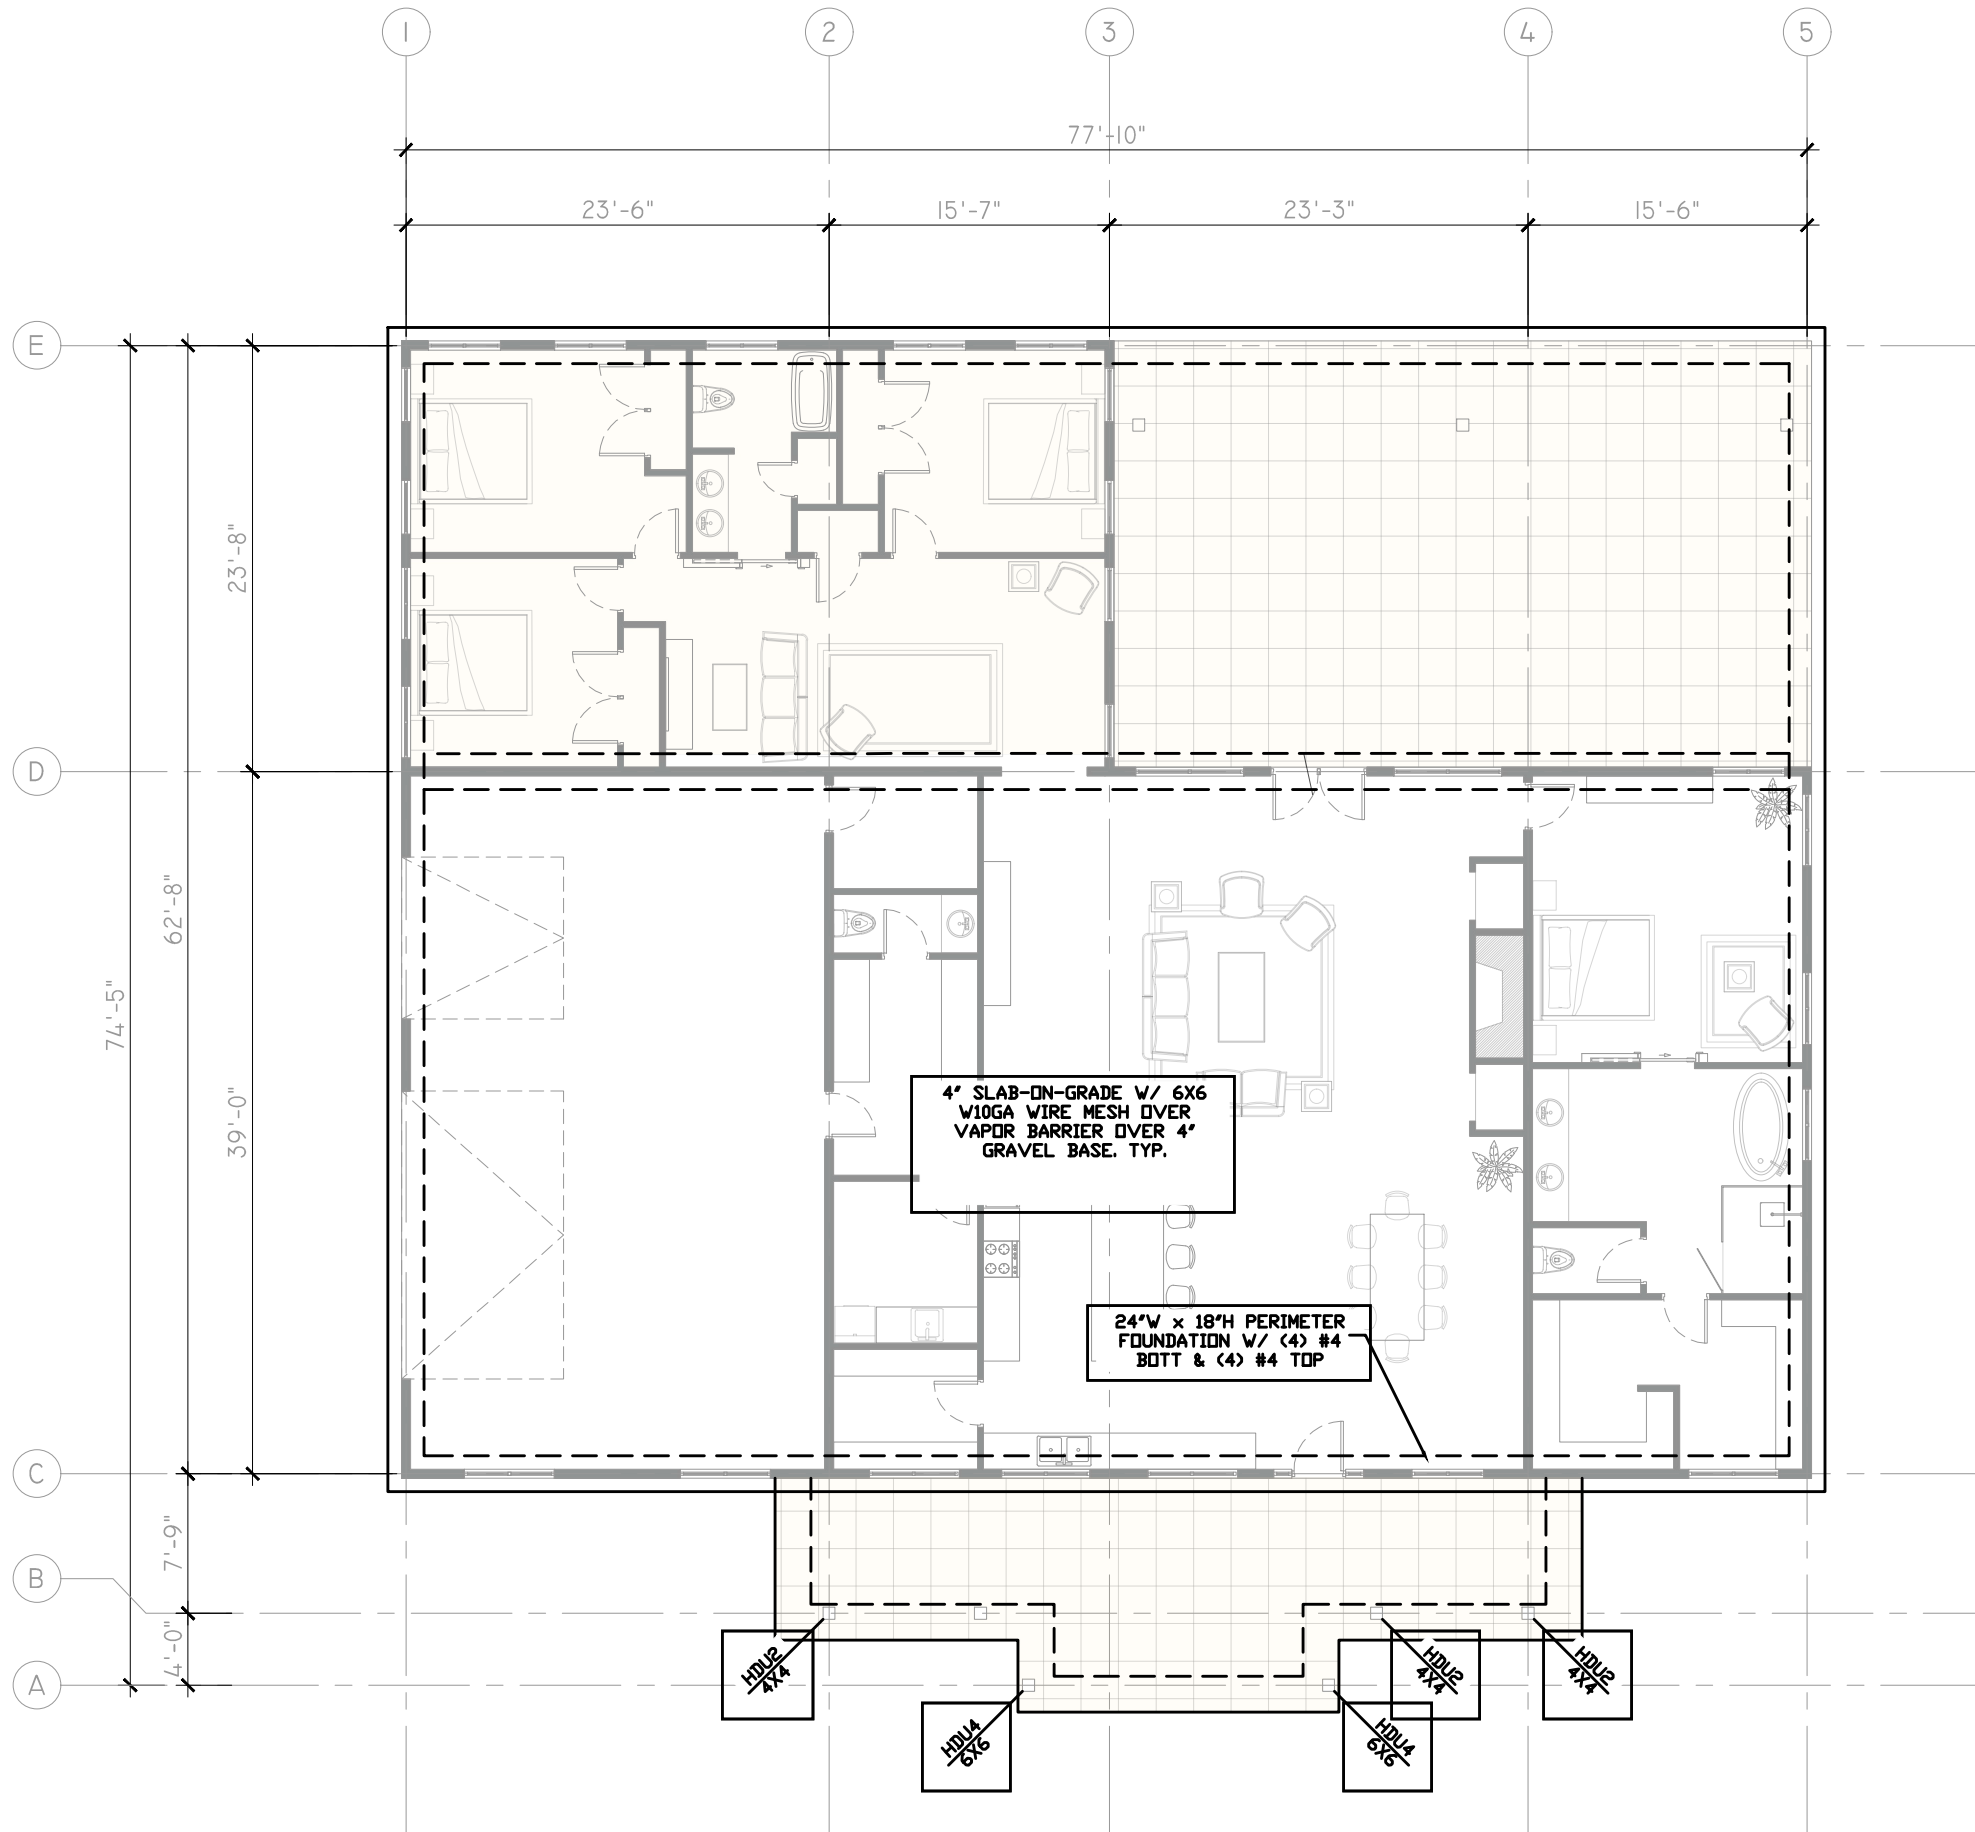

FOUNDATION PLAN

SCALE 3/32"=1'-0"

Bauen Consultants
ENGINEERING & ARCHITECTURE

CONTACT: 773-937-0712
ADDRESS: 128 DAV LN LONDON KY 40741

THIS DRAWING IS PROVIDED AS AN INSTRUMENT OF SERVICE BY THE ARCHITECT AND IS INTENDED FOR USE ON THIS PROJECT ONLY. THE DRAWING REMAINS THE PROPERTY OF THE ARCHITECT AND SHALL BE RETURNED TO HIM/HER UPON COMPLETION OF THE CONSTRUCTION WORK. PURSUANT TO THE ARCHITECTURAL WORKS COPYRIGHT PROTECTION ACT OF 1990, ALL DRAWINGS, SPECIFICATIONS, IDEAS, AND DESIGNS, INCLUDING THE OVERALL FORM, ARRANGEMENT, AND COMPOSITION OF THE SPACES, AND ELEMENTS APPEARING HEREIN, CONSTITUTE THE COPYRIGHT WORK OF THE ARCHITECT. ANY REPRODUCTION, USE, OR DISCLOSURE OF INFORMATION CONTAINED HEREIN WITHOUT PRIOR WRITTEN CONSENT OF THE ARCHITECT IS STRICTLY PROHIBITED.

- GENERAL PLAN NOTES**
- OWNER TO PERFORM THE FOLLOWING BEFORE CONSTRUCTION COMMENCES. DESIGNER ASSUMES NO LIABILITY FOR CONSTRUCTION:
- BUILDER OR CONTRACTOR SHALL VERIFY ALL DIMENSIONS PRIOR TO PROCEEDING WITH CONSTRUCTION.
 - BUILDER OR CONTRACTOR SHALL VERIFY COMPLIANCE WITH CITY AMENDMENTS TO IRC.
 - DO NOT USE SCALED DIMENSIONS; USE ONLY DIMENSIONS AS CALLED OUT. WHEN NO DIMENSION IS PROVIDED, CONSULT WITH THE OWNER BEFORE PROCEEDING WITH WORK.
 - CONTRACTOR SHALL VERIFY ALL EXISTING CONDITIONS, SITE UTILITY SERVICES AND DIMENSIONS AND NOTIFY ARCHITECT OF DISCREPANCIES THAT MAY AFFECT THE EXECUTION OF THE WORK BEFORE PROCEEDING.
 - OMISSIONS OR CONFLICTS WITHIN THE DRAWINGS, NOTES OR DETAILS SHALL BE REPORTED TO THE OWNER BEFORE PROCEEDING WITH WORK.
 - DETAILS TAKE PRECEDENCE DRAWING NOTES

REVISION SCHEDULE		
REV. #	NAME	DATE

PROPOSED ONE STORY FARM HOUSE


264 CROCKETT RD WEATHERFORD TX 76088

FOUNDATION PLAN


DATE 01.31.2025

S101


SCALE AS INDICATED ON I1X17

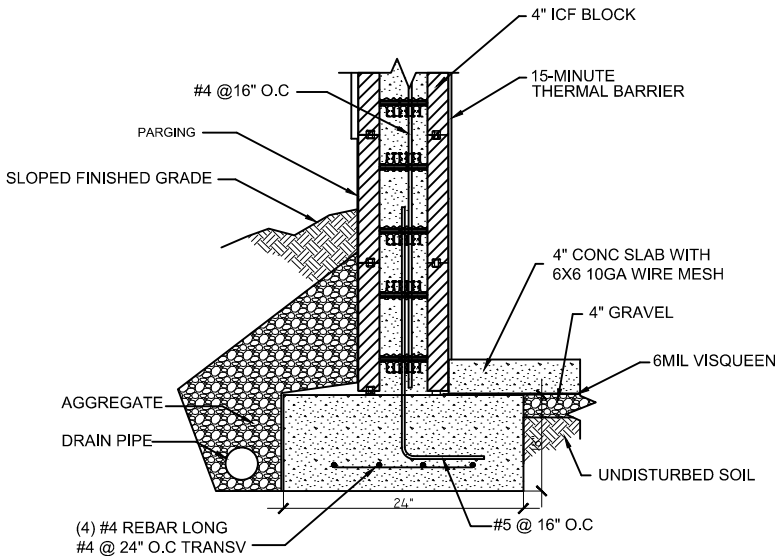


EXT FOUNDATION DETAIL
SCALE 1/2"=1'-0"

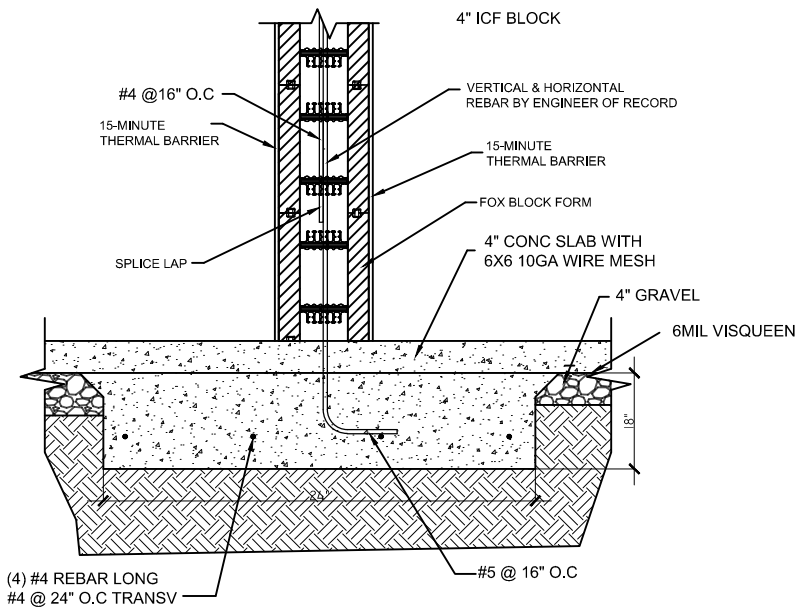

INT FOUNDATION DETAIL
SCALE 1/2"=1'-0"

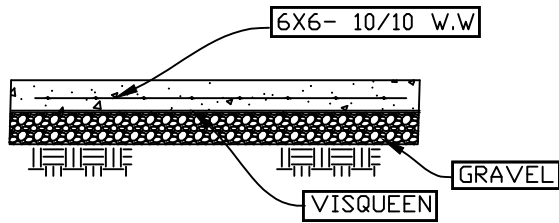

SLAB DETAIL
SCALE 1/2"=1'-0"

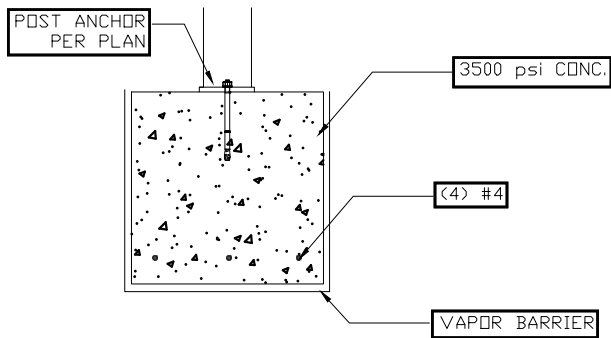

WOOD POST DETAIL
SCALE 1/2"=1'-0"

THIS DRAWING IS PROVIDED AS AN INSTRUMENT OF SERVICE BY THE ARCHITECT AND IS INTENDED FOR USE ON THIS PROJECT ONLY. THE DRAWING REMAINS THE PROPERTY OF THE ARCHITECT AND SHALL BE RETURNED TO HIM/HER UPON COMPLETION OF THE CONSTRUCTION WORK. PURSUANT TO THE ARCHITECTURAL WORKS COPYRIGHT PROTECTION ACT OF 1990, ALL DRAWINGS, SPECIFICATIONS, IDEAS, AND DESIGNS, INCLUDING THE OVERALL FORM, ARRANGEMENT, AND COMPOSITION OF THE SPACES, AND ELEMENTS APPEARING HEREIN, CONSTITUTES THE COPYRIGHT WORK OF THE ARCHITECT. ANY REPRODUCTION, USE, OR DISCLOSURE OF INFORMATION CONTAINED HEREIN WITHOUT PRIOR WRITTEN CONSENT OF THE ARCHITECT IS STRICTLY PROHIBITED.

GENERAL PLAN NOTES

OWNER TO PERFORM THE FOLLOWING BEFORE CONSTRUCTION COMMENCES. DESIGNER ASSUMES NO LIABILITY FOR CONSTRUCTION:

1. BUILDER OR CONTRACTOR SHALL VERIFY ALL DIMENSIONS PRIOR TO PROCEEDING WITH CONSTRUCTION.
2. BUILDER OR CONTRACTOR SHALL VERIFY COMPLIANCE WITH CITY AMENDMENTS TO IRC.
3. DO NOT USE SCALED DIMENSIONS; USE ONLY DIMENSIONS AS CALLED OUT. WHEN NO DIMENSION IS PROVIDED, CONSULT WITH THE OWNER BEFORE PROCEEDING WITH WORK.
4. CONTRACTOR SHALL VERIFY ALL EXISTING CONDITIONS, SITE UTILITY SERVICES AND DIMENSIONS AND NOTIFY ARCHITECT OF DISCREPANCIES THAT MAY AFFECT THE EXECUTION OF THE WORK BEFORE PROCEEDING.
5. OMISSIONS OR CONFLICTS WITHIN THE DRAWINGS, NOTES OR DETAILS SHALL BE REPORTED THE OWNER BEFORE PROCEEDING WITH WORK.
6. DETAILS TAKE PRECEDENCE DRAWING NOTES

REVISION SCHEDULE

REV. #	NAME	DATE

PROPOSED ONE STORY FARM HOUSE


264 CROCKETT RD WEATHERFORD TX 76088

FOUNDATION NOTES

DATE 01.31.2025

S100

SCALE AS INDICATED ON IXX7

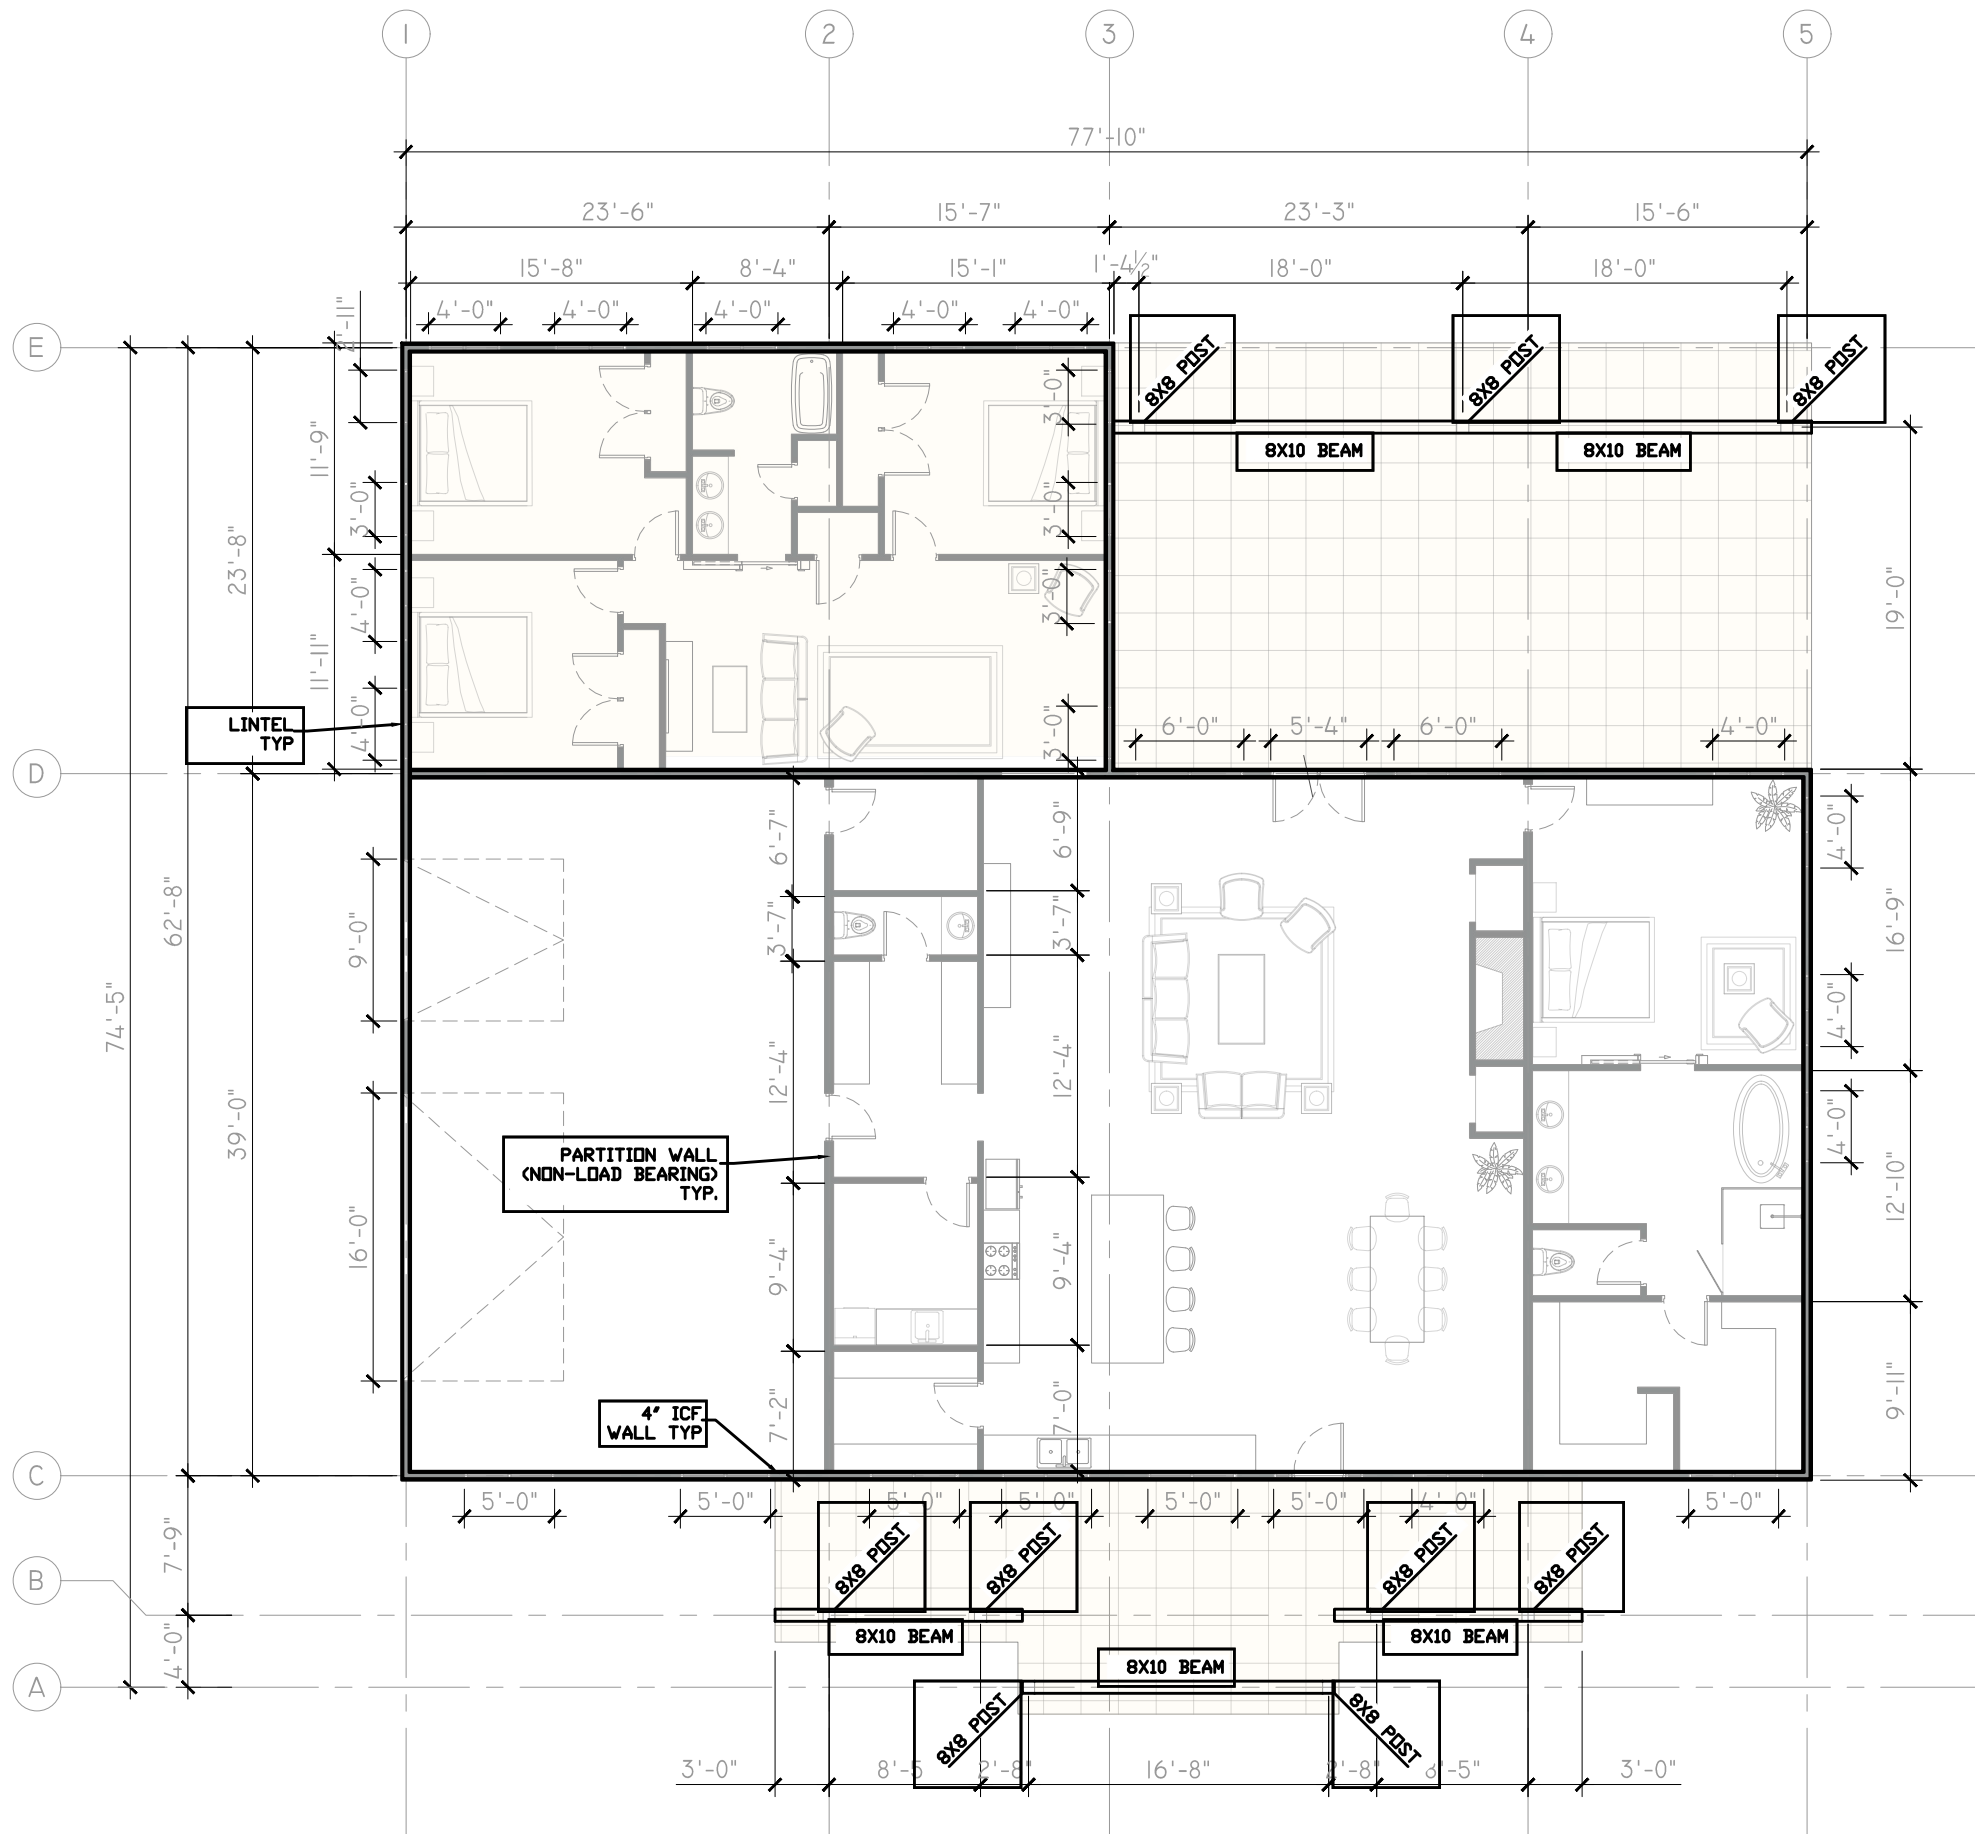

FRAMING PLAN

SCALE 3/32"=1'-0"

Bauen Consultants
ENGINEERING & ARCHITECTURE

CONTACT: 773-937-0712
ADDRESS: 128 DAV LN LONDON KY 40741

THIS DRAWING IS PROVIDED AS AN INSTRUMENT OF SERVICE BY THE ARCHITECT AND IS INTENDED FOR USE ON THIS PROJECT ONLY. THE DRAWING REMAINS THE PROPERTY OF THE ARCHITECT AND SHALL BE RETURNED TO HIM/HER UPON COMPLETION OF THE CONSTRUCTION WORK. PURSUANT TO THE ARCHITECTURAL WORKS COPYRIGHT PROTECTION ACT OF 1990, ALL DRAWINGS, SPECIFICATIONS, IDEAS, AND DESIGNS, INCLUDING THE OVERALL FORM, ARRANGEMENT, AND COMPOSITION OF THE SPACES, AND ELEMENTS APPEARING HEREIN, CONSTITUTES THE COPYRIGHT WORK OF THE ARCHITECT. ANY REPRODUCTION, USE, OR DISCLOSURE OF INFORMATION CONTAINED HEREIN WITHOUT PRIOR WRITTEN CONSENT OF THE ARCHITECT IS STRICTLY PROHIBITED.

GENERAL PLAN NOTES

OWNER TO PERFORM THE FOLLOWING BEFORE CONSTRUCTION COMMENCES. DESIGNER ASSUMES NO LIABILITY FOR CONSTRUCTION:

1. BUILDER OR CONTRACTOR SHALL VERIFY ALL DIMENSIONS PRIOR TO PROCEEDING WITH CONSTRUCTION.
2. BUILDER OR CONTRACTOR SHALL VERIFY COMPLIANCE WITH CITY AMENDMENTS TO IRC.
3. DO NOT USE SCALED DIMENSIONS; USE ONLY DIMENSIONS AS CALLED OUT. WHEN NO DIMENSION IS PROVIDED, CONSULT WITH THE OWNER BEFORE PROCEEDING WITH WORK.
4. CONTRACTOR SHALL VERIFY ALL EXISTING CONDITIONS, SITE UTILITY SERVICES AND DIMENSIONS AND NOTIFY ARCHITECT OF DISCREPANCIES THAT MAY AFFECT THE EXECUTION OF THE WORK BEFORE PROCEEDING.
5. OMISSIONS OR CONFLICTS WITHIN THE DRAWINGS, NOTES OR DETAILS SHALL BE REPORTED THE OWNER BEFORE PROCEEDING WITH WORK.
6. DETAILS TAKE PRECEDENCE DRAWING NOTES

REVISION SCHEDULE

REV. #	NAME	DATE

PROPOSED ONE STORY FARM HOUSE


264 CROCKETT RD WEATHERFORD TX 76088

FRAMING PLAN

DATE 01.31.2025

S200

SCALE AS INDICATED ON I1X17

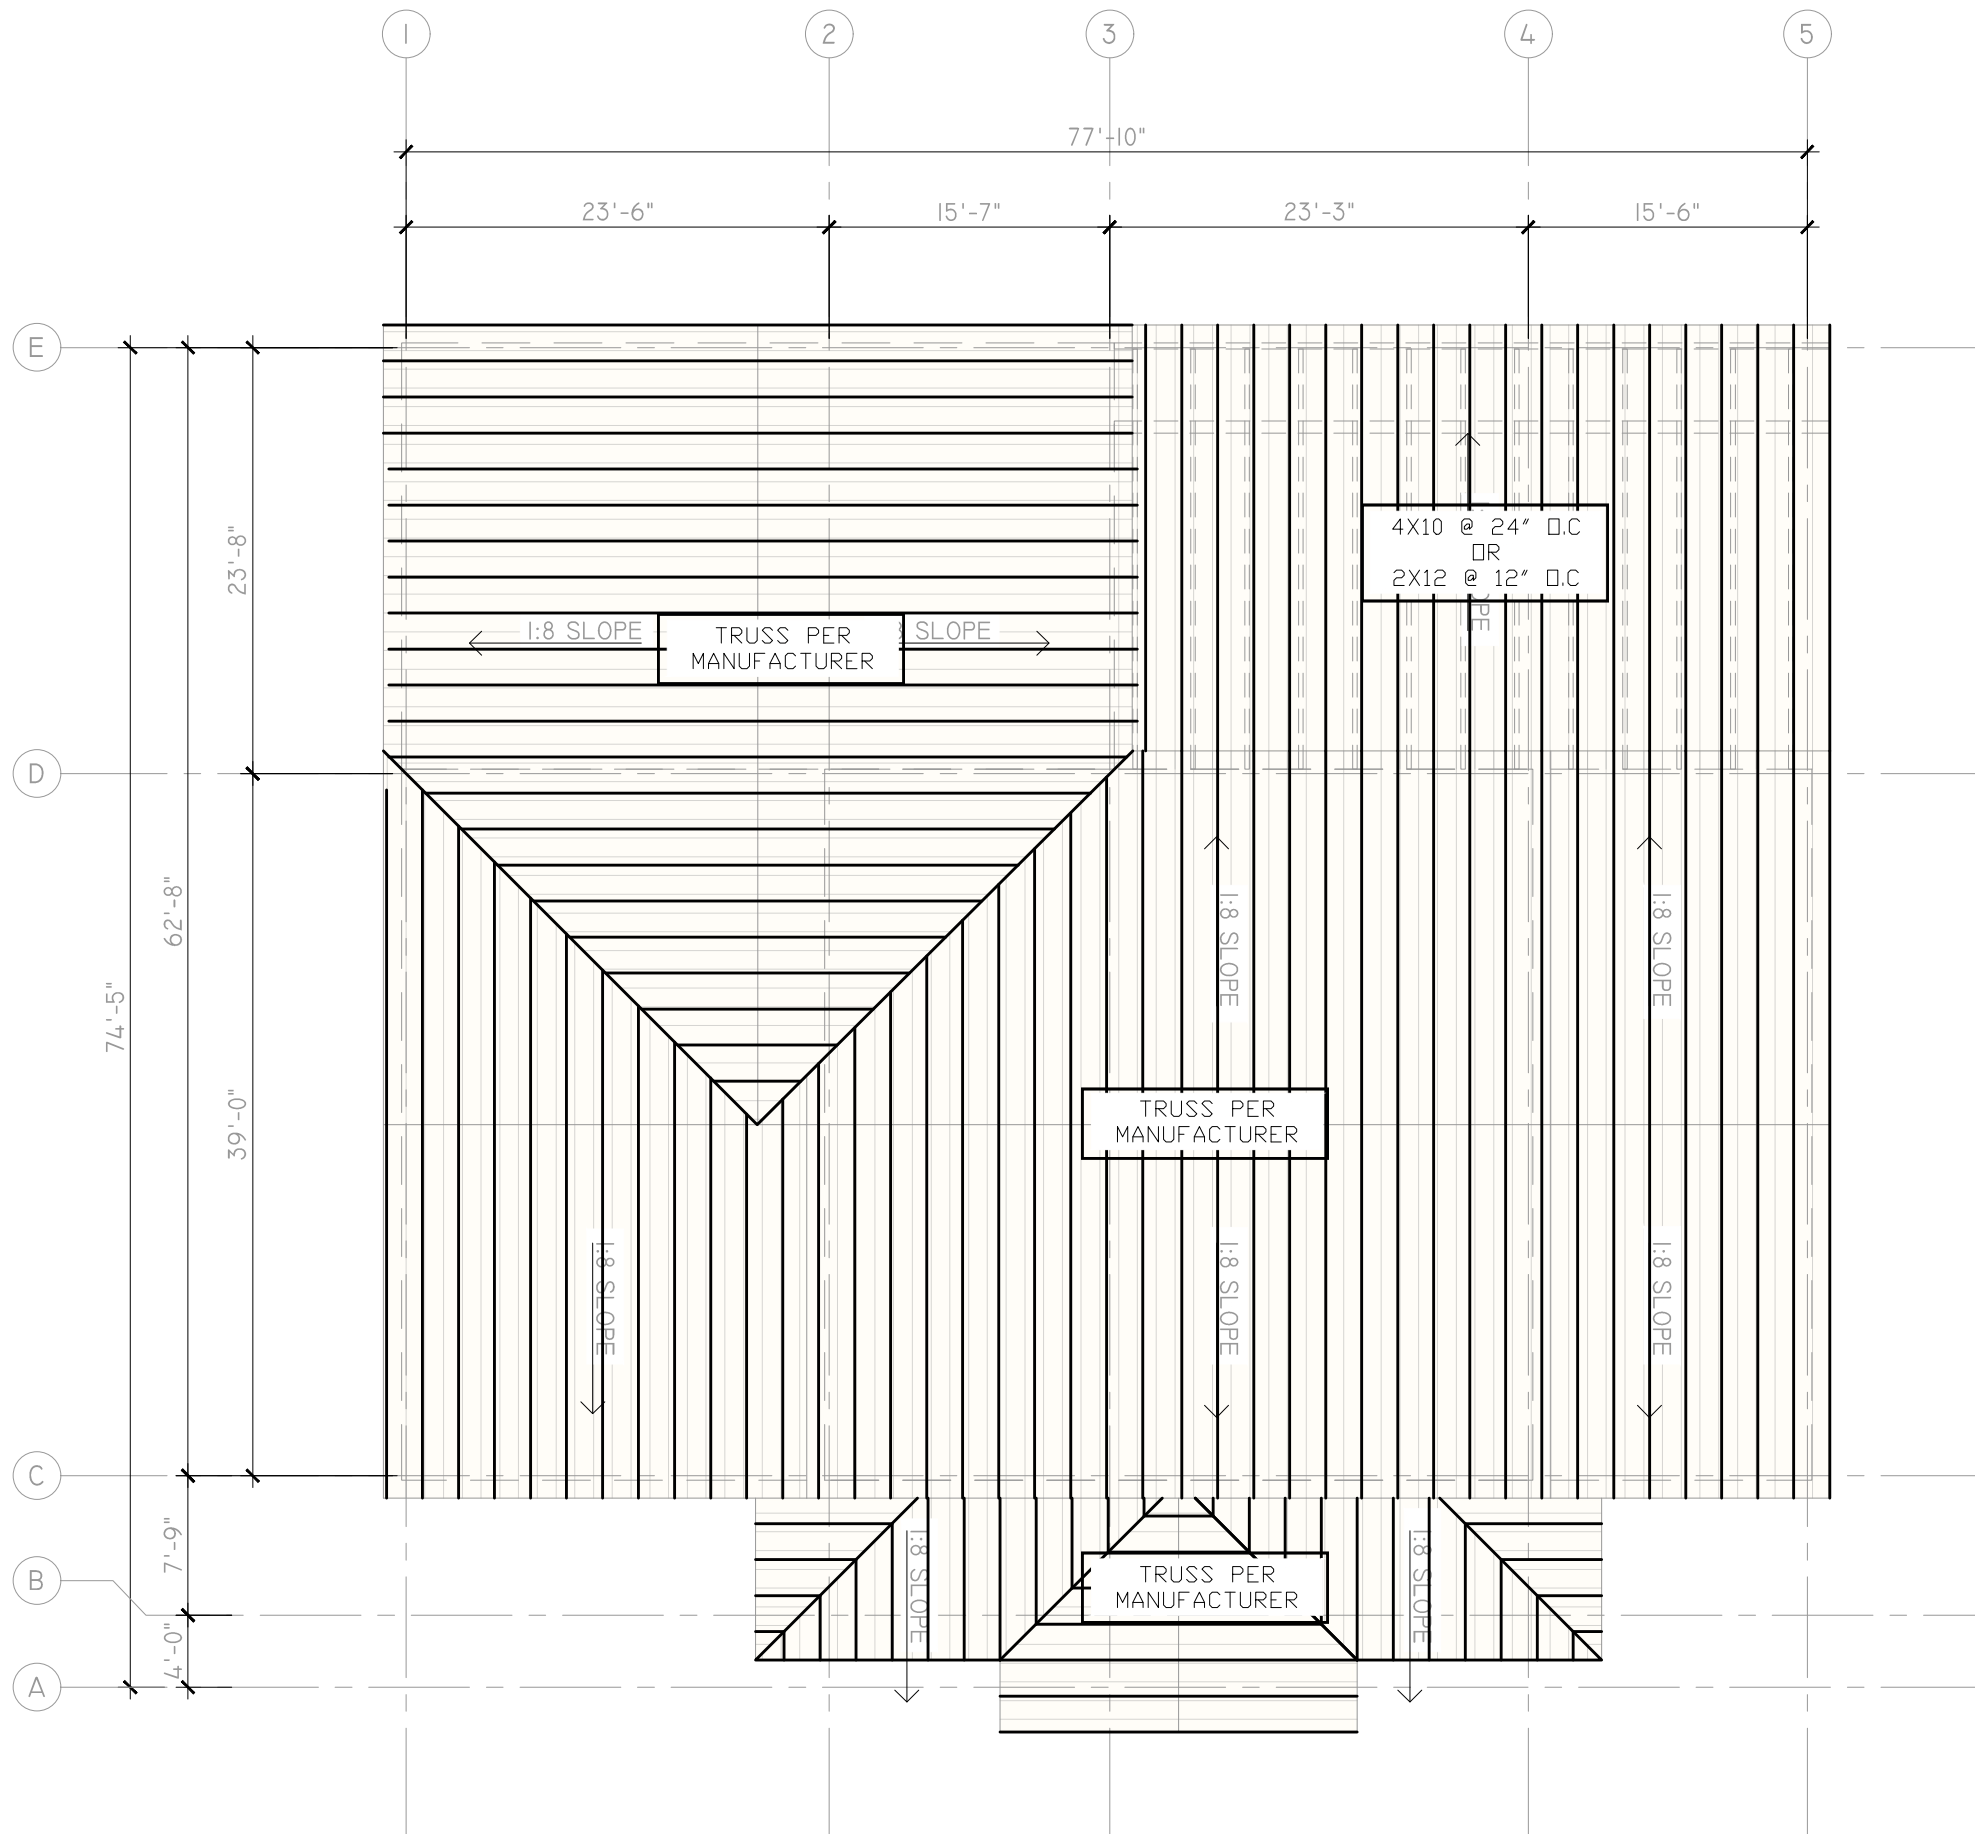

ROOF PLAN
SCALE 3/32"=1'-0"

Bauen Consultants
ENGINEERING & ARCHITECTURE

CONTACT: 773-937-0712
ADDRESS: 128 DAV LN LONDON KY 40741

THIS DRAWING IS PROVIDED AS AN INSTRUMENT OF SERVICE BY THE ARCHITECT AND IS INTENDED FOR USE ON THIS PROJECT ONLY. THE DRAWING REMAINS THE PROPERTY OF THE ARCHITECT AND SHALL BE RETURNED TO HIM/HER UPON COMPLETION OF THE CONSTRUCTION WORK. PURSUANT TO THE ARCHITECTURAL WORKS COPYRIGHT PROTECTION ACT OF 1990, ALL DRAWINGS, SPECIFICATIONS, IDEAS, AND DESIGNS, INCLUDING THE OVERALL FORM, ARRANGEMENT, AND COMPOSITION OF THE SPACES, AND ELEMENTS APPEARING HEREIN, CONSTITUTES THE COPYRIGHT WORK OF THE ARCHITECT. ANY REPRODUCTION, USE, OR DISCLOSURE OF INFORMATION CONTAINED HEREIN WITHOUT PRIOR WRITTEN CONSENT OF THE ARCHITECT IS STRICTLY PROHIBITED.


GENERAL PLAN NOTES

- OWNER TO PERFORM THE FOLLOWING BEFORE CONSTRUCTION COMMENCES. DESIGNER ASSUMES NO LIABILITY FOR CONSTRUCTION:
1. BUILDER OR CONTRACTOR SHALL VERIFY ALL DIMENSIONS PRIOR TO PROCEEDING WITH CONSTRUCTION.
 2. BUILDER OR CONTRACTOR SHALL VERIFY COMPLIANCE WITH CITY AMENDMENTS TO IRC.
 3. DO NOT USE SCALED DIMENSIONS; USE ONLY DIMENSIONS AS CALLED OUT. WHEN NO DIMENSION IS PROVIDED, CONSULT WITH THE OWNER BEFORE PROCEEDING WITH WORK.
 4. CONTRACTOR SHALL VERIFY ALL EXISTING CONDITIONS, SITE UTILITY SERVICES AND DIMENSIONS AND NOTIFY ARCHITECT OF DISCREPANCIES THAT MAY AFFECT THE EXECUTION OF THE WORK BEFORE PROCEEDING.
 5. OMISSIONS OR CONFLICTS WITHIN THE DRAWINGS, NOTES OR DETAILS SHALL BE REPORTED THE OWNER BEFORE PROCEEDING WITH WORK.
 6. DETAILS TAKE PRECEDENCE DRAWING NOTES


REVISION SCHEDULE		
REV. #	NAME	DATE

PROPOSED ONE STORY
FARM HOUSE
264 CROCKETT RD WEATHERFORD TX
76088



ROOF PLAN	
DATE	01.31.2025
S201	
SCALE	AS INDICATED ON IXX7

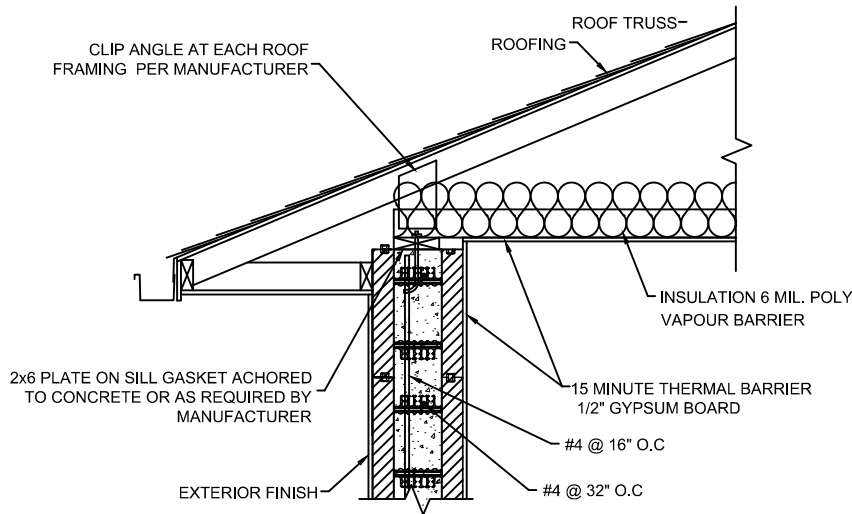


WALL TO ROOF DETAIL
SCALE NTS

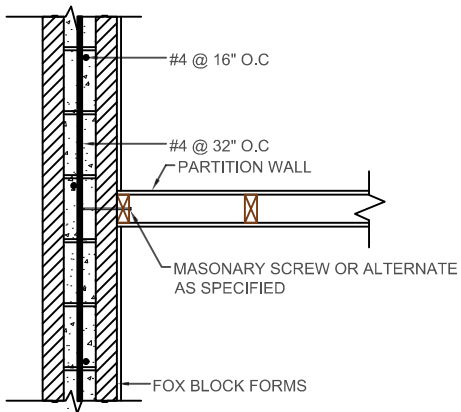

WALL TO ROOF DETAIL
SCALE NTS

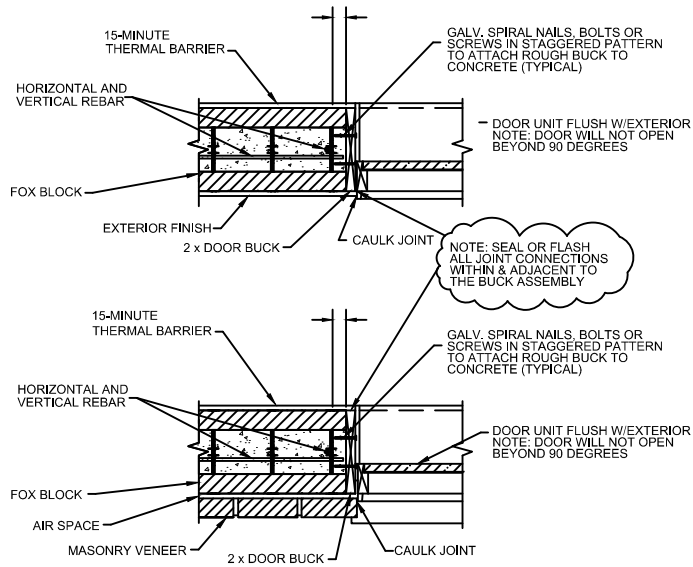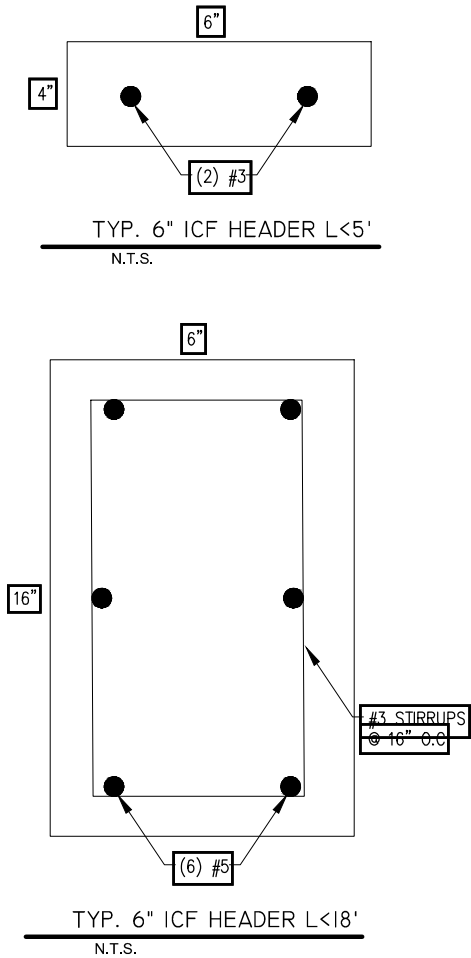

DOOR JAMB SECTION
SCALE NTS

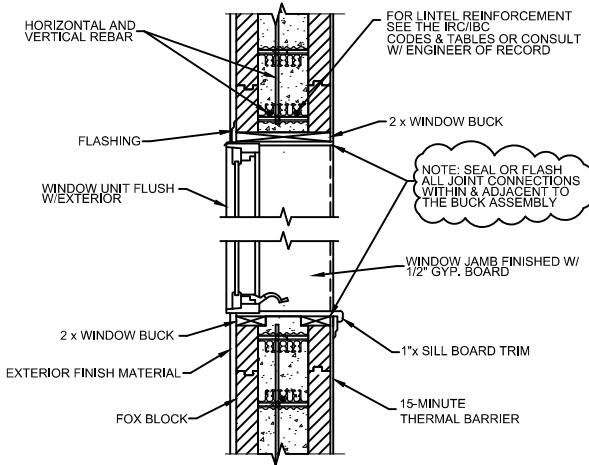

WINDOW HEAD/SILL DETAIL
SCALE NTS

Bauen Consultants
ENGINEERING & ARCHITECTURE

CONTACT: 773-937-0712
ADDRESS: 128 DAV LN LONDON KY 40741

THIS DRAWING IS PROVIDED AS AN INSTRUMENT OF SERVICE BY THE ARCHITECT AND IS INTENDED FOR USE ON THIS PROJECT ONLY. THE DRAWING REMAINS THE PROPERTY OF THE ARCHITECT AND SHALL BE RETURNED TO HIM/HER UPON COMPLETION OF THE CONSTRUCTION WORK. PURSUANT TO THE ARCHITECTURAL WORKS COPYRIGHT PROTECTION ACT OF 1990, ALL DRAWINGS, SPECIFICATIONS, IDEAS, AND DESIGNS, INCLUDING THE OVERALL FORM, ARRANGEMENT, AND COMPOSITION OF THE SPACES, AND ELEMENTS APPEARING HEREIN, CONSTITUTES THE COPYRIGHT WORK OF THE ARCHITECT. ANY REPRODUCTION, USE, OR DISCLOSURE OF INFORMATION CONTAINED HEREIN WITHOUT PRIOR WRITTEN CONSENT OF THE ARCHITECT IS STRICTLY PROHIBITED.

GENERAL PLAN NOTES

OWNER TO PERFORM THE FOLLOWING BEFORE CONSTRUCTION COMMENCES. DESIGNER ASSUMES NO LIABILITY FOR CONSTRUCTION:

1. BUILDER OR CONTRACTOR SHALL VERIFY ALL DIMENSIONS PRIOR TO PROCEEDING WITH CONSTRUCTION.
2. BUILDER OR CONTRACTOR SHALL VERIFY COMPLIANCE WITH CITY AMENDMENTS TO IRC.
3. DO NOT USE SCALED DIMENSIONS; USE ONLY DIMENSIONS AS CALLED OUT. WHEN NO DIMENSION IS PROVIDED, CONSULT WITH THE OWNER BEFORE PROCEEDING WITH WORK.
4. CONTRACTOR SHALL VERIFY ALL EXISTING CONDITIONS, SITE UTILITY SERVICES AND DIMENSIONS AND NOTIFY ARCHITECT OF DISCREPANCIES THAT MAY AFFECT THE EXECUTION OF THE WORK BEFORE PROCEEDING.
5. OMISSIONS OR CONFLICTS WITHIN THE DRAWINGS, NOTES OR DETAILS SHALL BE REPORTED THE OWNER BEFORE PROCEEDING WITH WORK.
6. DETAILS TAKE PRECEDENCE DRAWING NOTES

REVISION SCHEDULE

REV. #	NAME	DATE

PROPOSED ONE STORY FARM HOUSE

264 CROCKETT RD WEATHERFORD TX 76088

FRAMING DETAILS

DATE 01.31.2025

S202

SCALE AS INDICATED ON : IIX17