


Control, Grades, and Elevation:


1. All finished concrete surfaces shall be a minimum of 1 inch above the finished grade.

2. ICF Construction: Modular thin veneer, Grade SW ICF Construction, alternately stacked (unless noted otherwise).

3. Stucco: Control three coat with fine texture finish. Control joints according to elevations, 20' o.c. max.
 4. Tile: All exterior walls to be masonry.
 5. Place ladder type horizontal reinforcement at every other course.
 6. Mortar joints: all joints shall be a tuck point concave tool joint with a 3/8" width.
 7. Construction Joints: Vertical masonry movement joints to be 20' o.c. max, unless noted otherwise, and shall not cross lintels or ICF Construction shelf angles.
 8. Approval: Architect reserves the right to reject any work that does not satisfy the design intent.
 9. Cutting of masonry blocks: all cutting, trimming, or shaping shall be done by a motorized masonry saw. Breaking or splitting will not be accepted.
 10. Weep holes: Provide at 24" o.c. at the base of the masonry facade one course above the foundation and immediately above all other flashing.
 11. Flashing: Provide stainless steel flashing at the base of the masonry facade one course above the foundation. Provide flashing above all bond beams and openings.
 12. Sealant: All masonry surfaces to be coated with Behr Premium Waterproofing and Protector No. 980 or equivalent.
- Stud Walls:**
13. Wood Studs: All exterior wall and demising wall studs to be 2"x6" spaced at 16" on center. All other interior walls to be 2"x4" studs spaced at 16" on center. Refer to Structural Drawings for load bearing stud layout, sections, and details.
 14. Fasteners: All exterior stud screws and fasteners to be stainless steel with neoprene washers.
 15. Sheathing: All exterior sheathing used in Cavity Walls to be Wood Structural Panel (ex: OSB).
 16. Vapor Barrier: Vapor barrier used over sheathing to be wrapped above flashing at the base and above window locations.

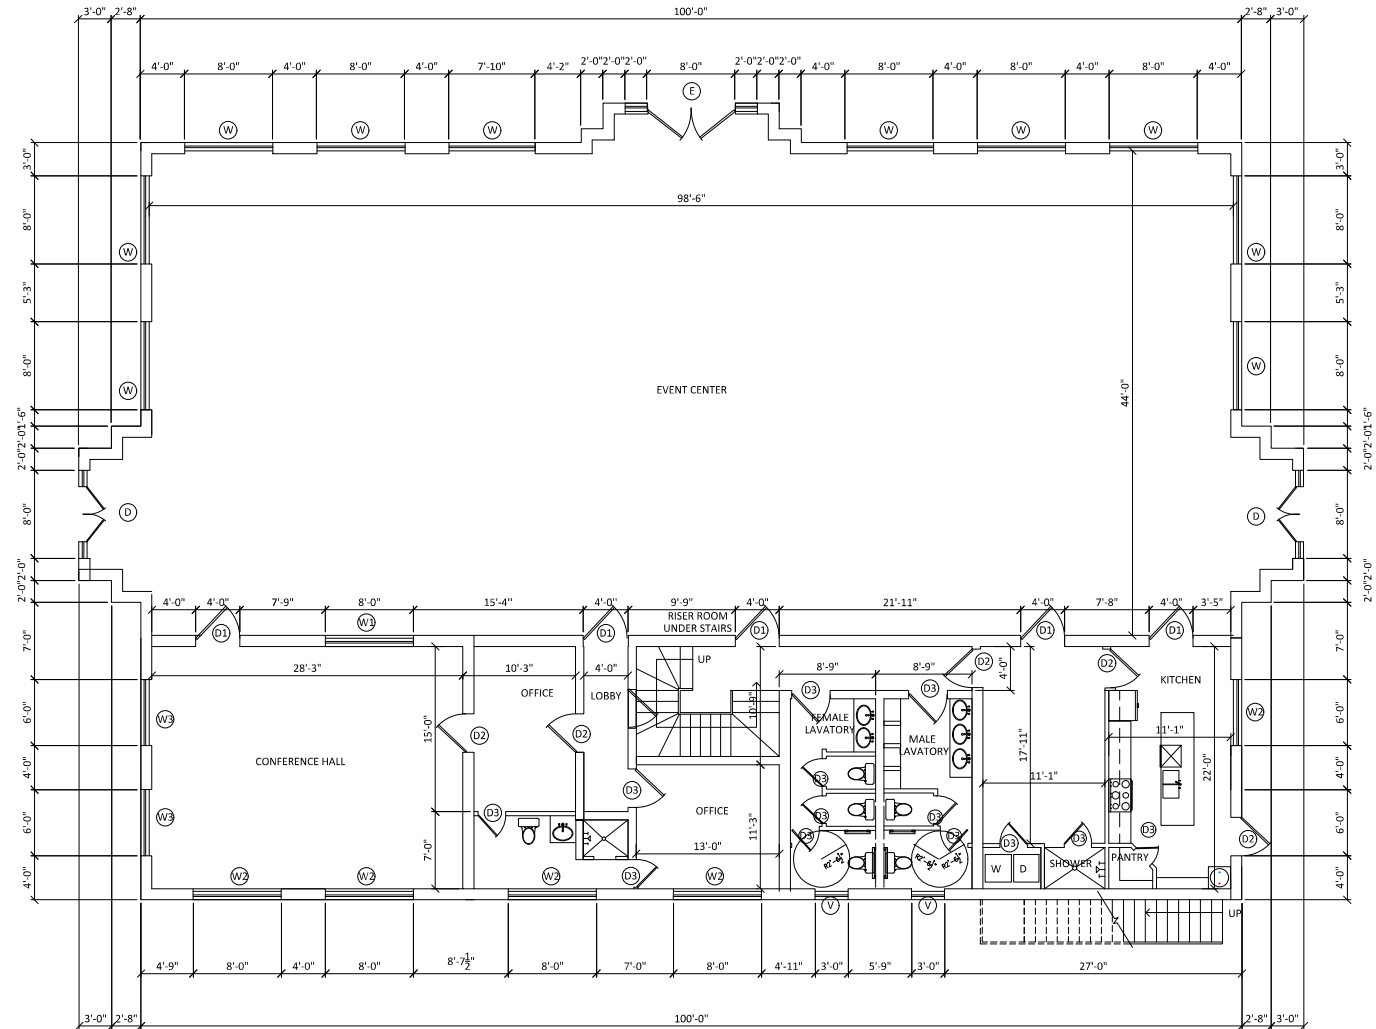

① FIRST FLOOR PLAN

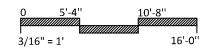

SHEET #	SHEET TITLE	FIRST FLOOR PLAN	DATE	ISSUED FOR	COMMENTS	PROJECT	EVENT CENTER 6321 OAK TIMBER DRIVE, FOREST HILL, TEXAS 76119.	Scale: 3/16" = 1'	Drawn By: R.R.	Page: 1	Date: 07/03/2023